


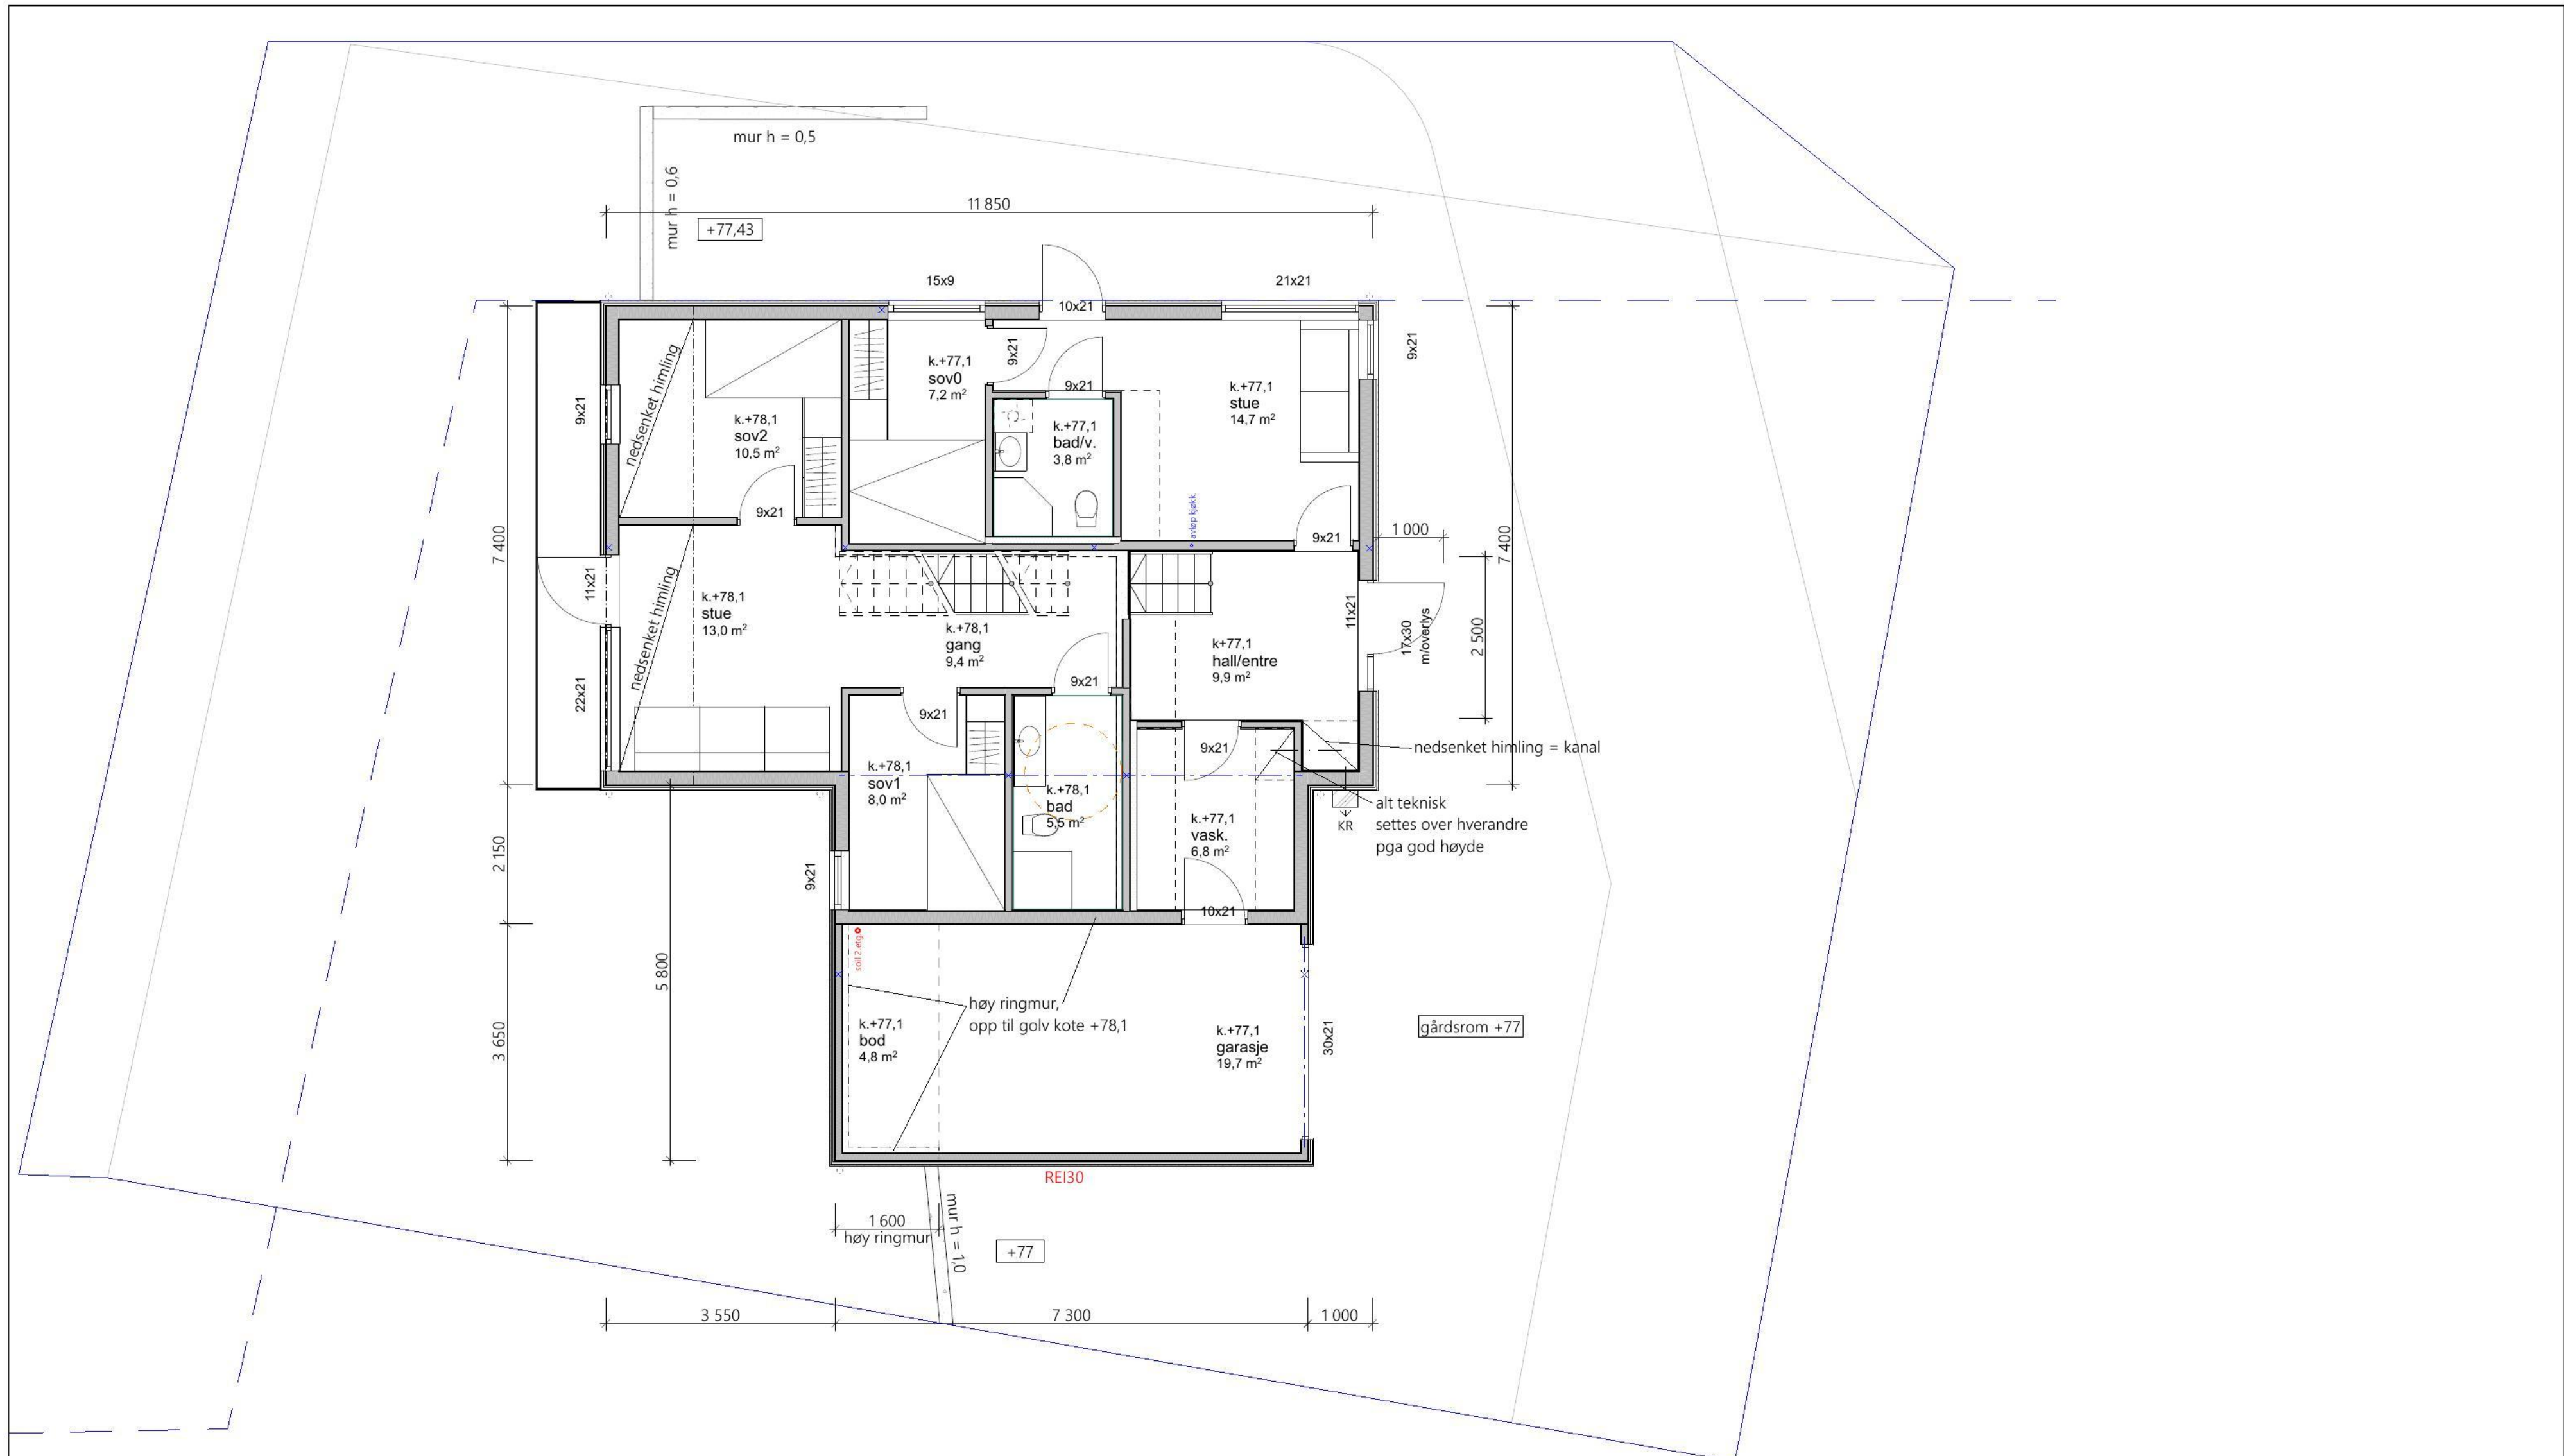

C	justert brutto og netto tomt og BYA bolig	11.01.2024	als	rh
B	justert gesimshøyden og nivå hage	20.12.2023	als	rh
A	BYGGEMELDING	18.12.2023	als	als
Rev	Beskrivelse	Dato	Sign	Kontr

Areal (BYA)		Areal (BRA)	
bolig inkl. garasje/bod	133,6 m²	1.etasje	94,5 m²
parkerings	18,0 m²	2. etasje	111,9 m²
SUM BYA	151,6 m²	SUM	206,4 m²
% BYA (maks 35 %)	35 %		
netto tomt (brutto = 517 m²)	433 m²		

BYGGEMELDING

FJOGSTAD
Etablert 1903
HUS

Byggherre: Fjogstad & Forny AS			
Bygglass: ULLANDHAUGVEIEN 91 Stavanger kommune			
Ark.:	als	G.nr.:	24
Tegner:	als	B.nr.:	359
Målestokk:	1:100	Prosjekt nr.:	17914
Dato:	24.11.2023	Tegningsnummer:	1 etasje
		Rev.:	C