


TEGNINGSNUMMER
A22-106



REVISJONSNUMMER

TYPE TEGNING

Hullet bak
carport?

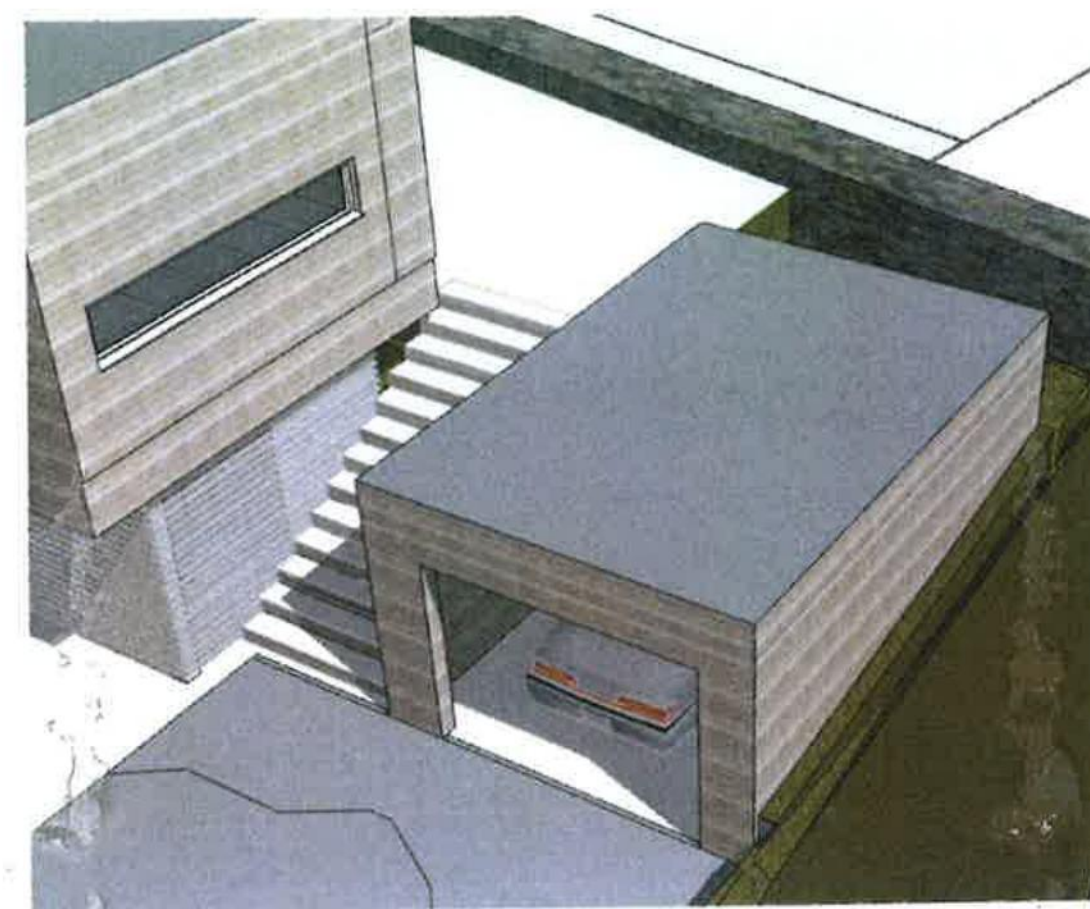

Garasje
Bod en etasje
på taket av
garasjen.

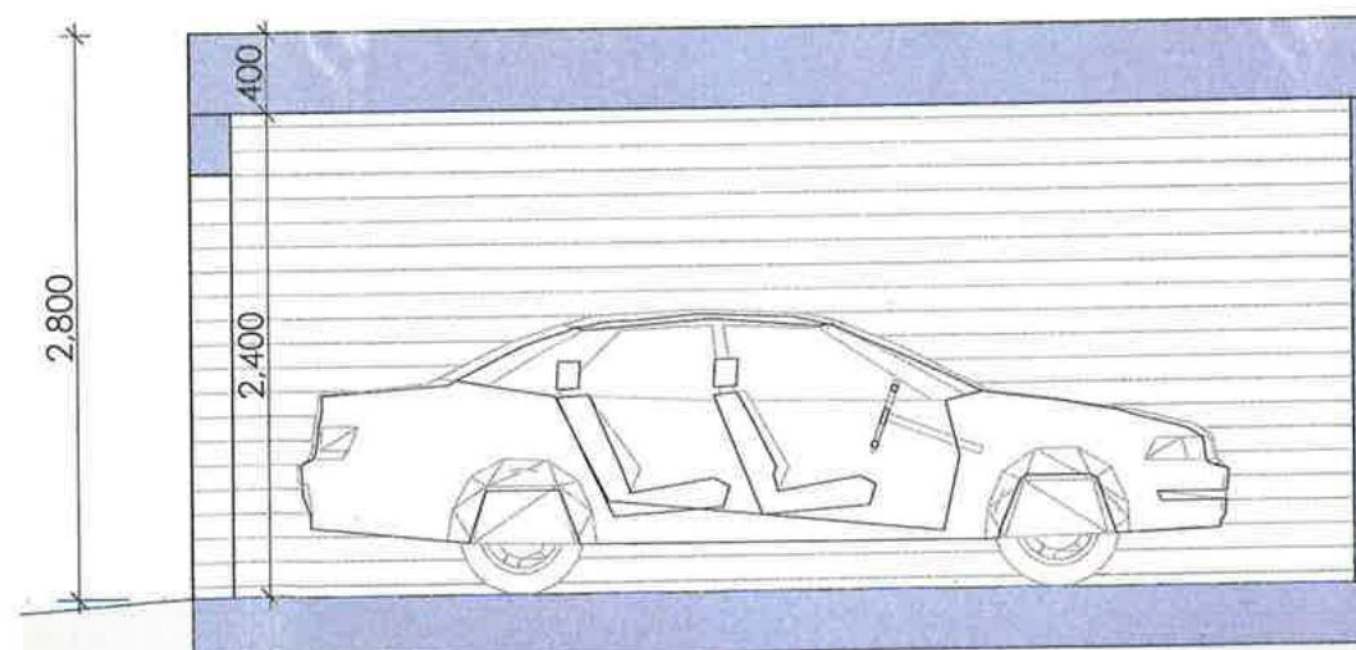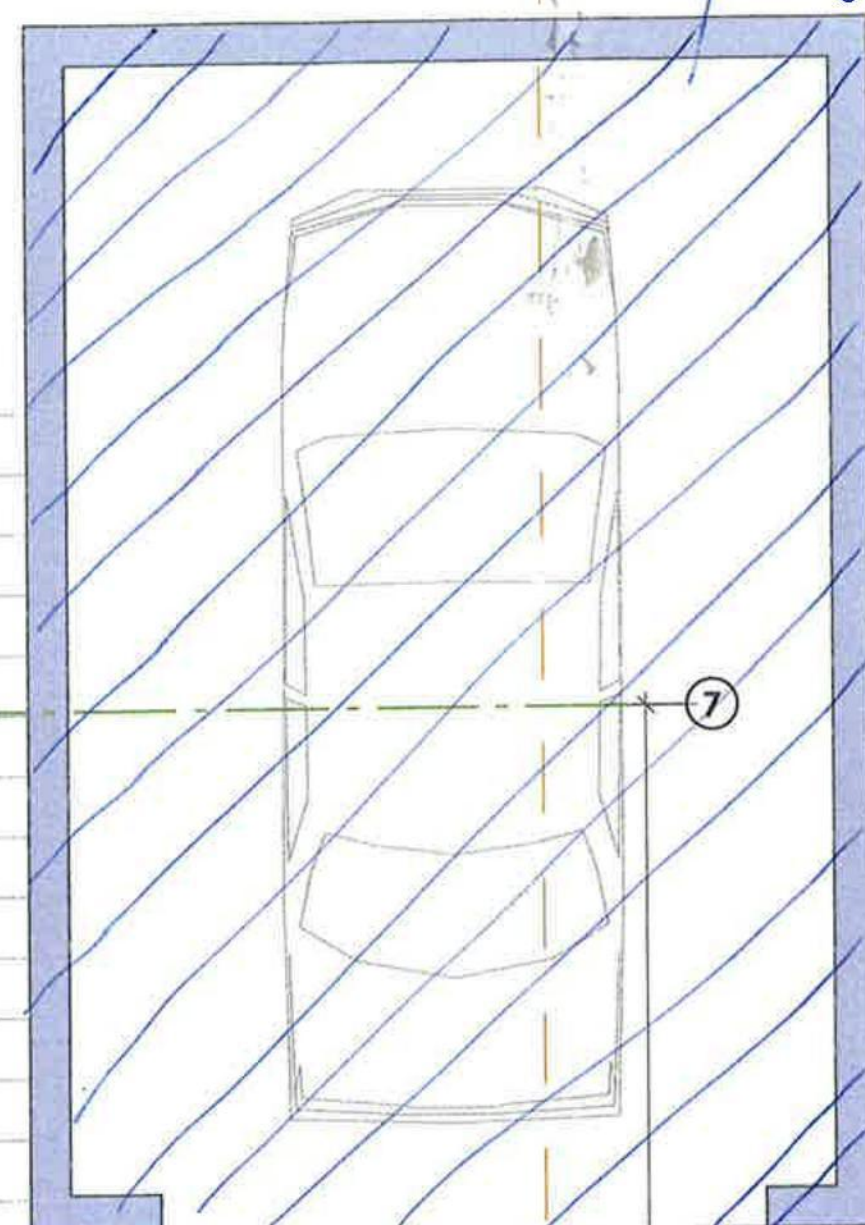

D-30 x 21

Taktekning fjernes

tak isoleres og bod bygges opp. Nytt tak samme konstruksjon som dagens garasjetak.

Snitt G

1:50

1. etasje

Index	Dato	Beskrivelse	Sign
-------	------	-------------	------

LOKALISERINGSFIGUR



Prosjekteringsgruppen:

- **ARK:** ak2 sivilarkitekt mna AS
- **RIB:** Rådg. ing. Bygg
- **RIE:** Rådg. ing. Elektro
- **RIV:** Rådg. ing. Vent.

Nylarget 1
4012 Stavanger
mob: 40872885

veien 0
0000 Stedst

Tlf. 00 00 00 00

Fax. 00 00 00 00

veien 0
0000 Stedst

Tlf. 00 00 00 00

Fax. 00 00 00 00

veien 0
0000 Stedst

Tlf. 00 00 00 00

Fax. 00 00 00 00

Fase:

Forprosjekt

Prosjektnummer:

ak2 - 024

Tittel:

Soltunveien 21
gnr 28 bnr 152
Stavanger

Birte Noer Borrevik

Tegningsnummer: A22-106

TYPE TEGNING:

Carport

Godkjent

Kontroll prosjekt.

Sign. Kontroll

Finnavn

ak2-024.12

12.12.13

Dato

13.09.2013

Målestokk

1:50

Kontroll utførende

Sign. Kontroll

Prosjektør, for

prosjekterende/

lev.