


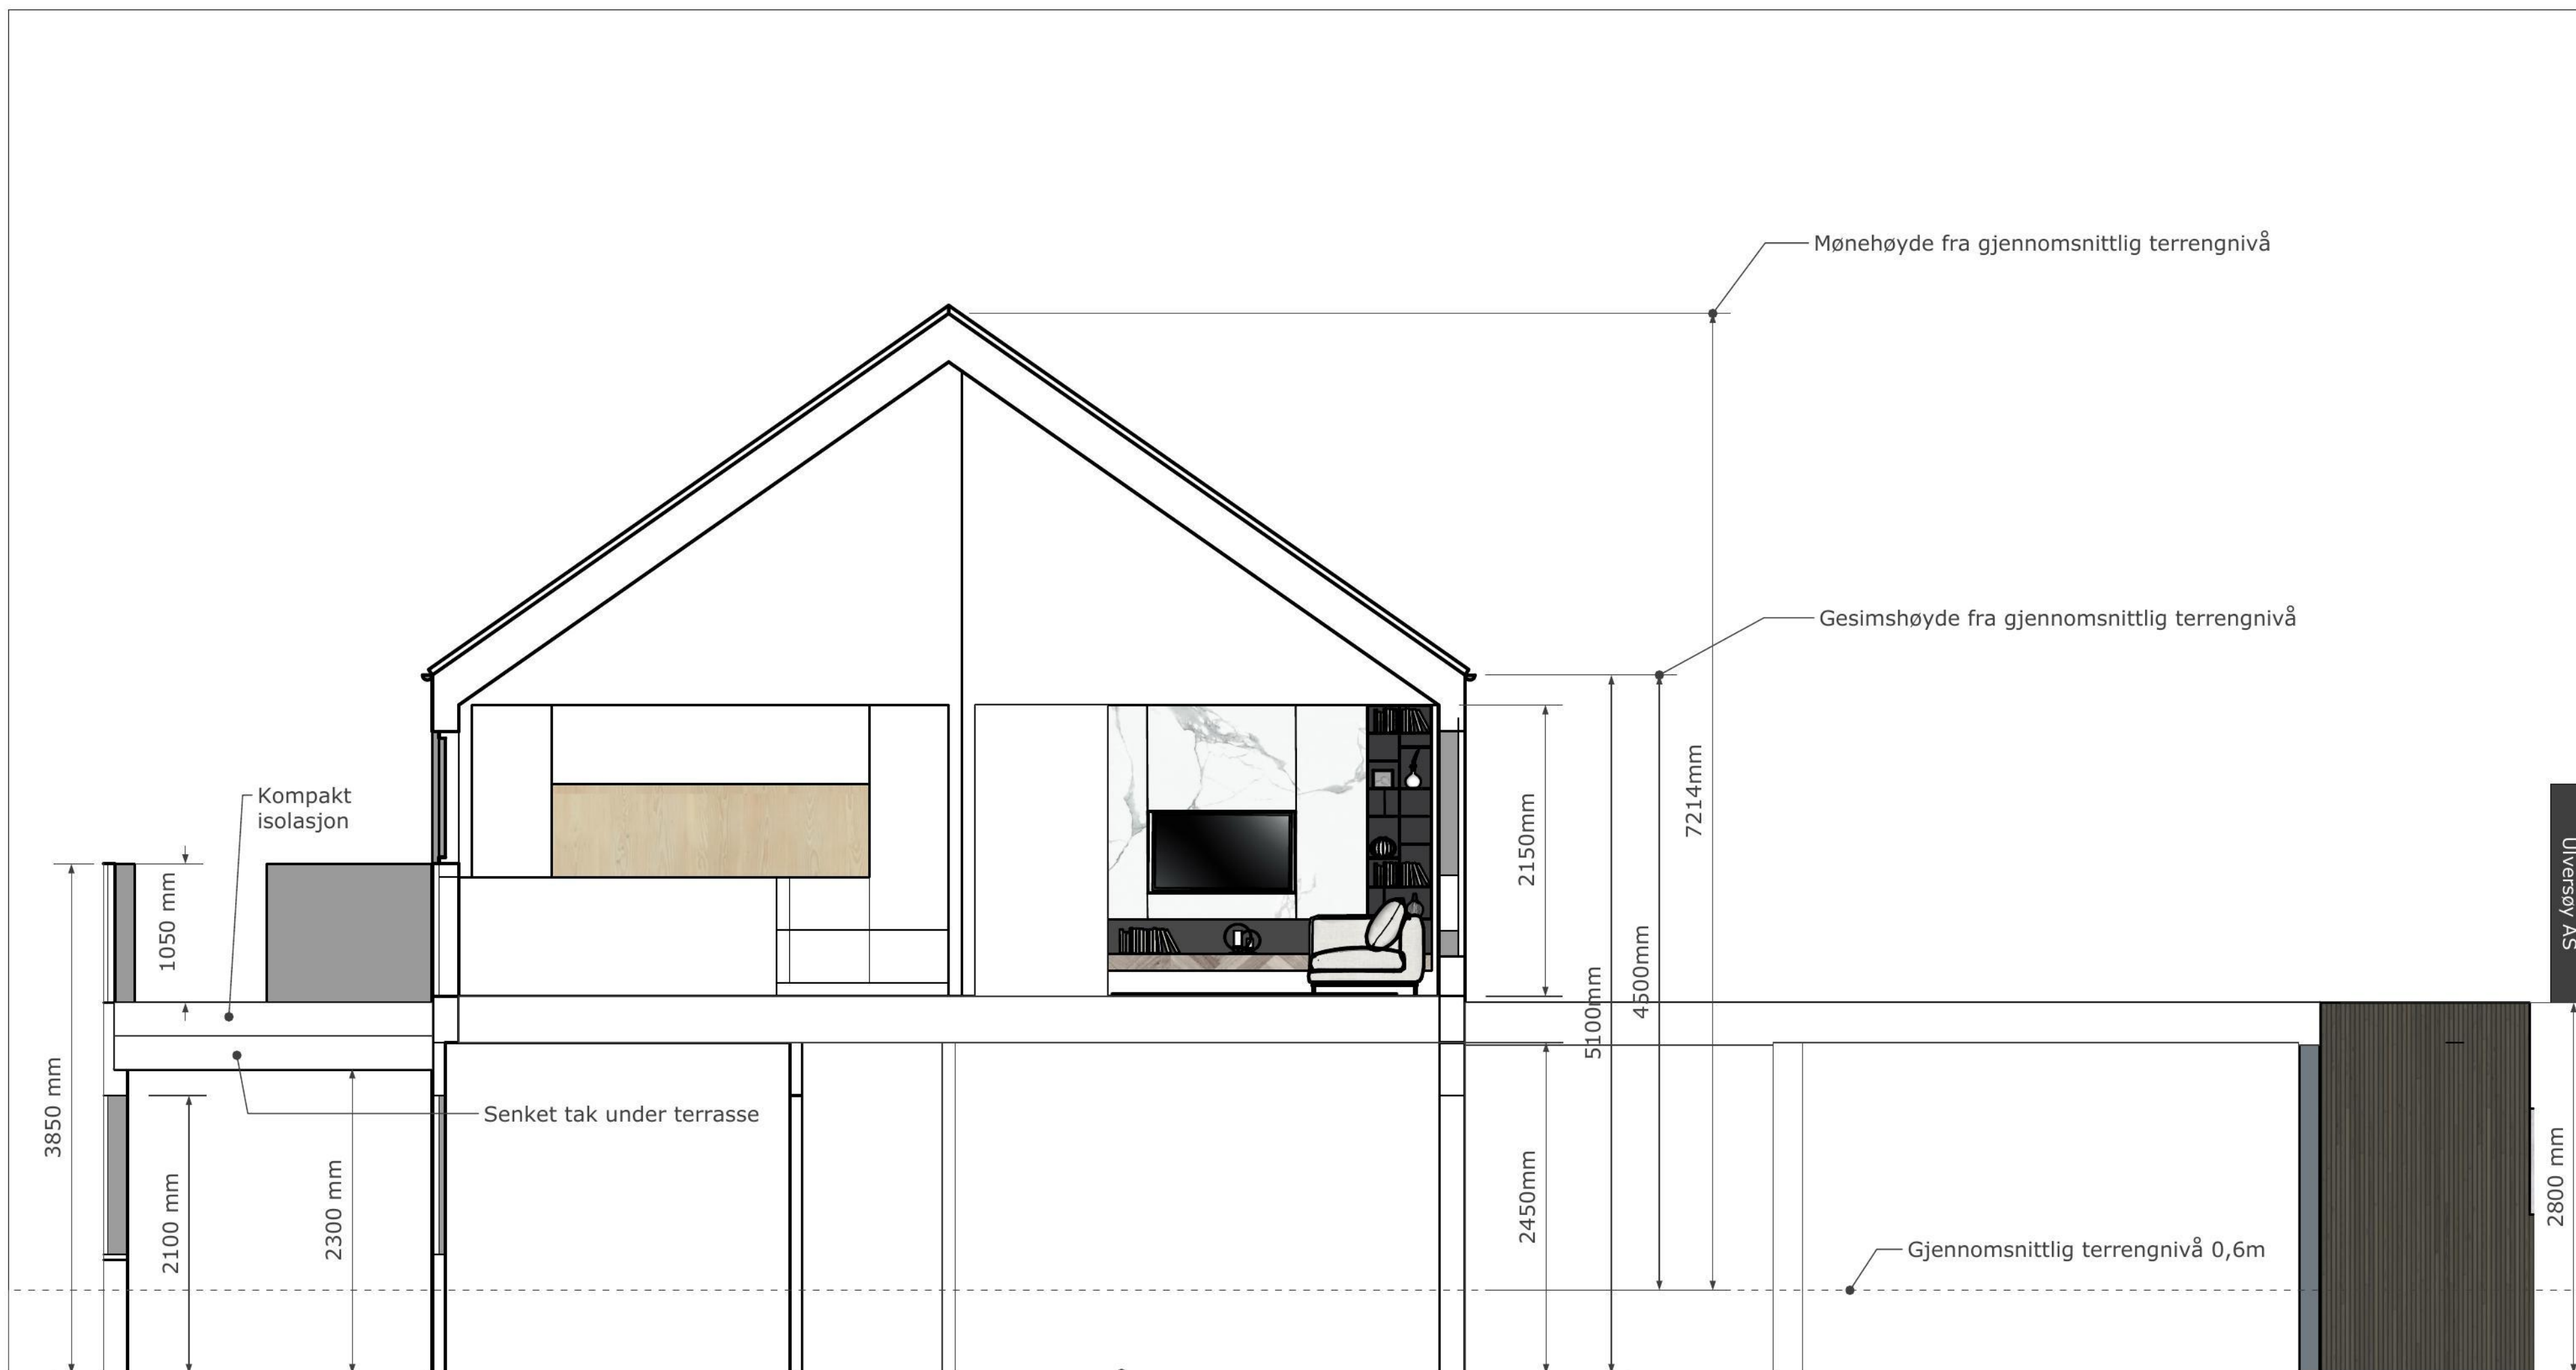

Topp gulv ca. samme høyde som Vedeveien 27 i 1.etg

Gjennomsnittlig terrengnivå = (Lengde hus x høyde terreng) / Lengde hus

Nord : 7,8m x 1,8m

Øst: 0,9m x 1,2m + 12,6m x 0m

Sør: 3,9m x 0m + 3,4m x 0m + 5,5m x 0m

Vest: 5,3m x 0m + 2,5m x 1m + 9,5m x (1,8+1)/2

$$\frac{30,92m \times m}{51,4m} = 0,6m \text{ gjennomsnittlig terrenghøyde}$$

Total Lengde hus = 51,4m

Snitt mot sør
Målestokk 1:50
Format: A3

desember 29, 2023

Vedeveien 29 | Enebolig med leilighet

A 01