


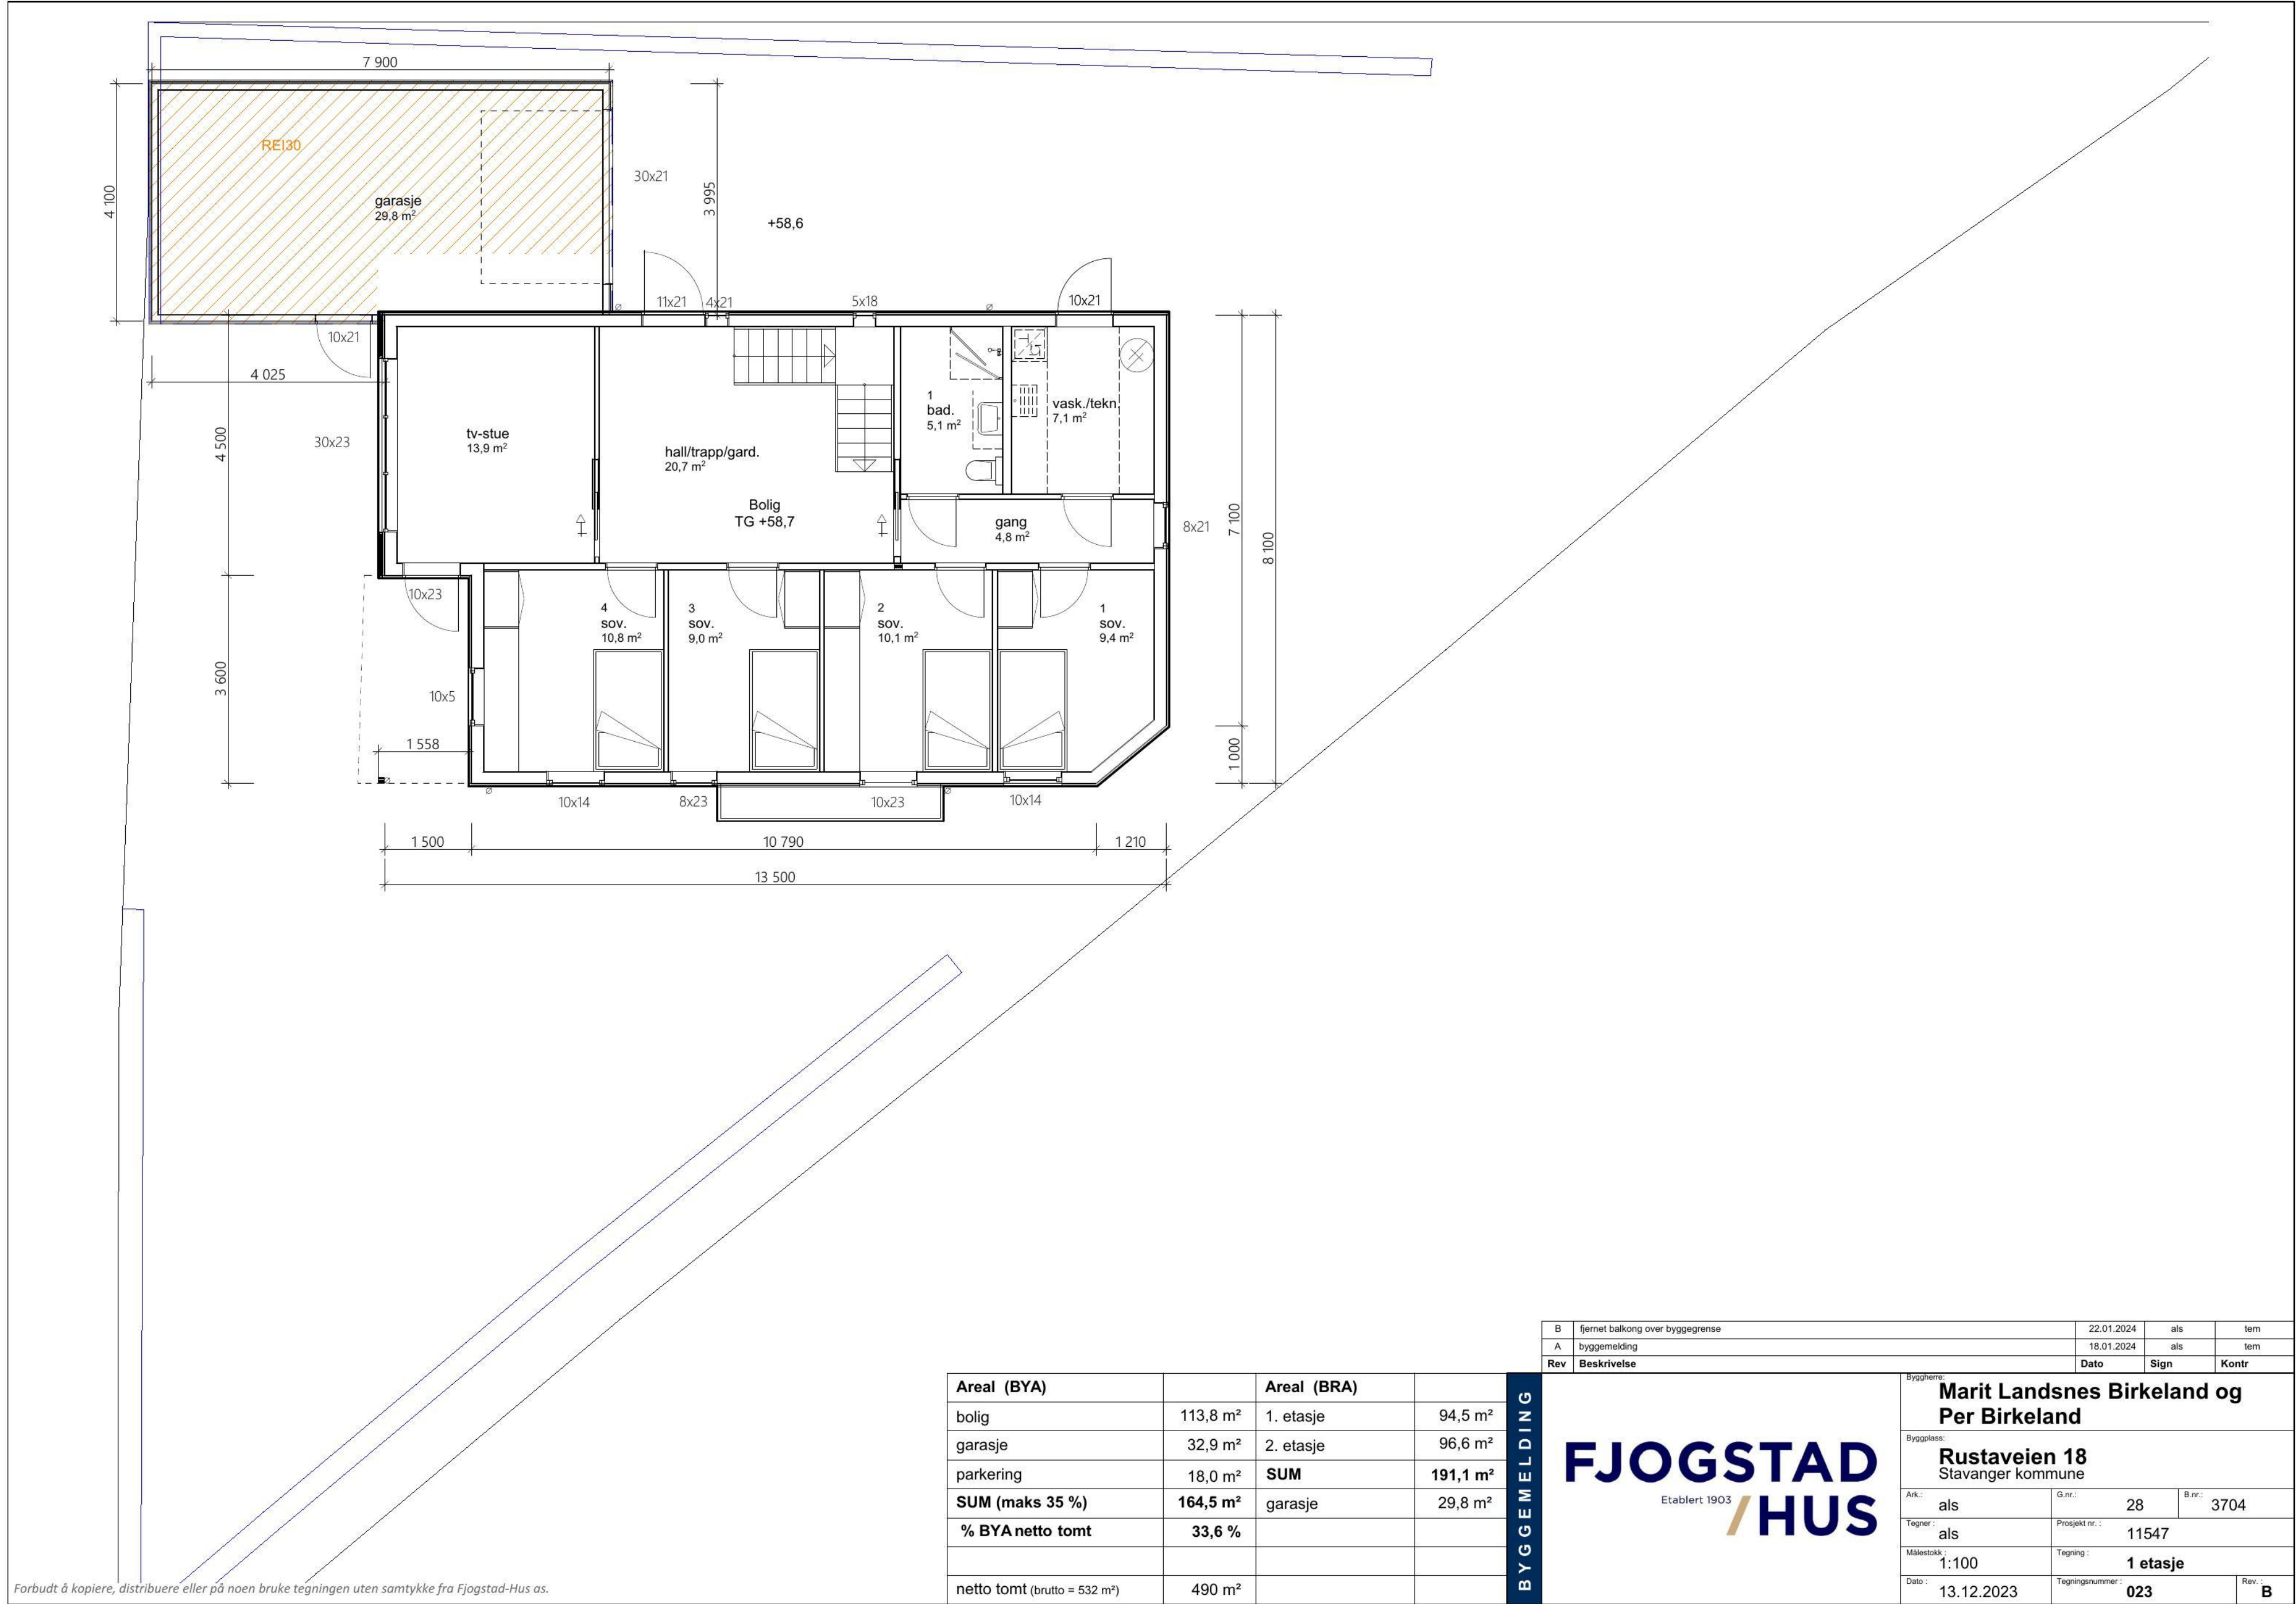

Forbudt å kopiere, distribuere eller på noen bruke tegningen uten samtykke fra Fjogstad-Hus as.

Areal (BYA)		Areal (BRA)	
bolig	113,8 m²	1. etasje	94,5 m²
garasje	32,9 m²	2. etasje	96,6 m²
parkering	18,0 m²	SUM	191,1 m²
SUM (maks 35 %)	164,5 m²	garasje	29,8 m²
% BYA netto tomt	33,6 %		
netto tomt (brutto = 532 m²)	490 m²		

B	fjernet balkong over byggegrense	22.01.2024	als	tem
A	byggemelding	18.01.2024	als	tem
Rev	Beskrivelse	Dato	Sign	Kontr
Byggherre: Marit Landsnes Birkeland og Per Birkeland				
Bygglass: Rustaveien 18 Stavanger kommune				
Ark.:	als	G.nr.:	28	B.nr.: 3704
Tegner:	als	Prosjekt nr.:	11547	
Målestokk:	1:100	Tegning:	1 etasje	
Dato:	13.12.2023	Tegningsnummer:	023	Rev.: B