



Stavanger kommune


Situasjonskart

Eiendom: 29/218
Adresse: Osebergveien 5A
Dato: 06.11.2023
Målestokk: 1:500

Vedlegg nr. D



UTM-32

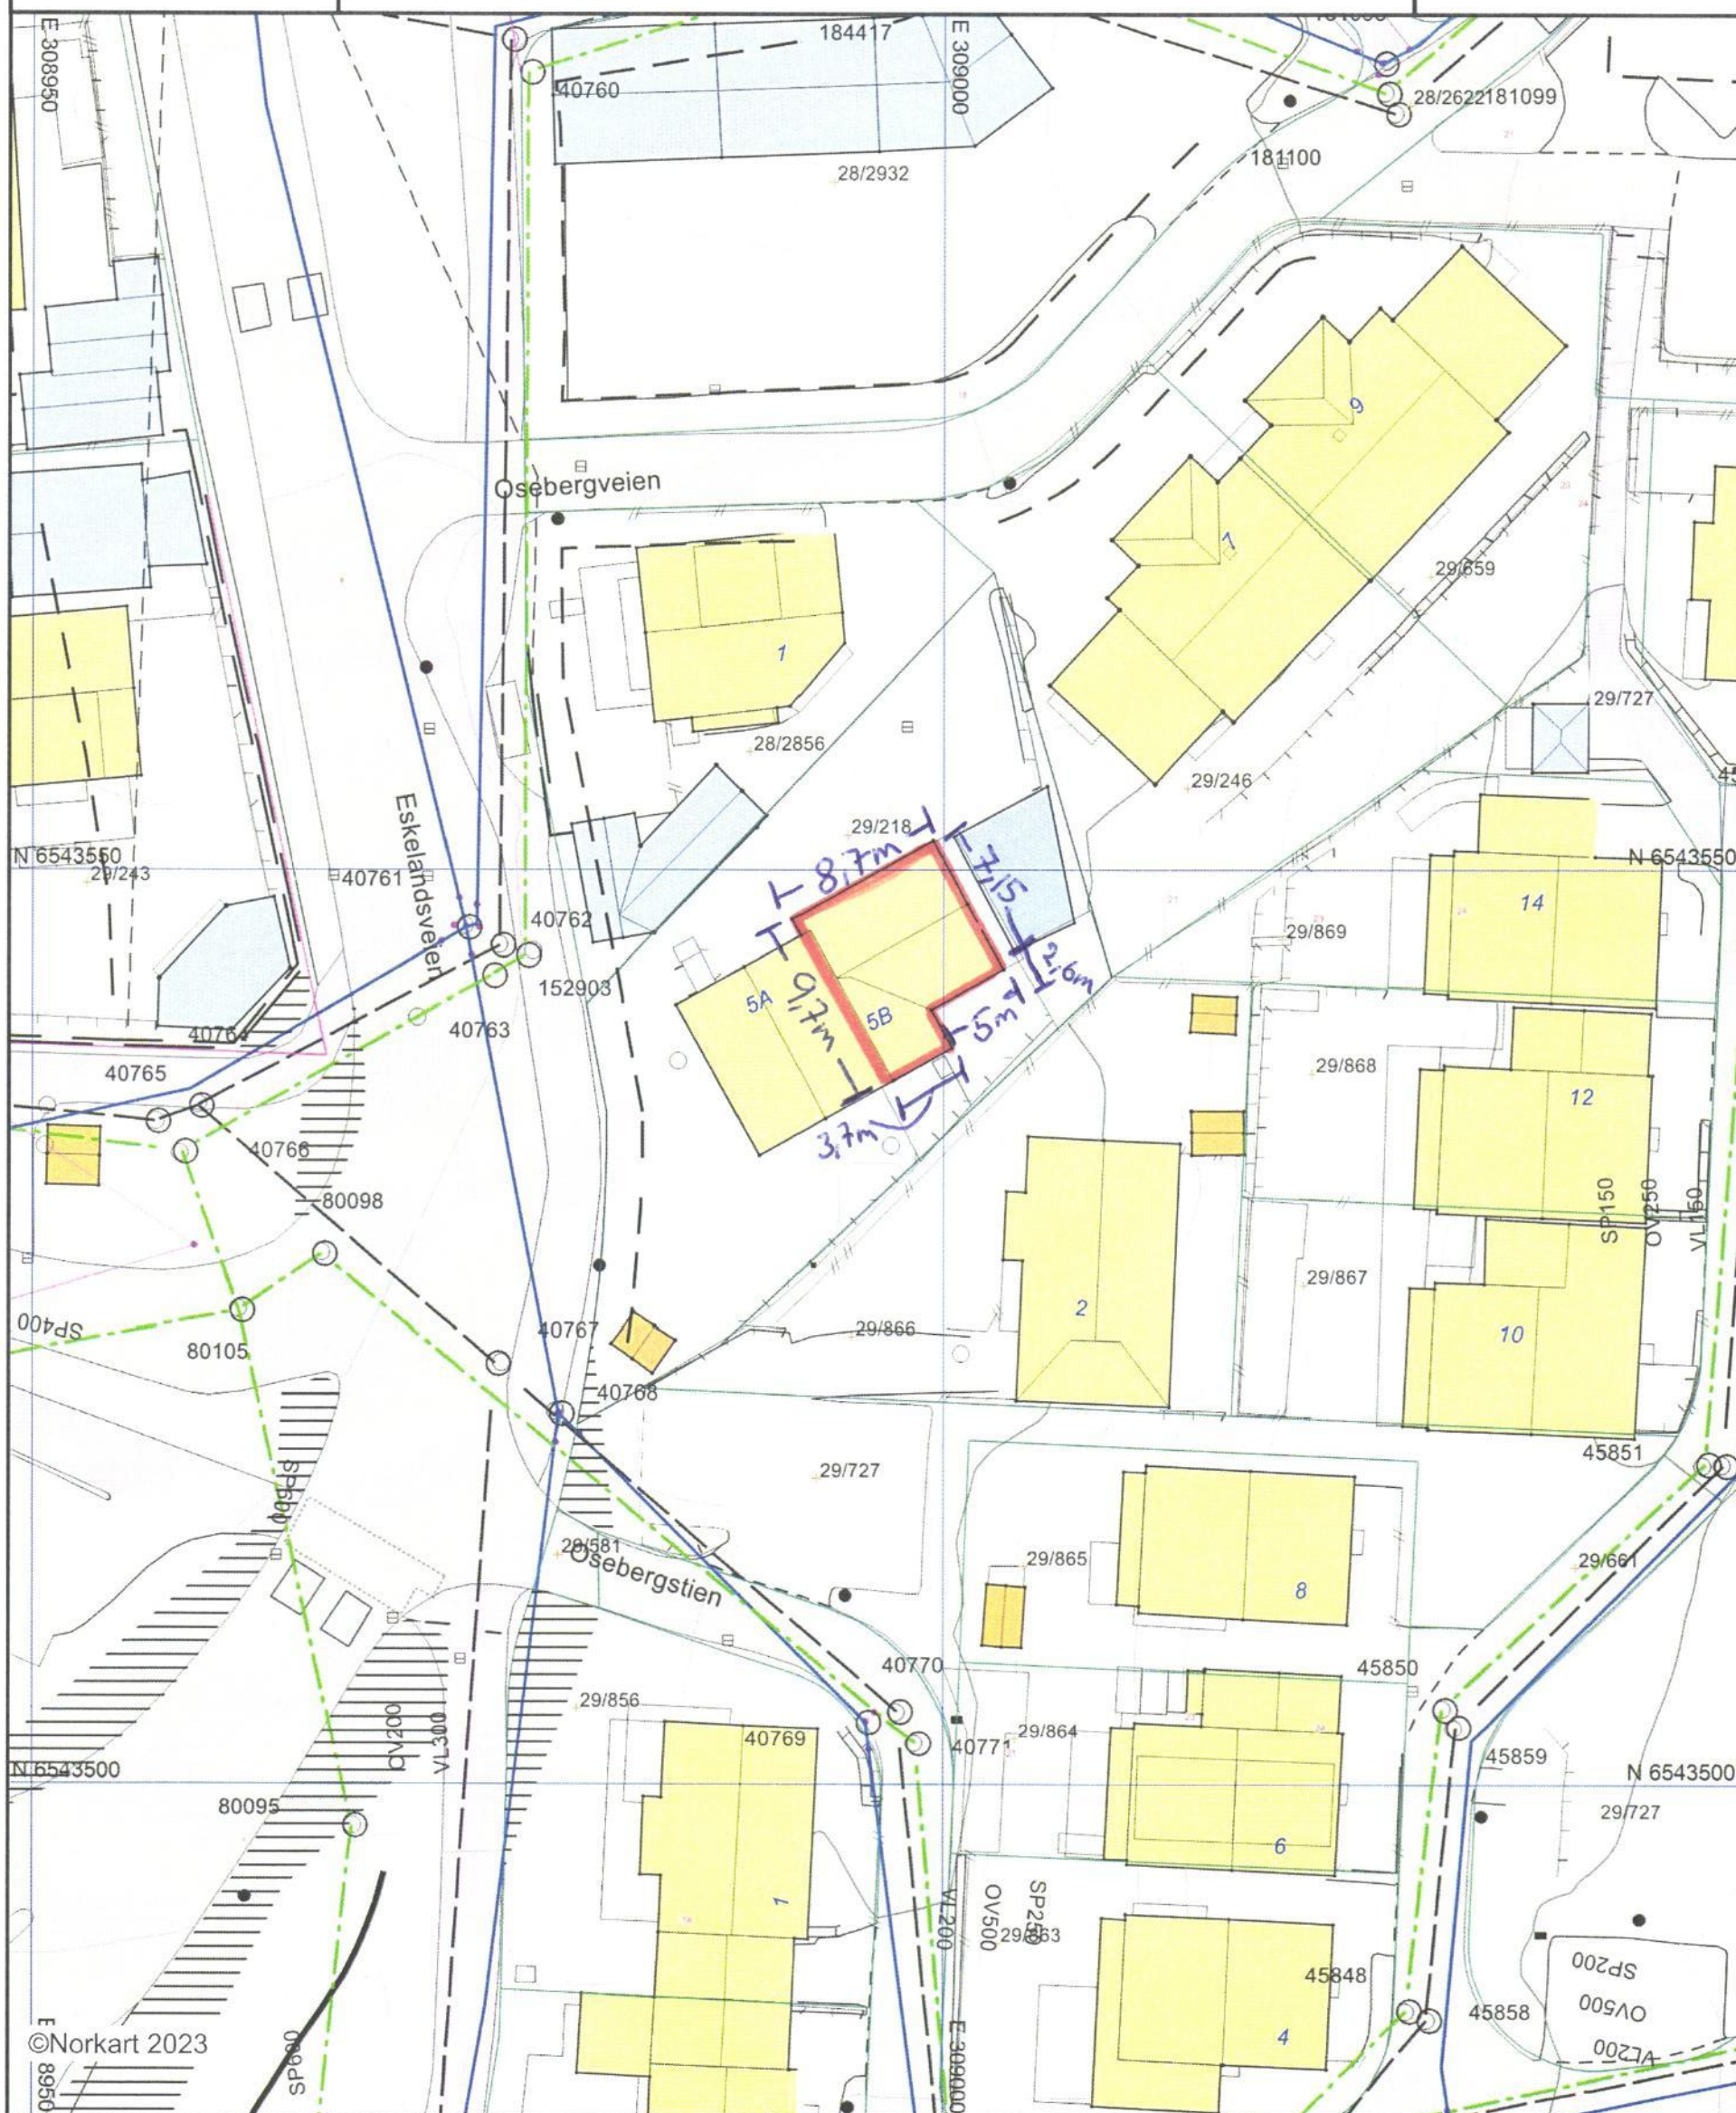

©Norkart 2023

1) Det tas forbehold om feil i kartgrunnlaget
2) Ved utskrift fra PDF-fil kan målestokken bli unøyaktig