


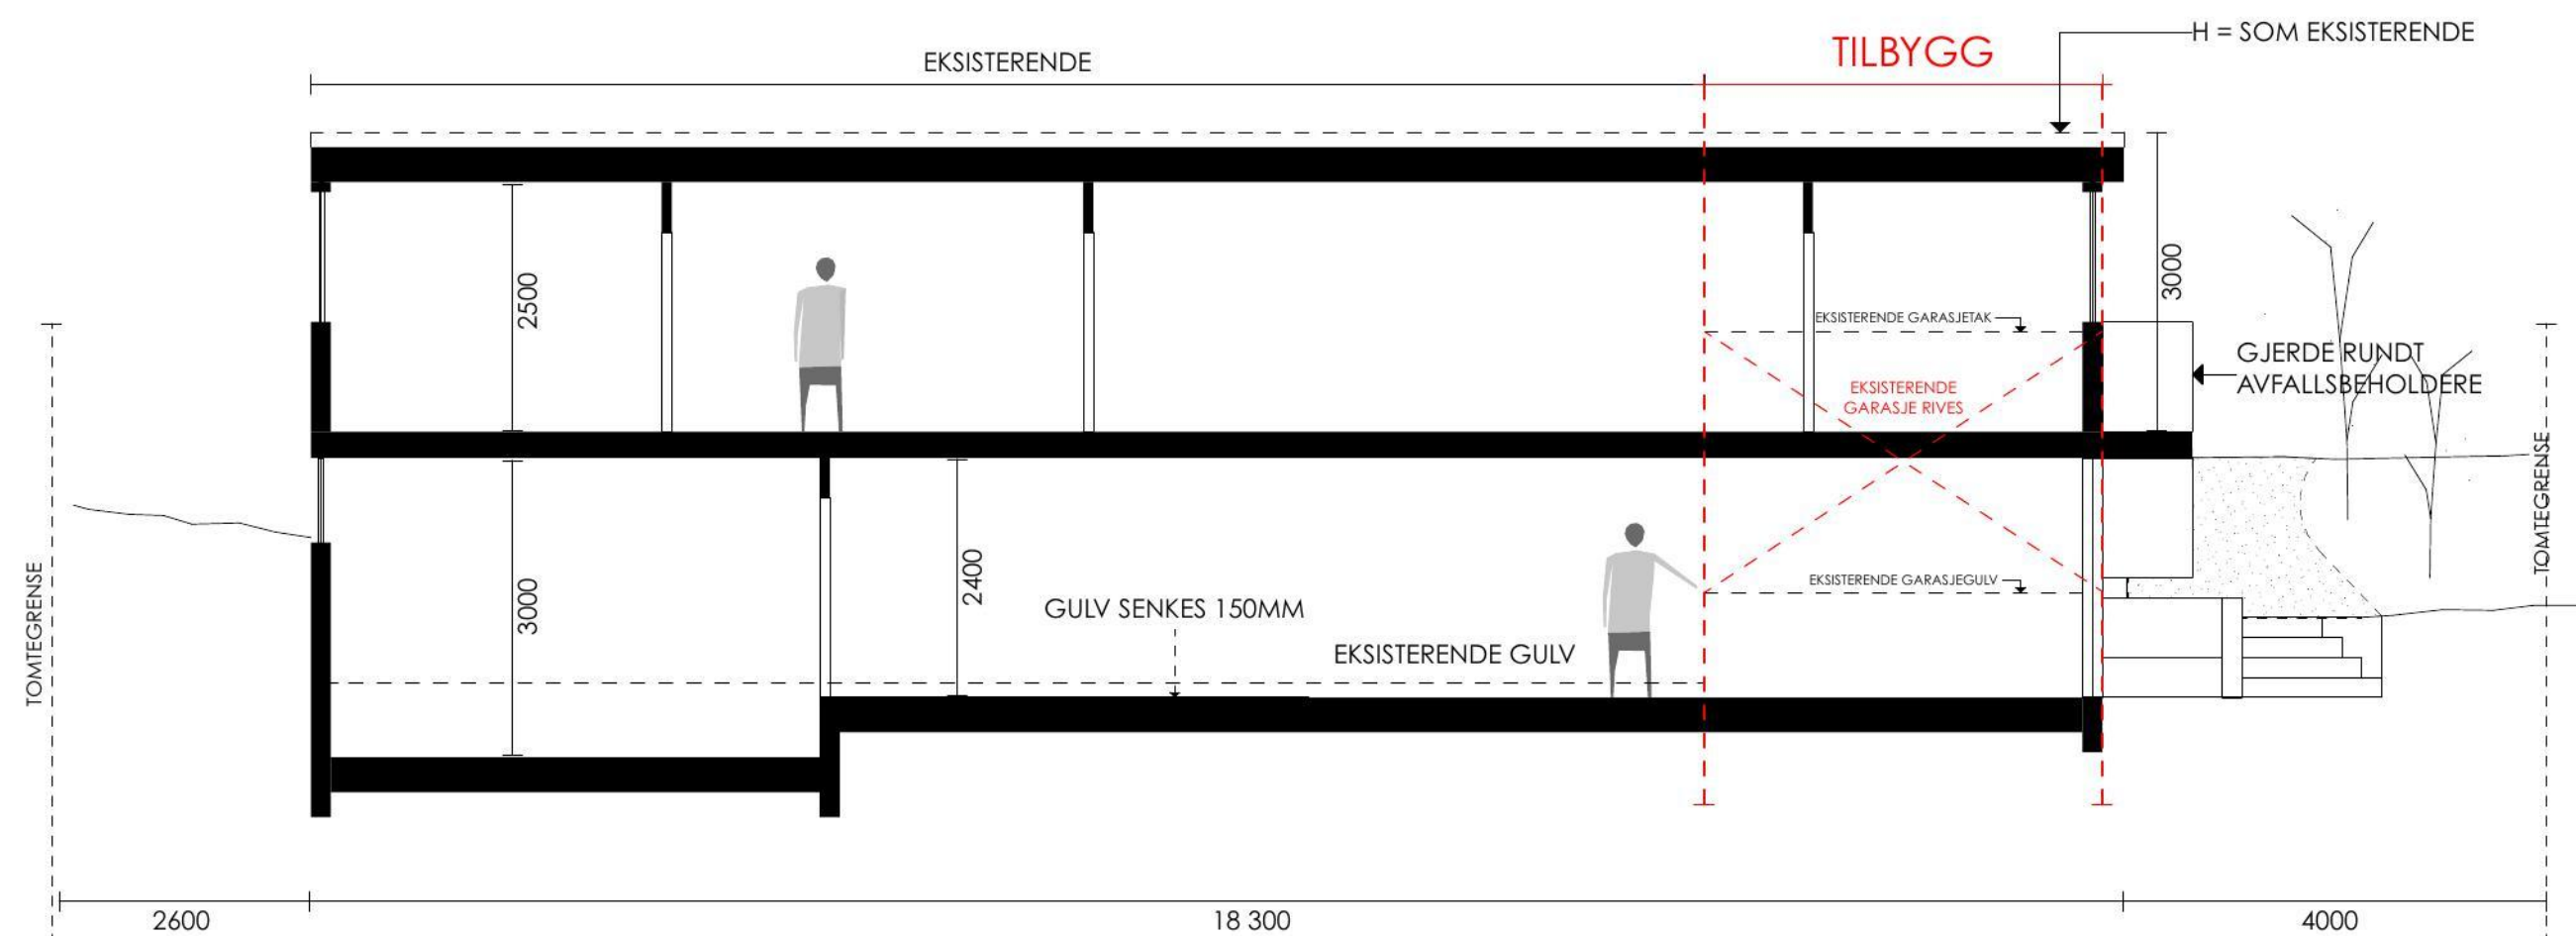

SNITT AA

REV.	DATO	BESKRIVELSE	SIGN.
------	------	-------------	-------

ARK :

Fase: FORPROSJEKT

HAGA & GROV AS
SIVILARKITEKTER MNAL

MARIA AHLQVIST MAX SAMUEL Ragnhildsgata 55 GNR. 38 / BNR. 1525 STAVANGER KOMMUNE	Kontroll prosjekt.	
	Sign.	Kontroll
	JHG	RG
	Filnavn	
Ragnhildsgata 55 GNR. 38 / BNR. 1525 STAVANGER KOMMUNE	Dato	
	06.02.2024	
	Målestokk	
	1:100	

Kontroll utførende	
Sign.	Kontroll

TYPE TEGNING:	Tegn.nr.:	Rev.:
Snitt AA	E4	