



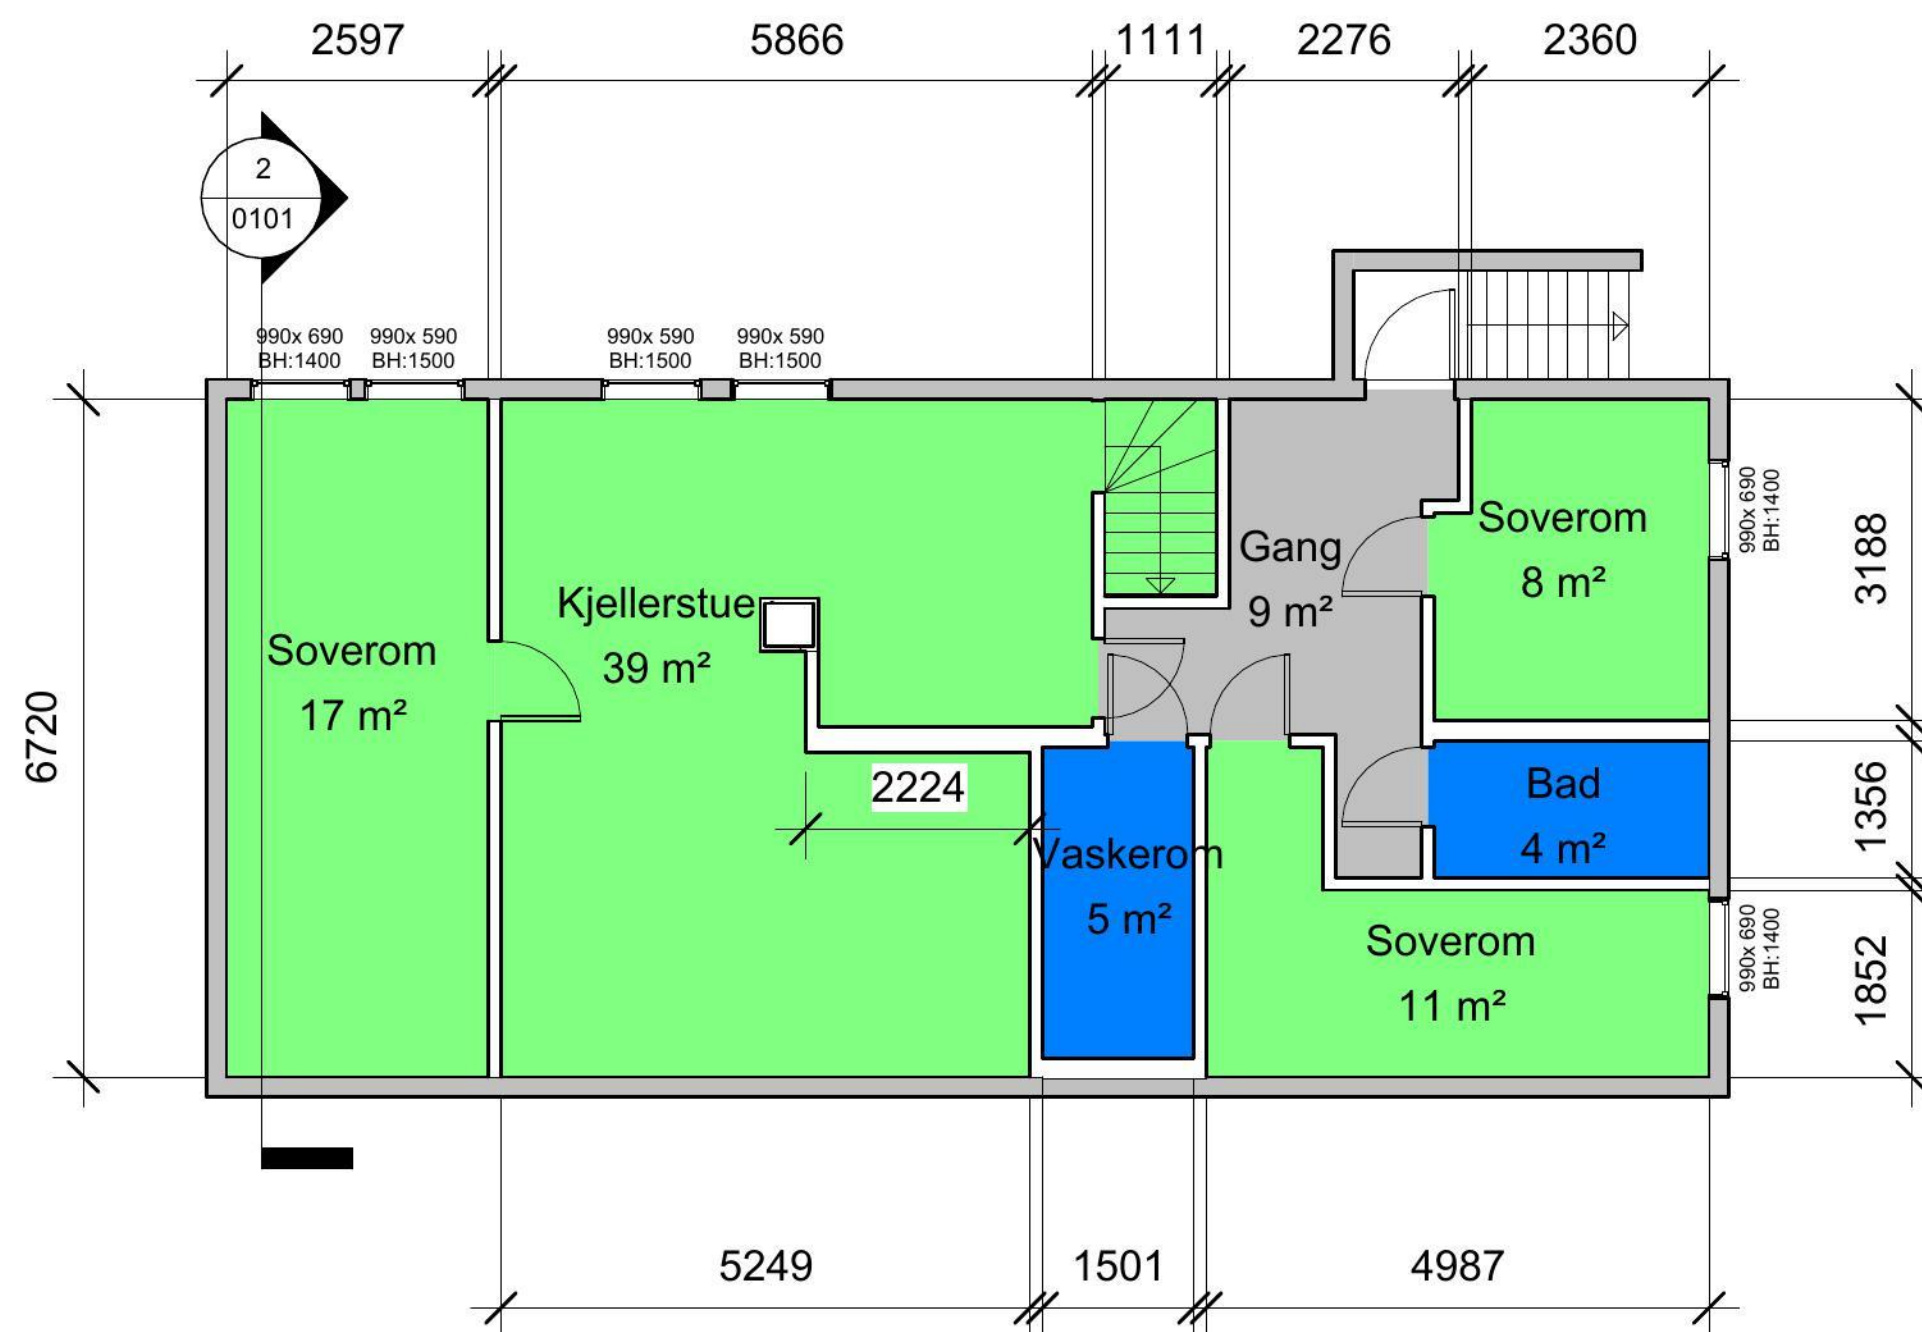

1 Kjeller
1 : 100

Romskjema			
Etasje	Rom	Areal	Kommentar
Kjeller	Soverom	17 m²	Bruksendres fra tilleggsdel til hoveddel
Kjeller	Kjellerstue	39 m²	Bruksendres fra tilleggsdel til hoveddel
Kjeller	Vaskerom	5 m²	Uendret
Kjeller	Gang	9 m²	Uendret
Kjeller	Soverom	8 m²	Bruksendres fra tilleggsdel til hoveddel
Kjeller	Bad	4 m²	Uendret
Kjeller	Soverom	11 m²	Bruksendres fra tilleggsdel til hoveddel

BRA som skal bruksendres: 75 m²

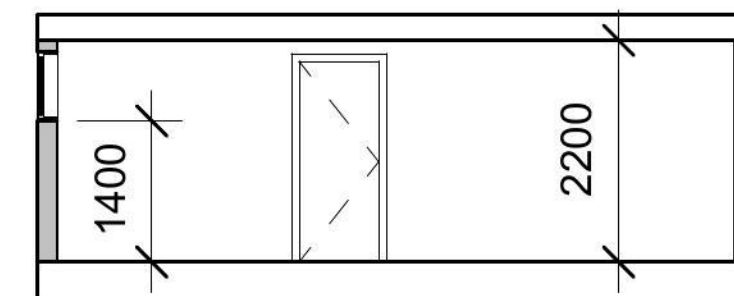

2 Snitt A
1 : 100