



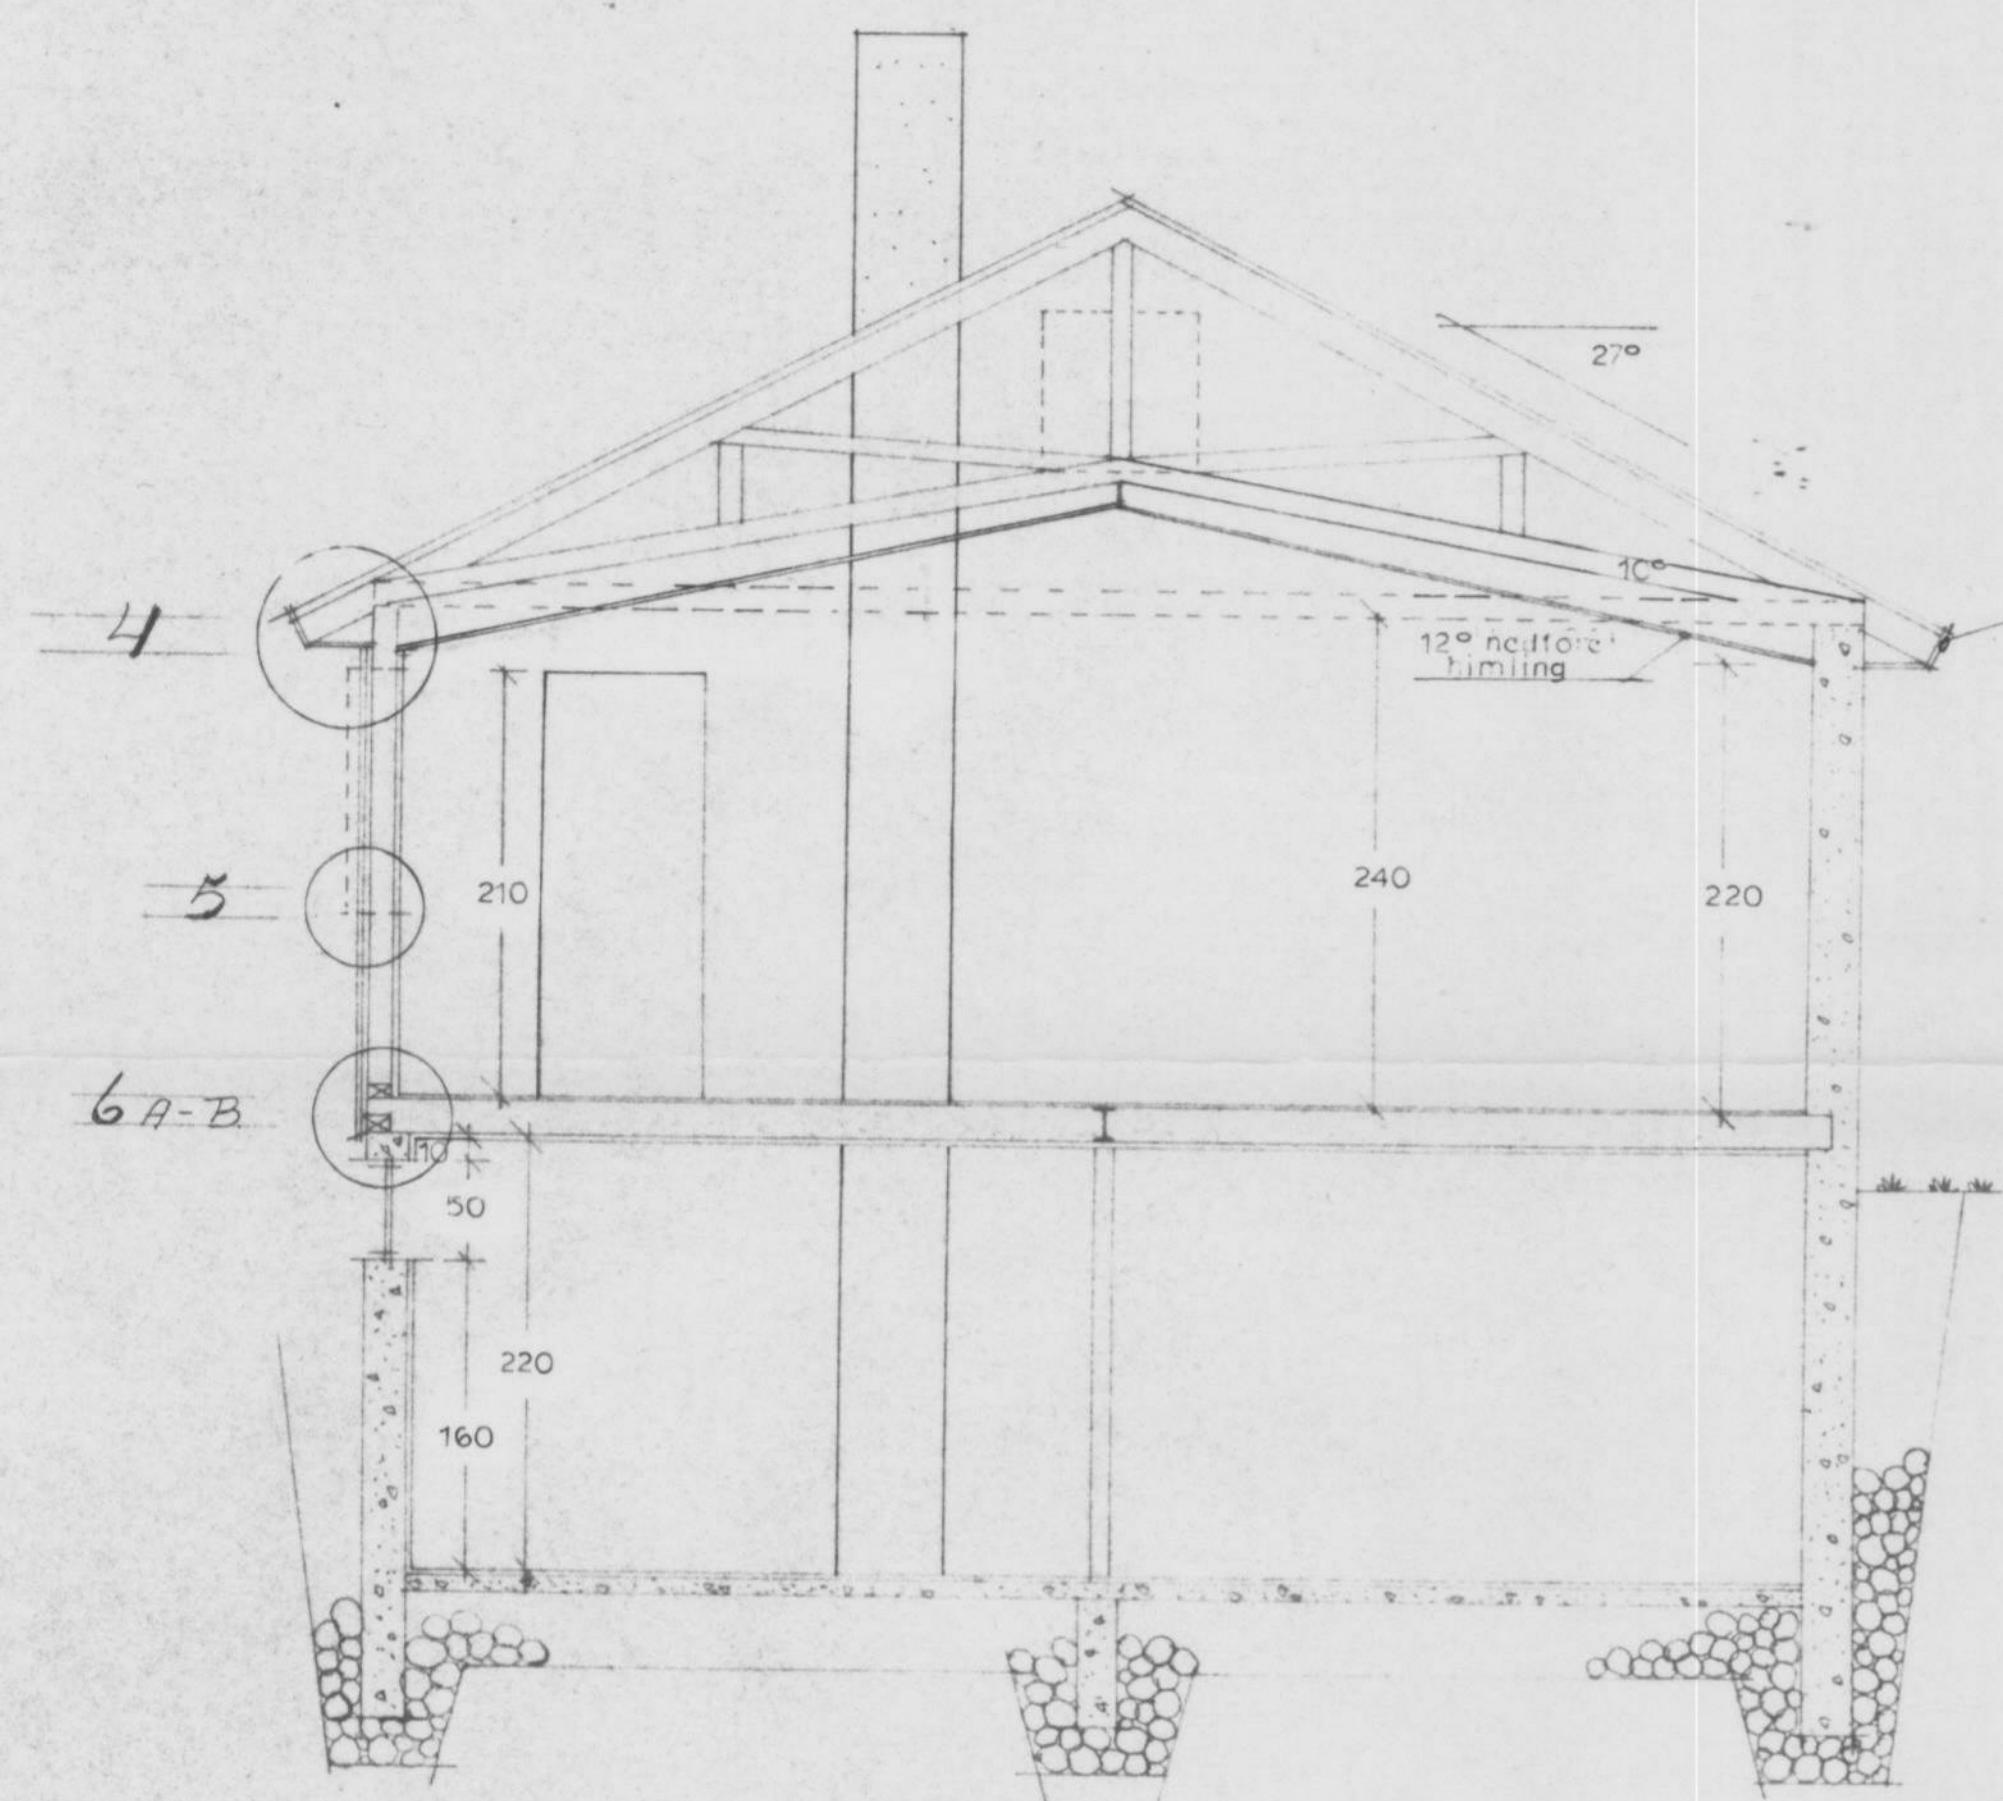

SNITT G. STUEFLØY

NB. EKSPANSJONSKLARING MELLOM  
VINDSKJEL OG PLÅSTRENNE SKAL VÆRE  
MIN 2 CM I HVER ENDE.

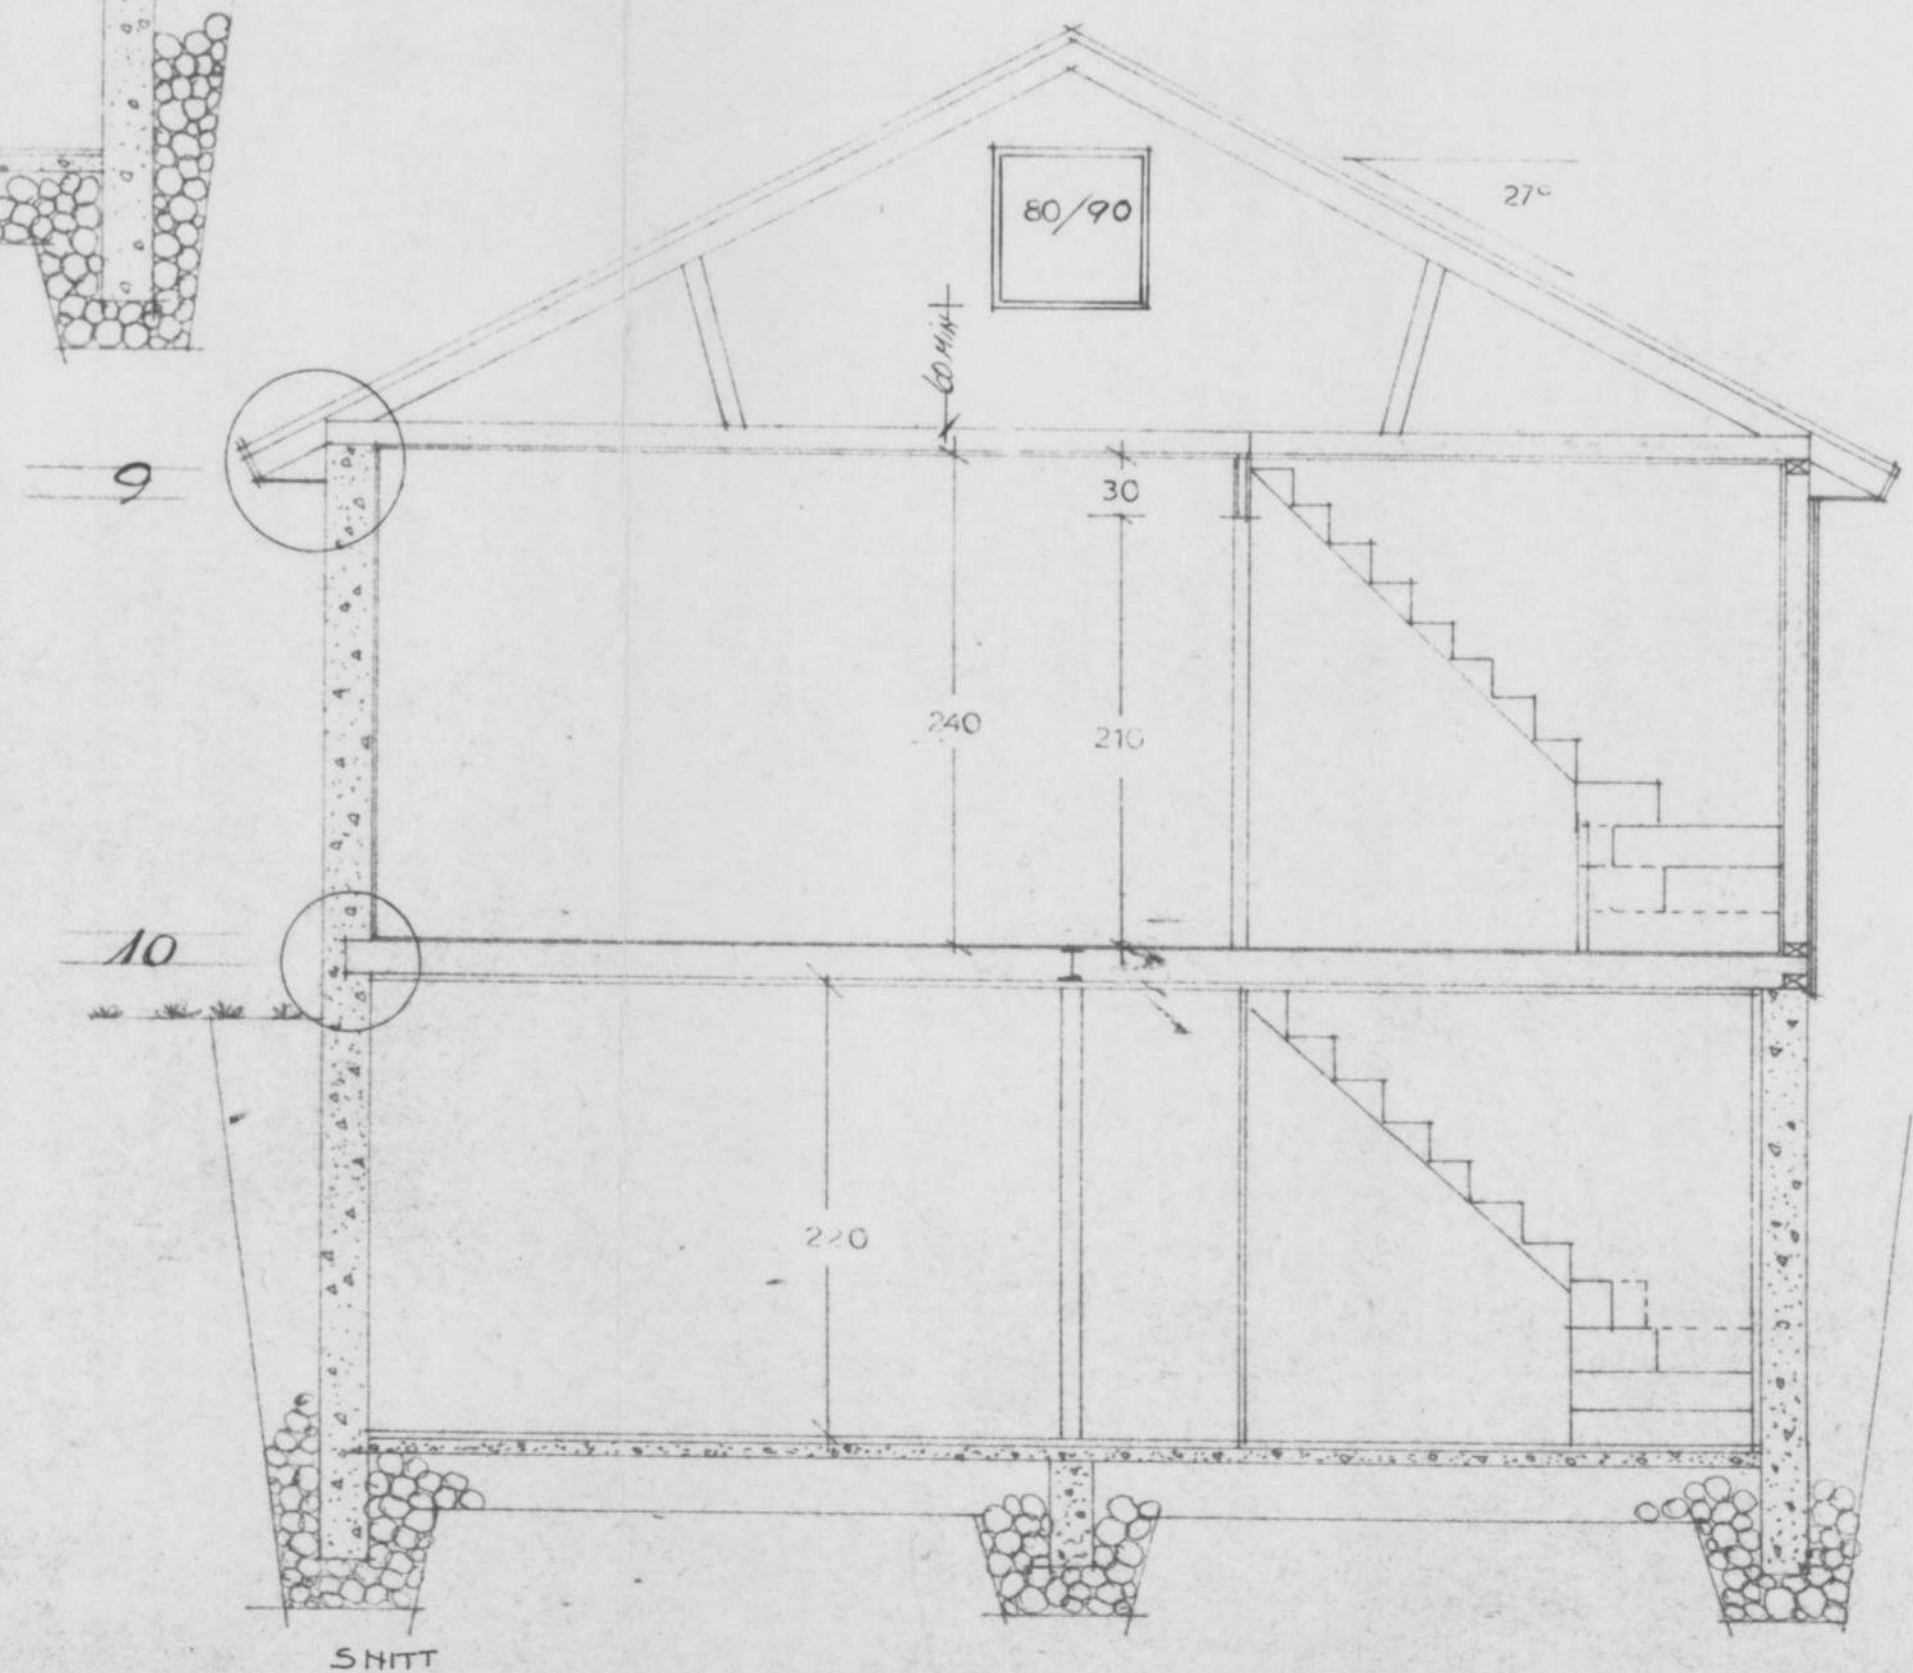

SNITT

|   |  |                                                       |
|---|--|-------------------------------------------------------|
| <b>TEI HUS NR. "HELGE" B</b><br>A/S TEI LAG KOMPANIET • FORUM • TELEFON 20 029   |  | SELVBYGGERLAGET<br>"HELGE" B                          |
| BYGGERIET:   |  | SKALA: 1:50<br>DATO: 17.6.69 9-9-69<br>RETTET 20.1.70 |
| NETTO LE AREAL: 84,8 m <sup>2</sup><br>BRUTTO GR. FLATE:   |  | SIGN.: JH. EJ.                                        |
| <small>         Disse tegninger kan kun benyttes med tillatelse fra Tei Lagskompaniet, og må ikke kopieres, fotokopieres eller gjengis i andre uten tillatelse. Tegningene er utarbeidet for eget bruk.       </small> |  |                                                       |

Stavanger Kommune  
 BYGNINGSSETATEN  
 9. SEP 1970  
 Arkiv nr. 503.1  
 J. nr. 258