


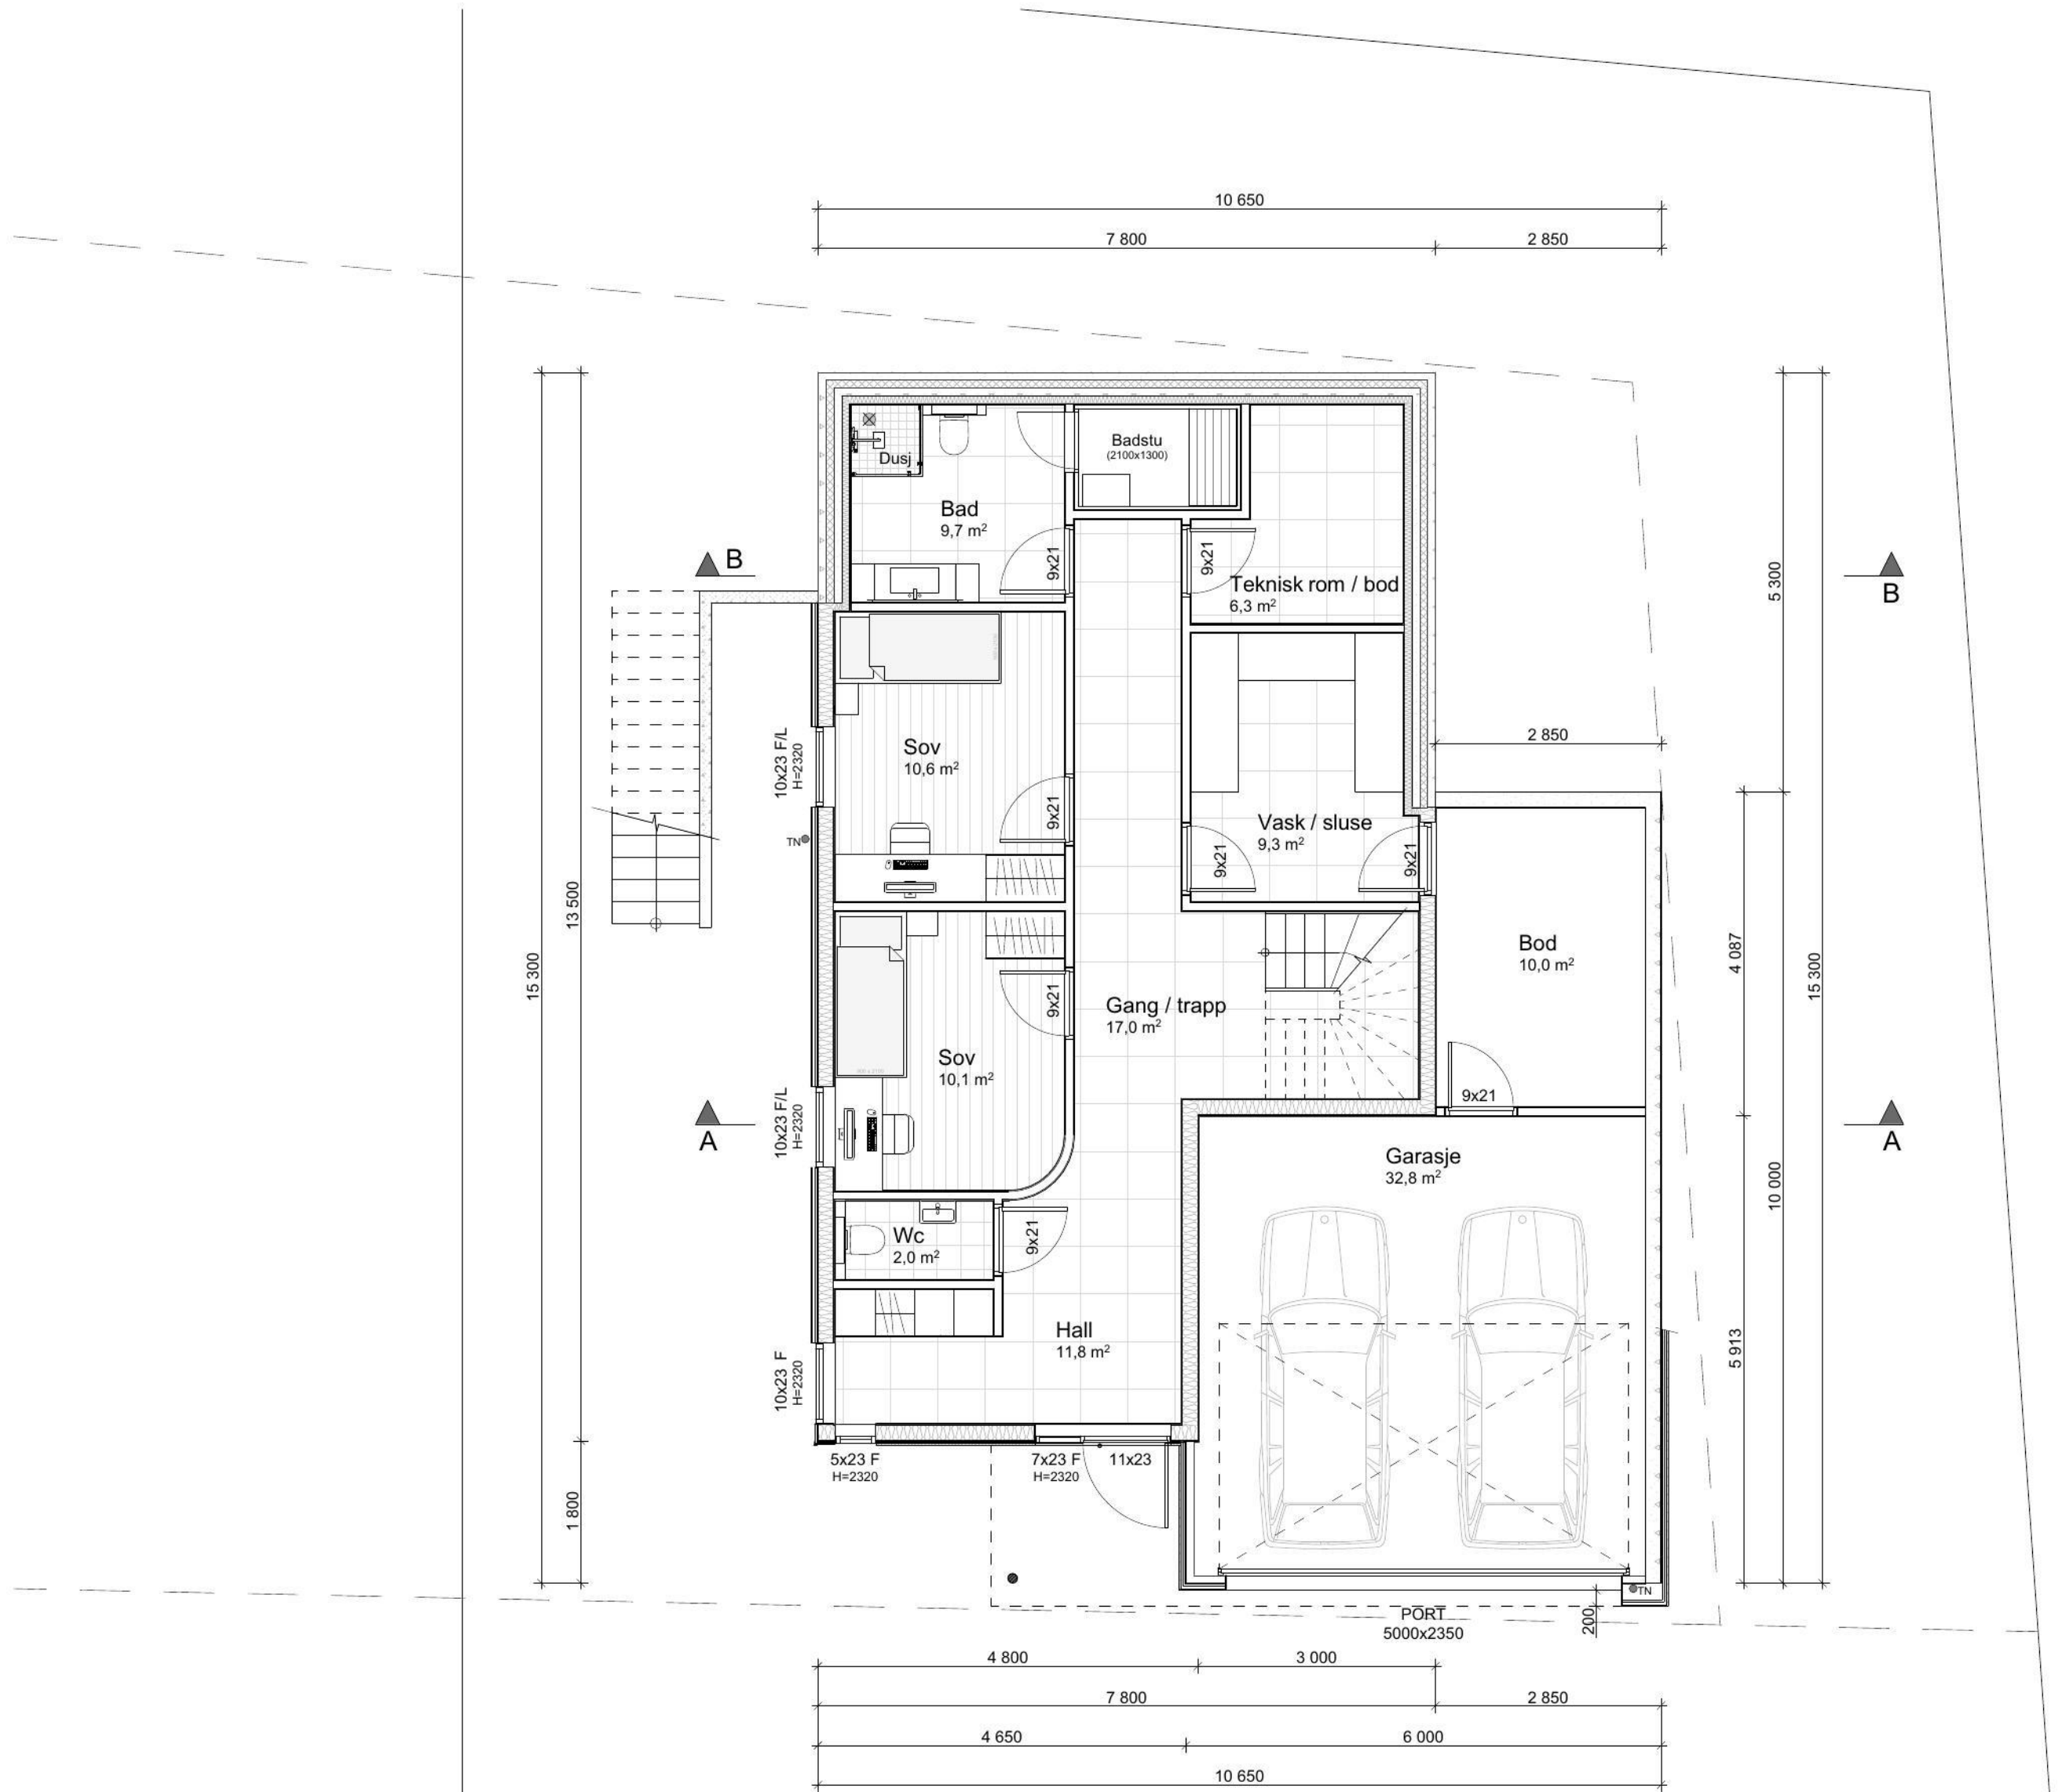

Plan 1.etasje
BRA bolig A (inkl. garasje)
126,6 m²

Areal (BYA)		Areal (BRA)	
Bolig	95,9 m²	1. etasje	82,3 m²
Garasje	47,6 m²	2. etasje	94,6 m²
		Garasje inkl. bod	44,3 m²
SUM (BYA)	143,5 m²	SUM (BRA)	221,2 m²

BYA % (BYA _{max} = 30%)	26,1 %
Tomteareal	550,7 m²
Tomteareal inkl. veiareal	568,1 m²

D	Diverse revideringer	11.01.24	JGRN
C	Diverse revideringer	05.01.24	JGRN
B	Tegninger klar for BYGGEMELDING	11.12.23	JGRN