


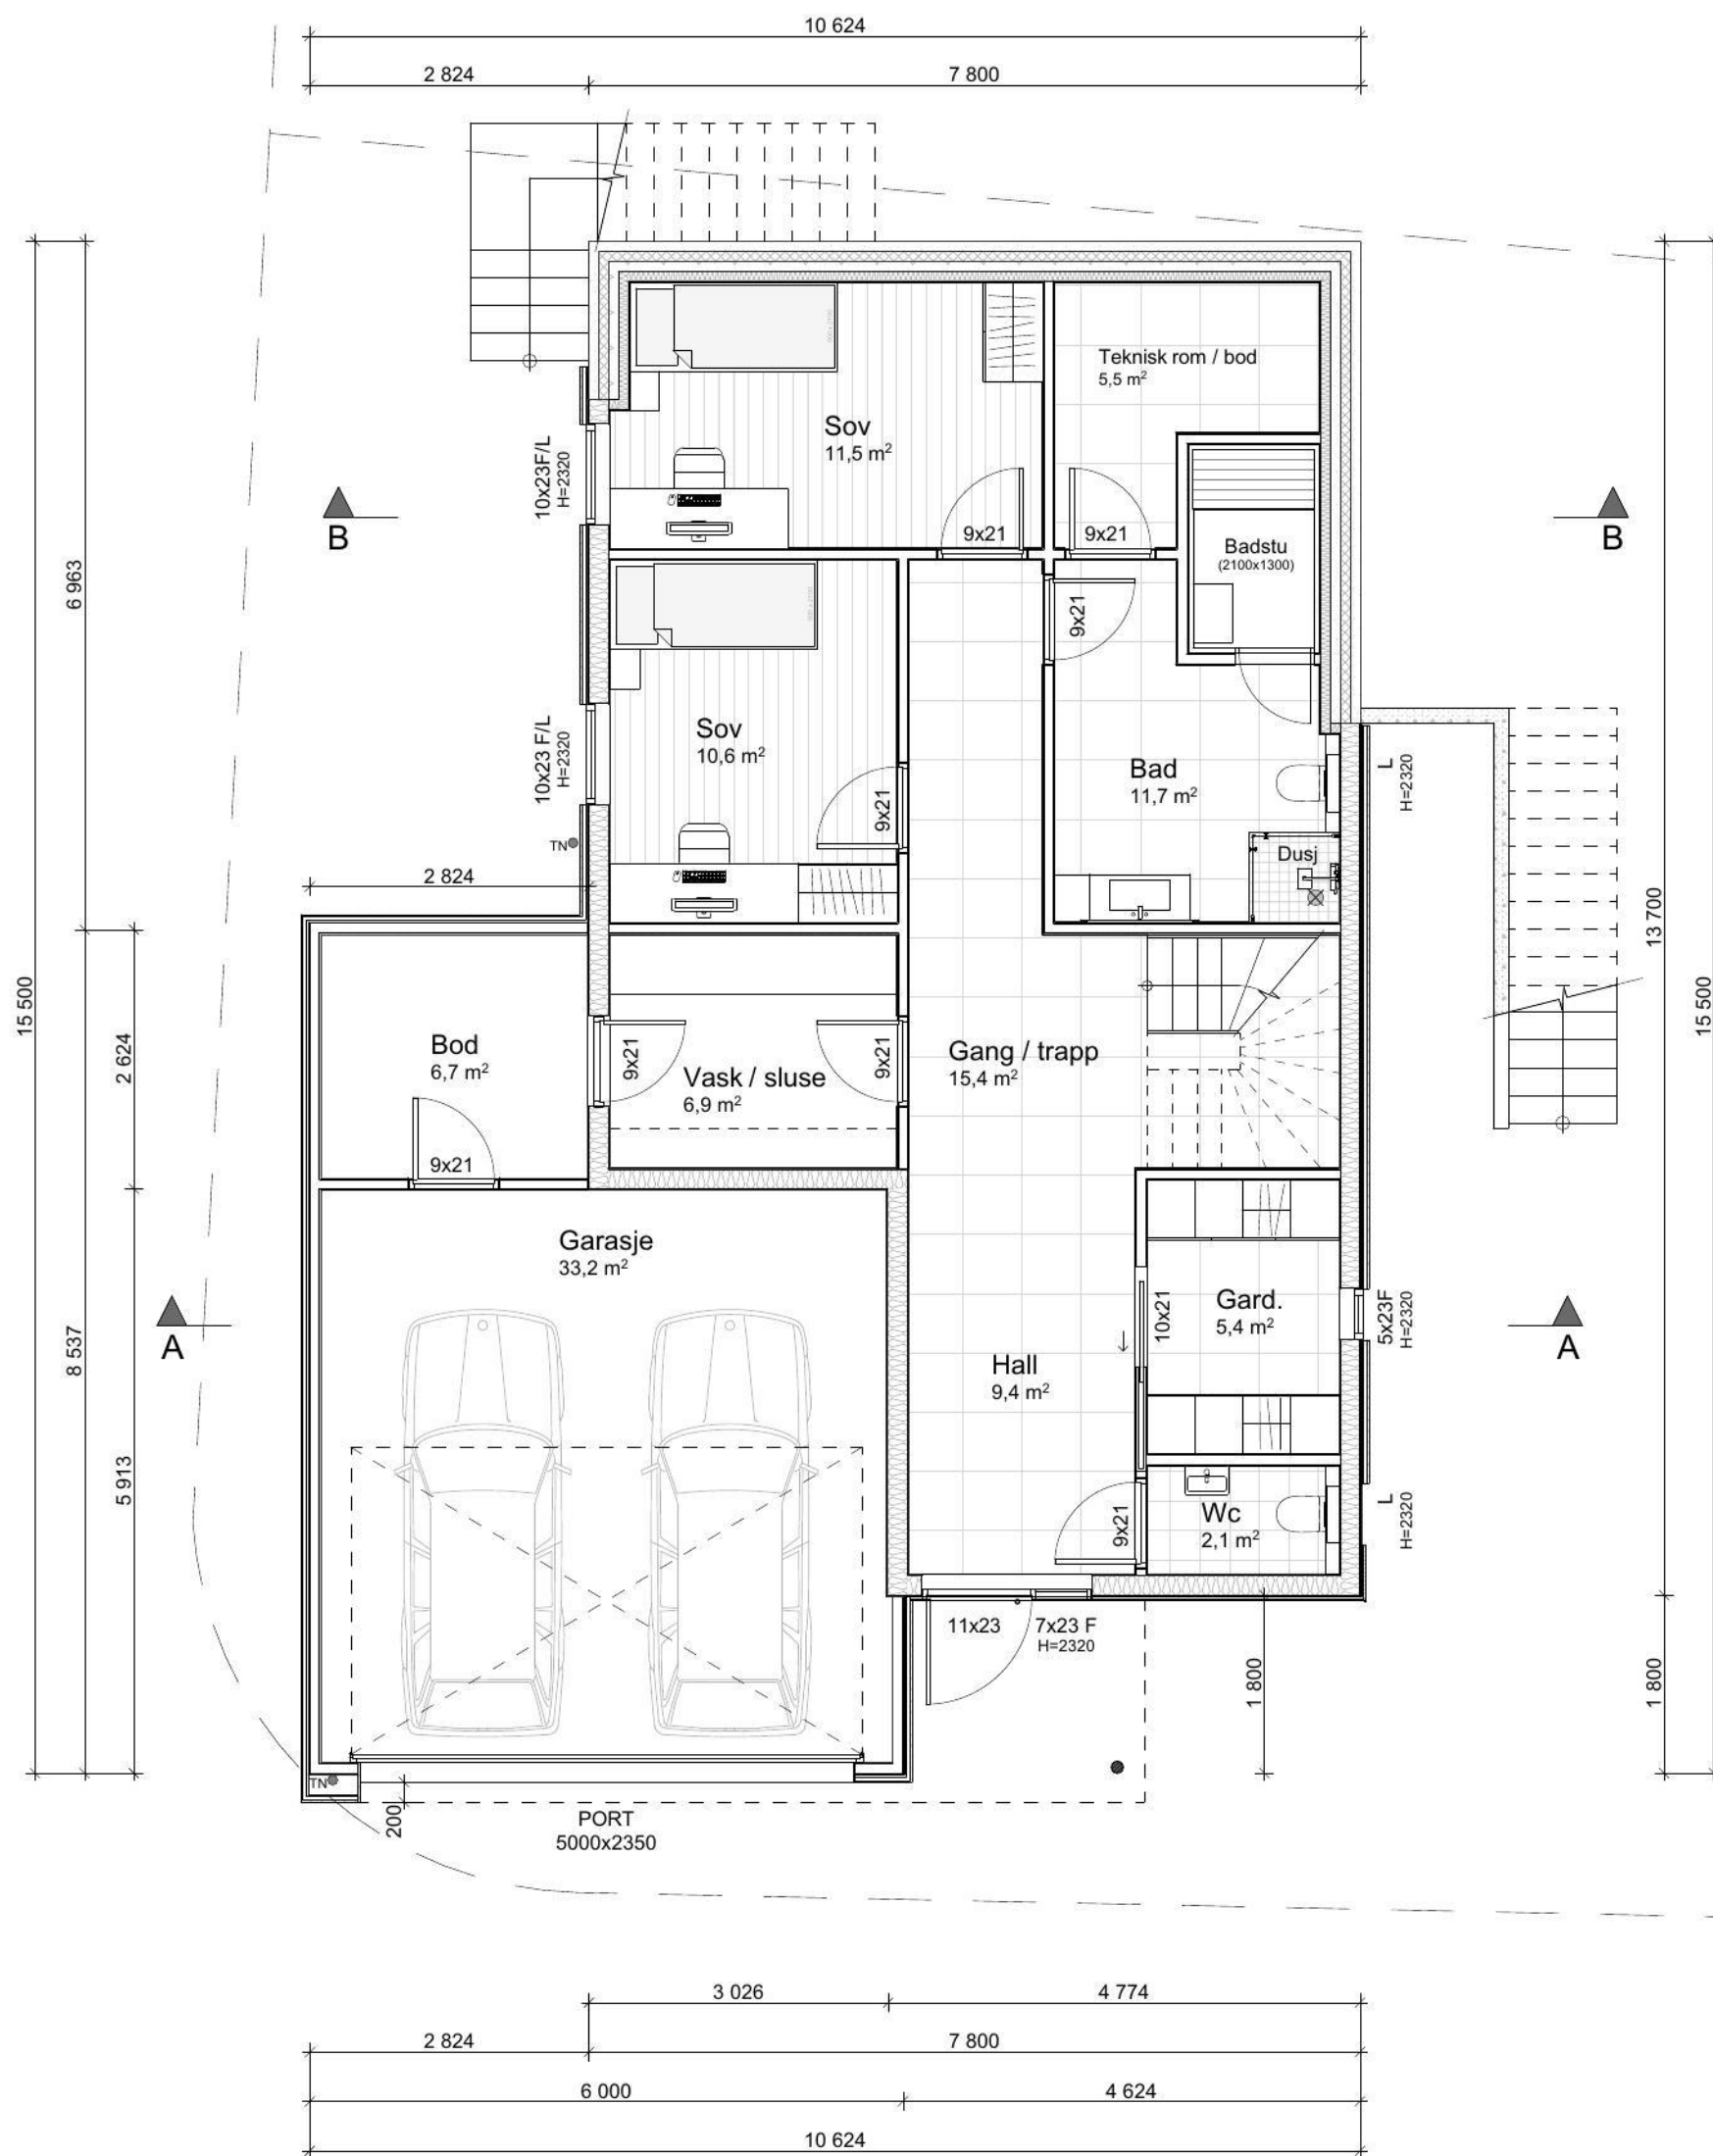

Plan 1.etasje
BRA bolig B (inkl. garasje)
125,2 m²

Areal (BYA)		Areal (BRA)	
Bolig	97,4 m²	1. etasje	83,9 m²
Garasje	43,4 m²	2-etasje	96,1 m²
		Garasje	41,3 m²
SUM (BYA)	140,8 m²	SUM (BRA)	221,3 m²

BYA % (BYA _{max} = 30%)	24,8 %
Tomteareal	567,3 m²
Tomteareal inkl. veiareal	650,3 m²

D	Diverse revideringer	11.01.24	JGRN
C	Diverse revideringer	05.01.24	JGRN
B	Tegninger klar for BYGGEMELDING	11.12.23	JGRN