
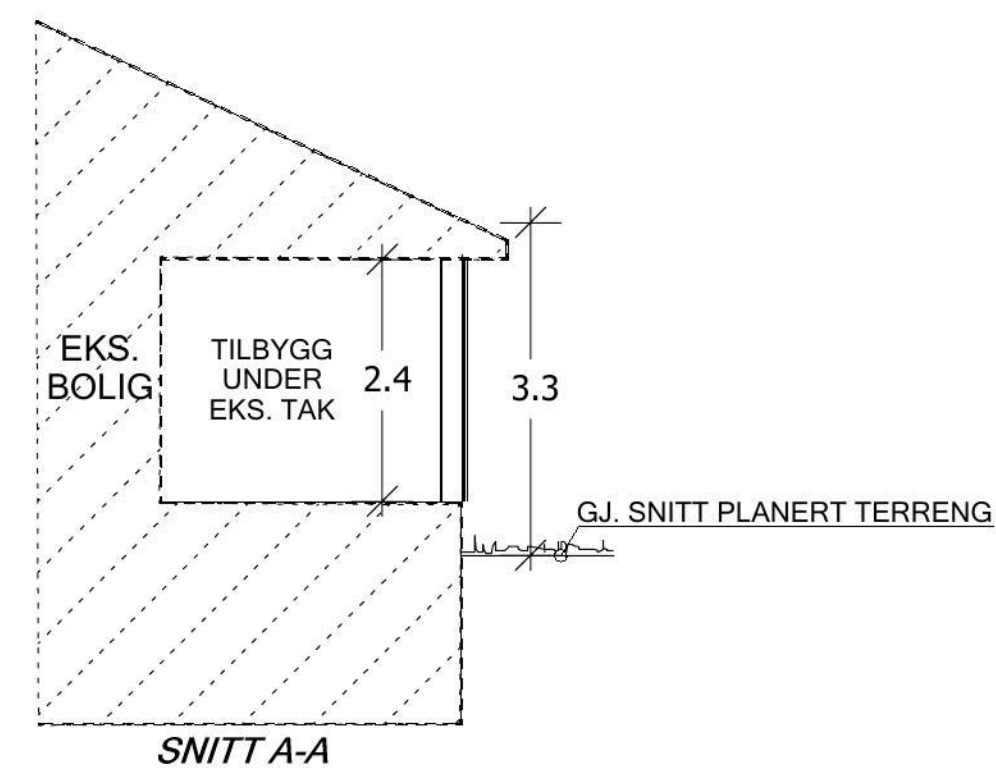


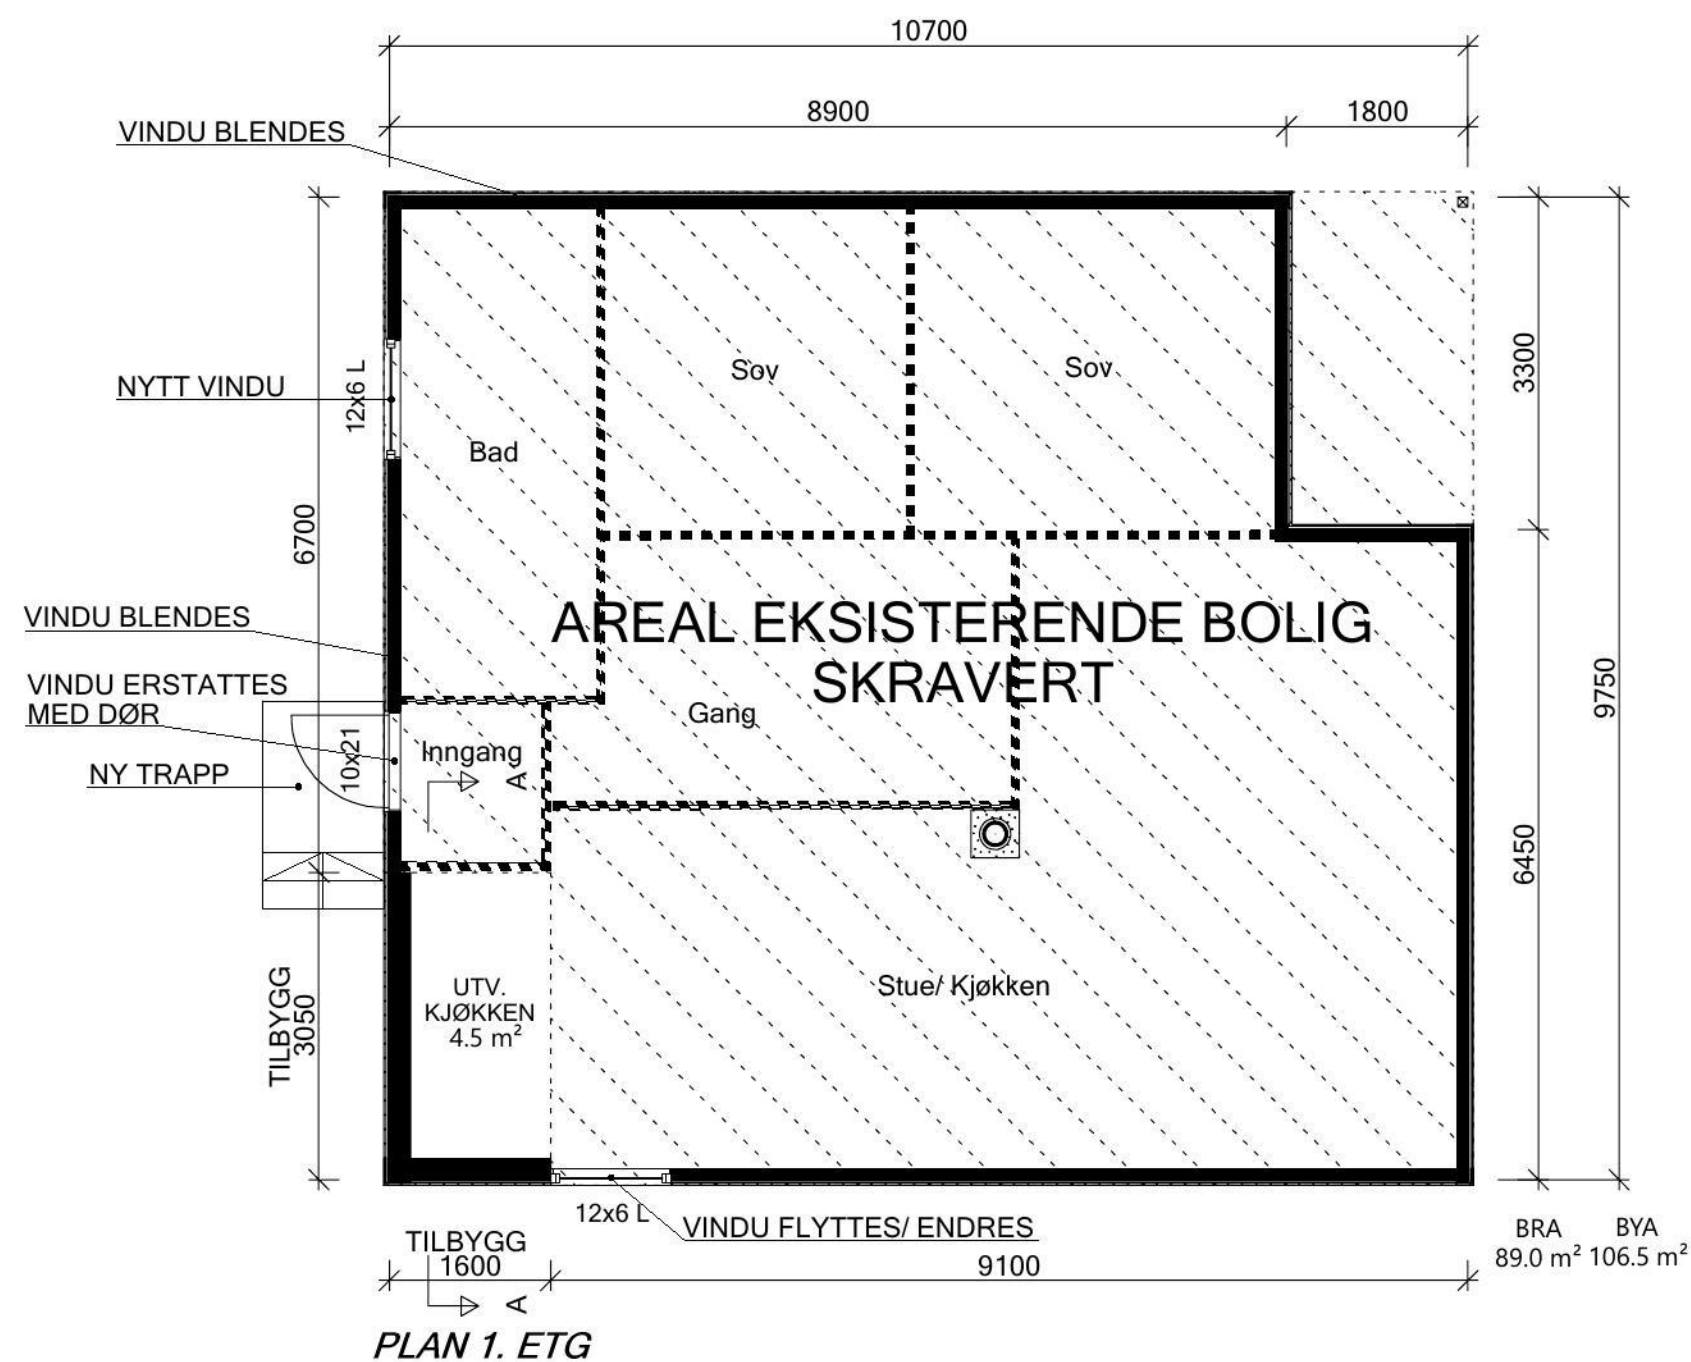

AREAL EKSISTERENDE:		
Arealberegninger i hht. NS 3940	Bruksareal BRA kvm	
	Pr etasje	Sum BRA
Kjeller	83.5	83.5
1. etasje	89.0	89.0
SUM :	172.5	172.5
BYA :	106.5	106.5

AREAL NYBYGG:		
Arealberegninger i hht. NS 3940	Bruksareal BRA kvm	
	Pr etasje	Sum BRA
1. etasje	4.5	4.5
SUM :	4.5	4.5

GRAPHISOFT

Bygg & Prosjekt Service as
Snekkerveien 22, 4321 Sandnes

TEGNER: Frank Hellenen
KONTR.:
MÅL: 1 : 100
DATO: 03.01.24

REV.	ANT.	REVIDERING GJELDER	SIGN.	DATO
				16.01.24
TILBYGG OG FASADENDRING Brit Eline Bendiksen Røspetteveien 5, 4083 Hundvåg Matrikkel: 5/ 381				
PLAN OG SNITT				
PROSJEKT NR.:		TEGN NR.		REV.
3679		500		