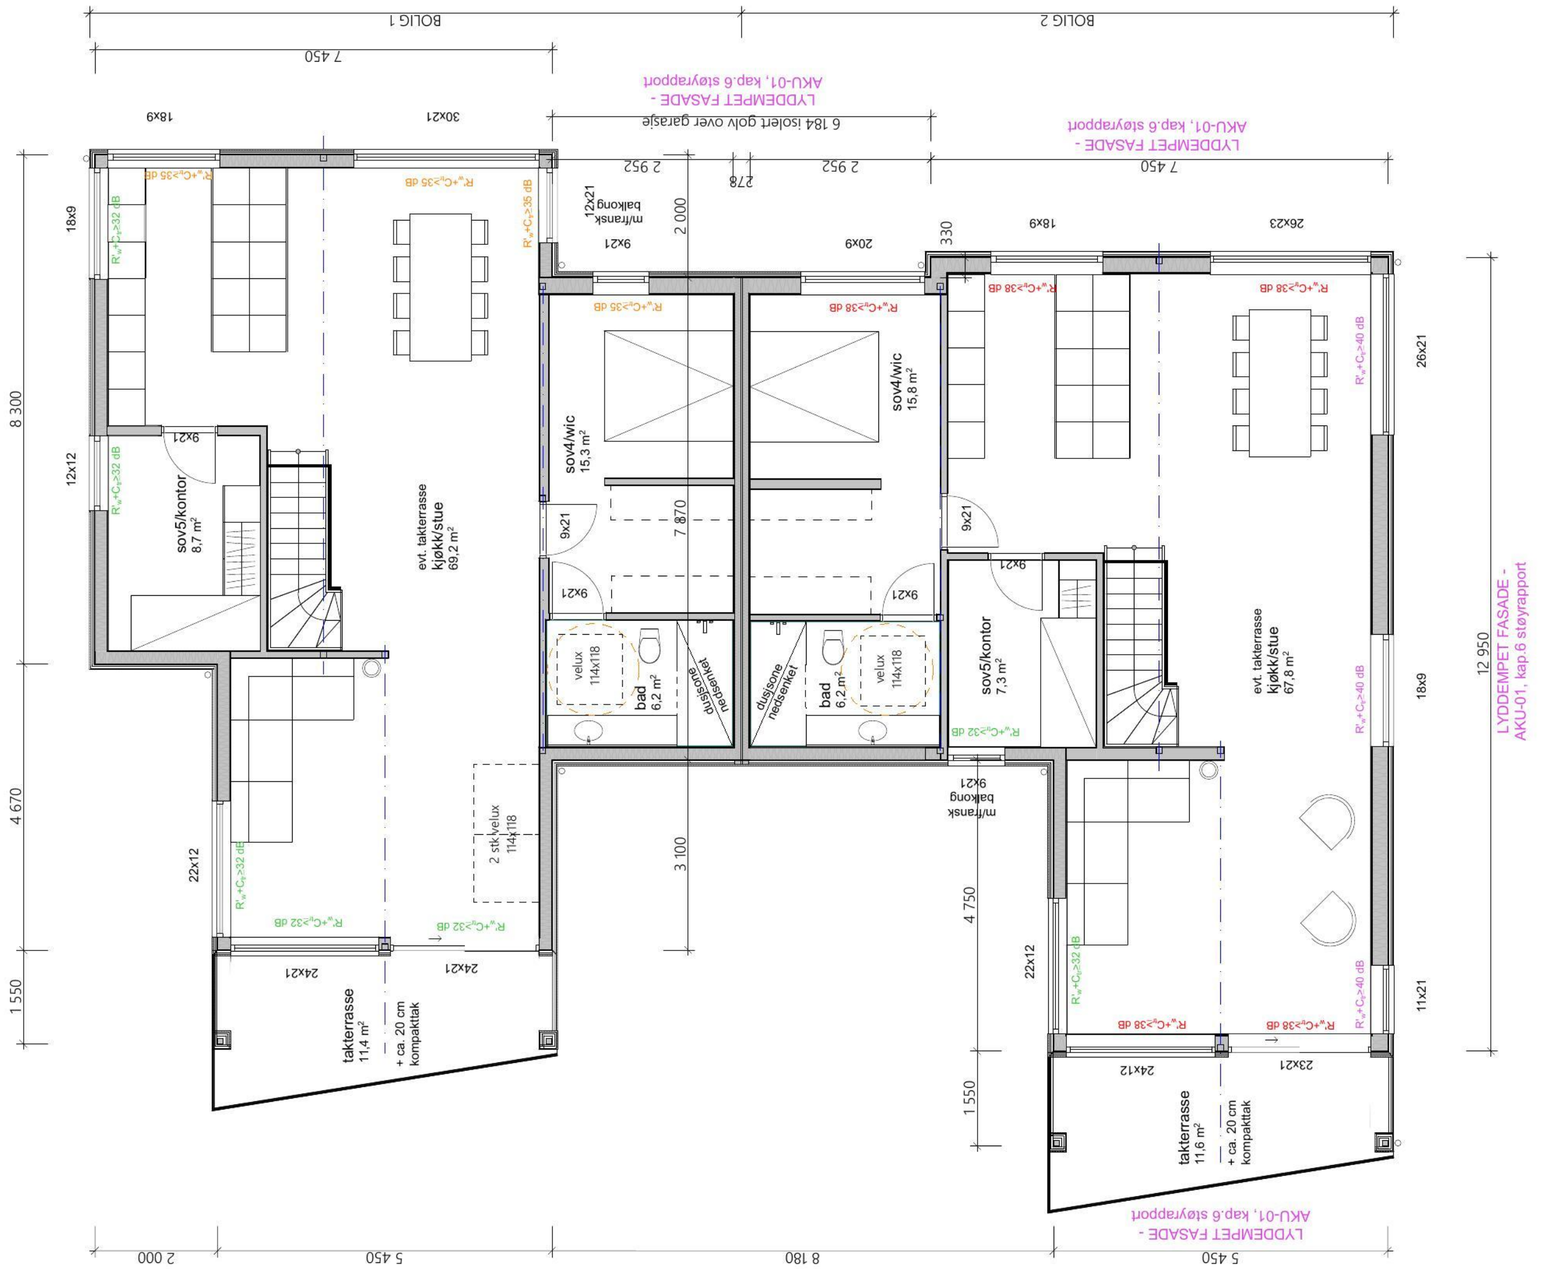



| Rev | Beskrivelse | Dato | Sign | Kontr |
|---|---|---|---|---|
| C | påført lydkrav på vinduer, oppdatert sol skygge | 19.01.2024 | als | tf//rh |
| B | justert gesimshøyde, senket nivå hager | 20.12.2023 | als | rh |
| A | BYGGEMELDING | 18.12.2023 | als | als |

| Areal (BYA) | | Areal BOLIG 1 (BRA) | | Areal BOLIG 2 (BRA) | |
|---|---|---|---|---|---|
| bolig inkl. garasje/bod | 246,4 m² | 1.etasje | 86,5 m² | 1.etasje | 85,4 m² |
| parkering | 18,0 m² | 2. etasje | 102,1 m² | 2. etasje | 100,2 m² |
| **SUM BYA** | **264,4 m²** | **SUM** | **188,6 m²** | **SUM** | **185,6 m²** |
| **% BYA (maks 35 %)** | **34,9 %** | | | | |
| | | garasje inkl. bod | 22,2 m² | garasje inkl. bod | 22,2 m² |
| | | | | | |
| netto tomt (brutto = 814,7 m²) | 756,8 m² | | | | |

BYGGEMELDING

FJOGSTAD Etablert 1903 /HUS

Byggherre: **Fjogstad & Forny AS**

Byggplass: **ULLANDHAUGVEIEN 91**
Stavanger kommune

| Ark.: | G.nr.: | B.nr.: |
|---|---|---|
| als | 24 | 358 |

| Tegner: | Prosjekt nr.: |
|---|---|
| als | 17915 |

| Målestokk: | Tegning: |
|---|---|
| 1:100 | **2 etasje** |

| Dato: | Tegningsnummer: | Rev. |
|---|---|---|
| 24.11.2023 | **024** | **C** |

*Forbudt å kopiere, distribuere eller på noen bruke tegningen uten samtykke fra Fjogstad-Hus as.*