


1:100 Fasade øst

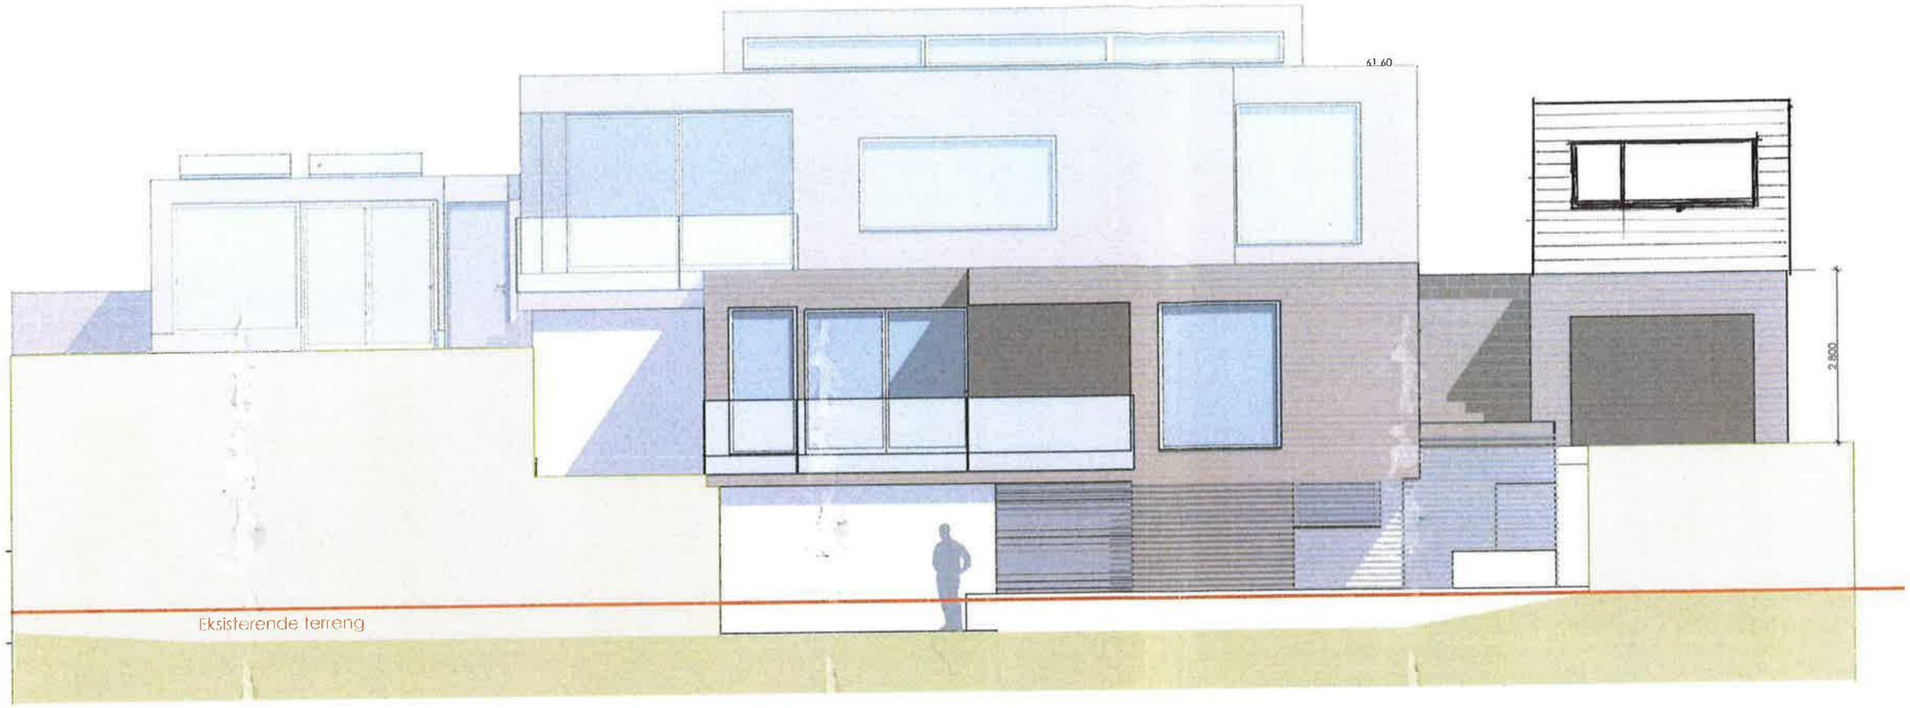

1:100 Fasade Sør

TEGNINGSNUMMER
A40-102

REVISJONSNUMMER

TYPE TEGNING

Prisforespørsel: 09.12.2013

Index	Dato	Beskrivelse	Sign

LOKALISERINGSFIGUR

N

Prosjekteringsgruppen:

ARK: ak2 sivilarkitekt mnal AS — Nylorget 1, 4012 Stavanger, mob. 40672885

RIB: Rådg. ing. Bygg — veien 0, 0000 Stedet, Tlf. 00 00 00 00, Fax. 00 00 00 00

RIE: Rådg. ing. Elektro — veien 0, 0000 Stedet, Tlf. 00 00 00 00, Fax. 00 00 00 00

RIV: Rådg. ing. Vent. — veien 0, 0000 Stedet, Tlf. 00 00 00 00, Fax. 00 00 00 00

Fase: Forprosjekt

Prosjektnummer: **ak2 - 024**

Tittel:

Soltunveien 21
gnr 28 bnr 152
Stavanger

Birte Noer Borrevik

Godkjent

Kontroll prosjekt.
Sign. | Kontroll

Filnavn: ak2-024.12 v17.pln

Dato: 13.09.2013

Målestokk: **1:100**

Kontroll utførende
Sign. | Kontroll

Tegningsnummer: A40-102

Prosjektnr. for prosjekterende/ lev.

TYPE TEGNING:

Fasade Sør og Øst