


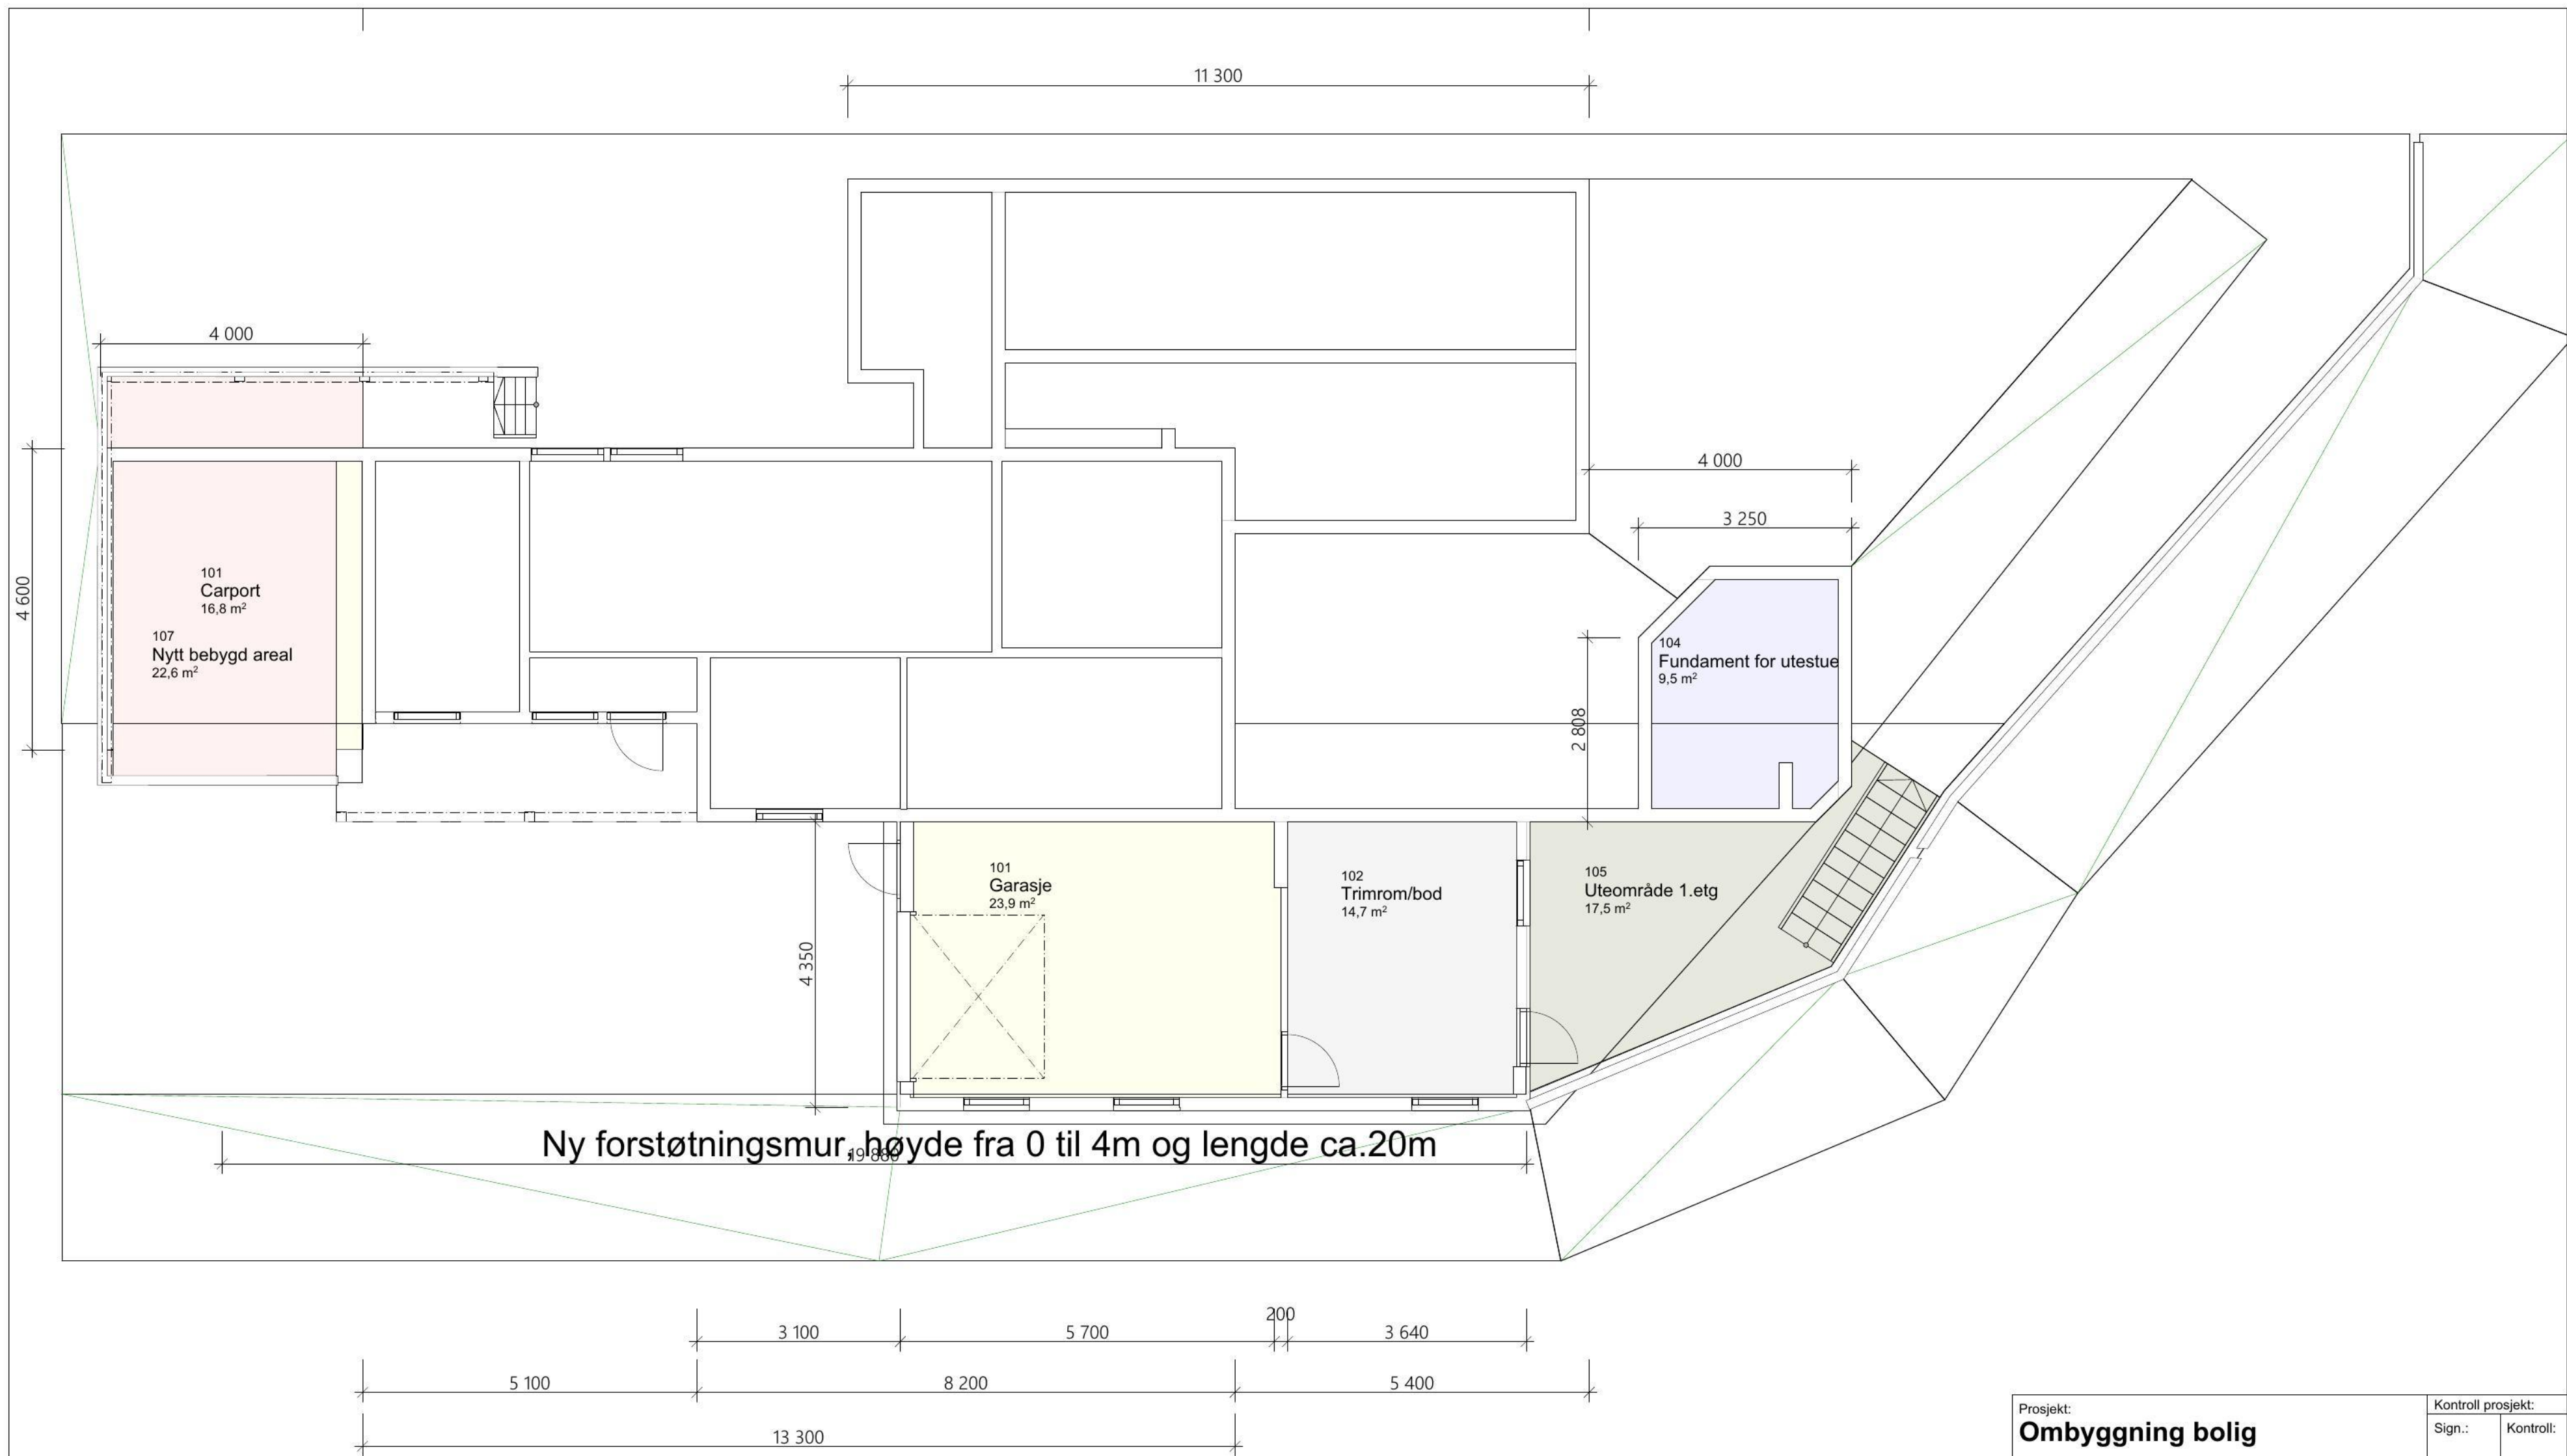

Prosjekt: Ombygging bolig	Kontroll prosjekt:	
	Sign.:	Kontroll:
Tiltakshaver: Håkon Jar Gimlekollen 3 4600 Kristiansand	Gnr./Bnr./Festenr.: Gnr107/Bnr05	
Prosjekterende: Skjærgårdsbygg a/s Østerøya 240 4625 Flekkerøy		
© Alle rettigheter tilhører utførende for prosjektering, kopiering eller bruk av disse tegningene er forbudt uten skriftlig samtykke	Dato: 07.08.2023	
Tegning: Plan 1. etasje	Målestokk: 1:100	
	Tegningsnr.: A20-1	Rev.: .