


Eksist. bolig er tegnet iht. gamle tegninger/mottatt mål.

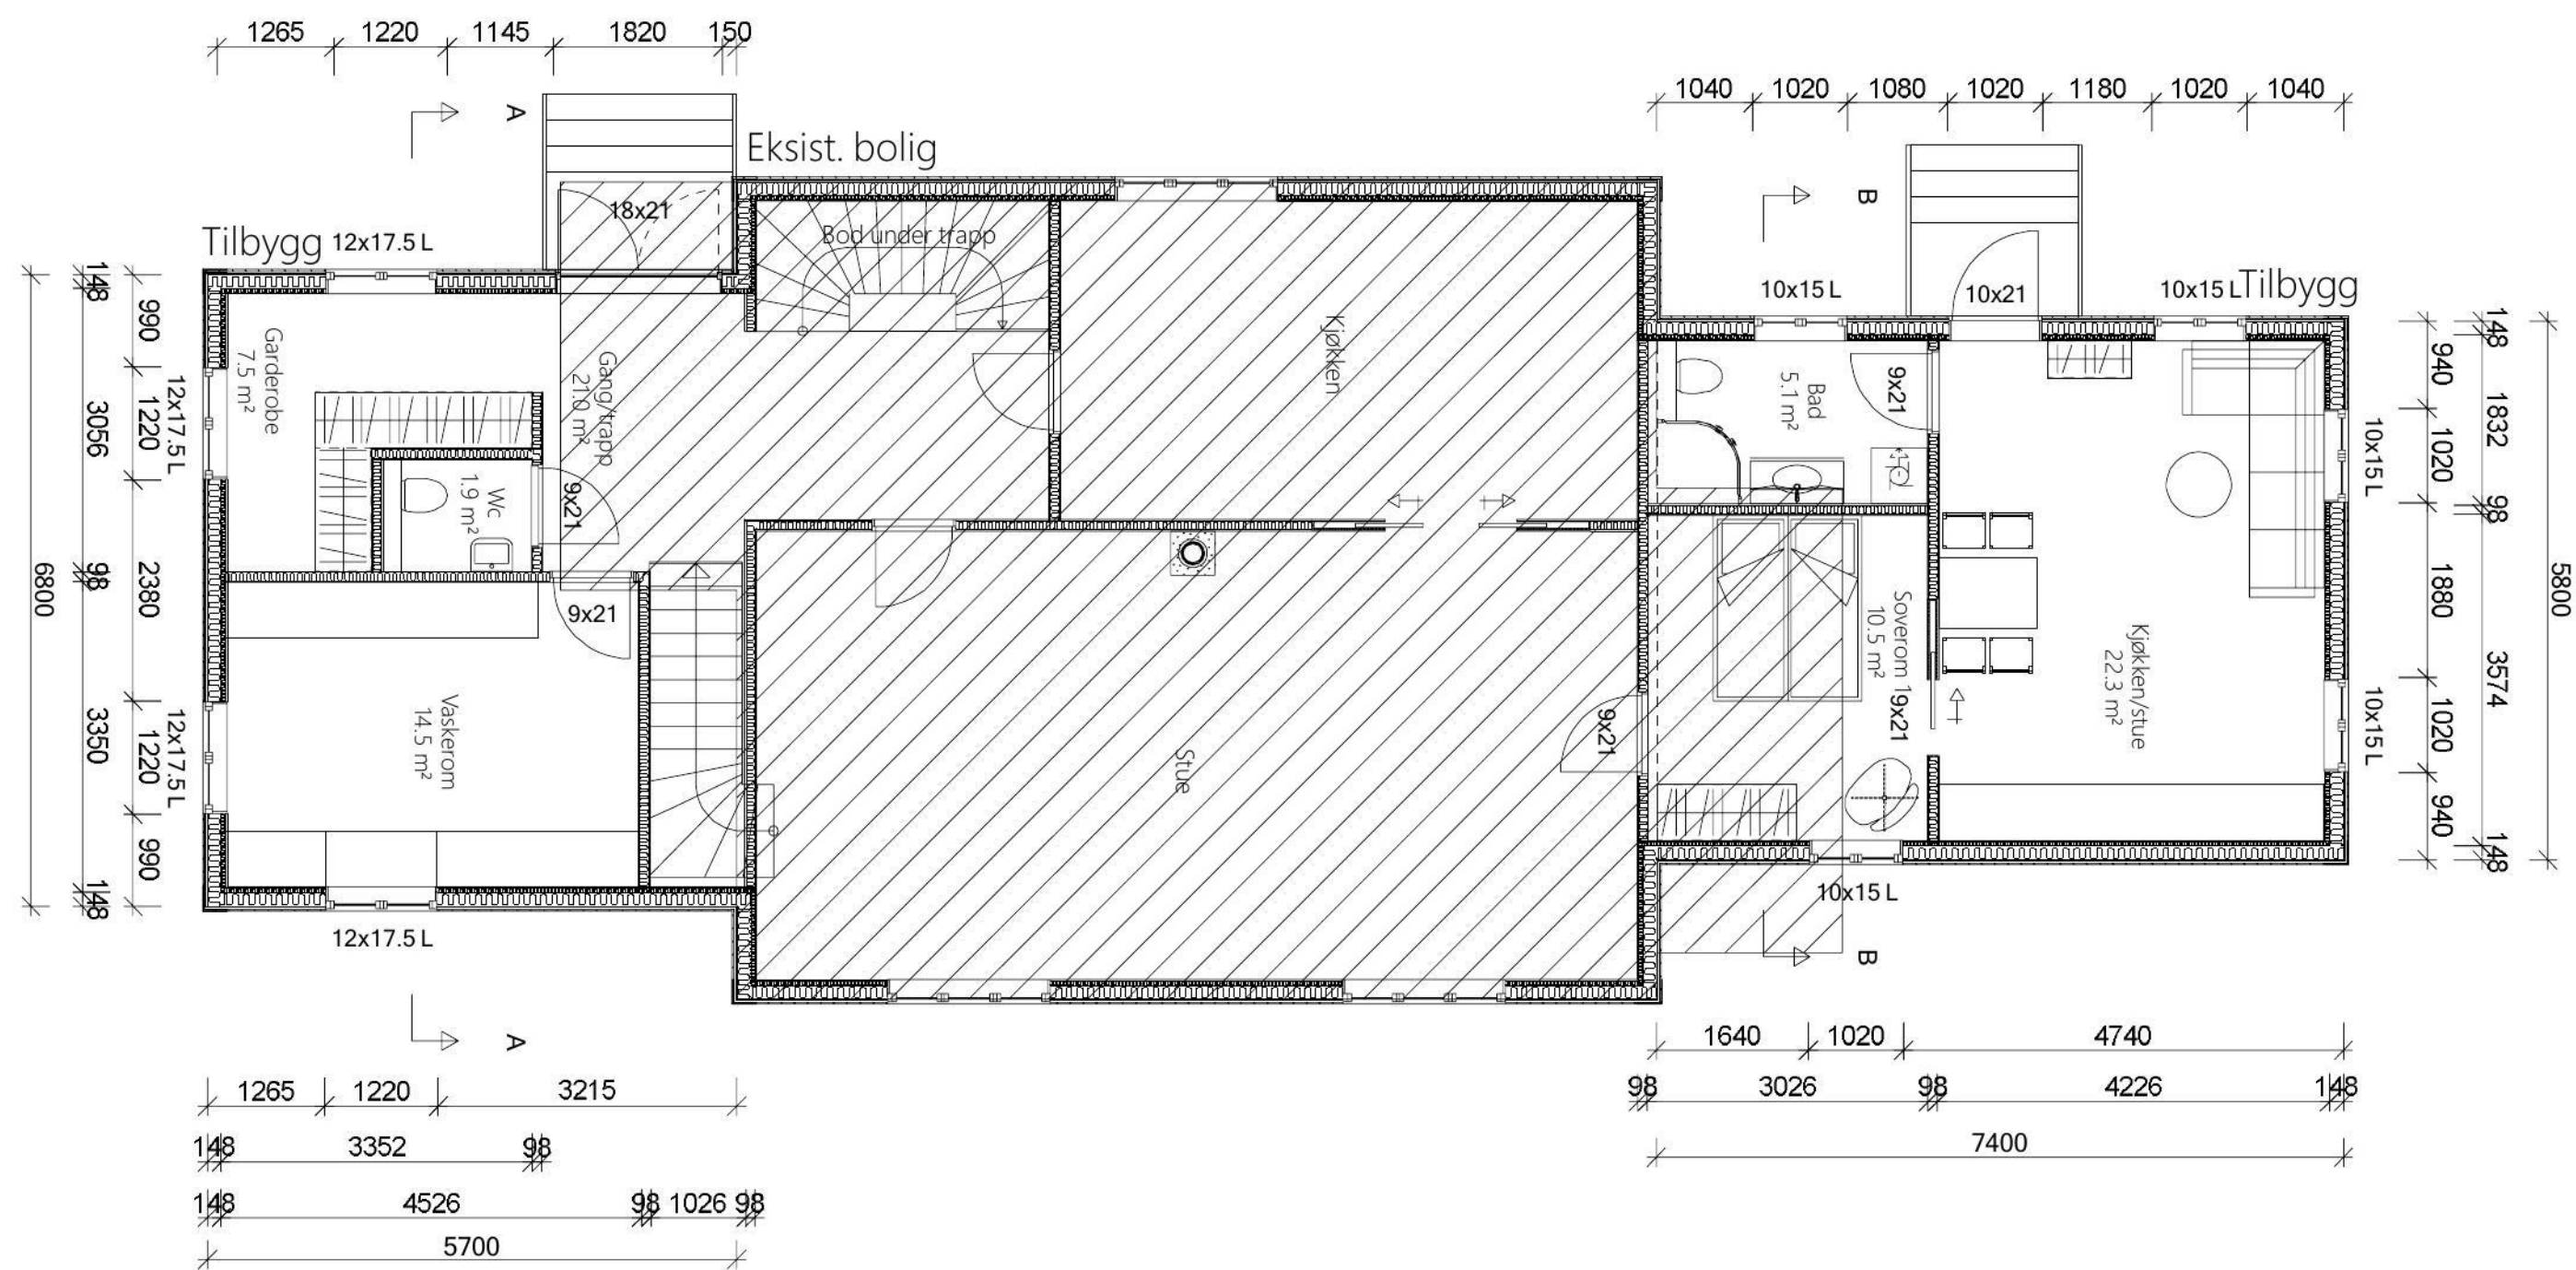

1. Etasje

Eksist. bolig + tilbygg:

Arealberegninger i hht. NS 3940	Bruksareal BRA kvm		
	Pr etasje	Utvendig bod/garasje	Sum BRA
SUM :	0.0	0.0	0.0
BYA :	172.3	7.1	179.4



 DATA DESIGN SYSTEM	A		Diverse	DMN	01.06.2023
	REV.	ANT.	REVIDERINGEN GJELDER	SIGN.	DATO
Andreas Haraldstad					
			G.NR. 20	B.NR. 56	
1. etasje					
Haslevollen 14			KOMMUNE: Kristiansand		
 Flatnes Bygg Consult			TEGN. DMN	PROSJ.NR. 6352	
			GODKJ.		
			MÅL 1 : 100	TEGN. NR. 501	
			DATO 08.05.2023		
TEGNINGEN MÅ HVERKEN HELT ELLER DELVIS KOPIERES ELLER BENYTTES UTEFØRELSE AV ARBEID SOM FLATNES BYGG CONSULT AS IKKE MEDVIRKER I					