


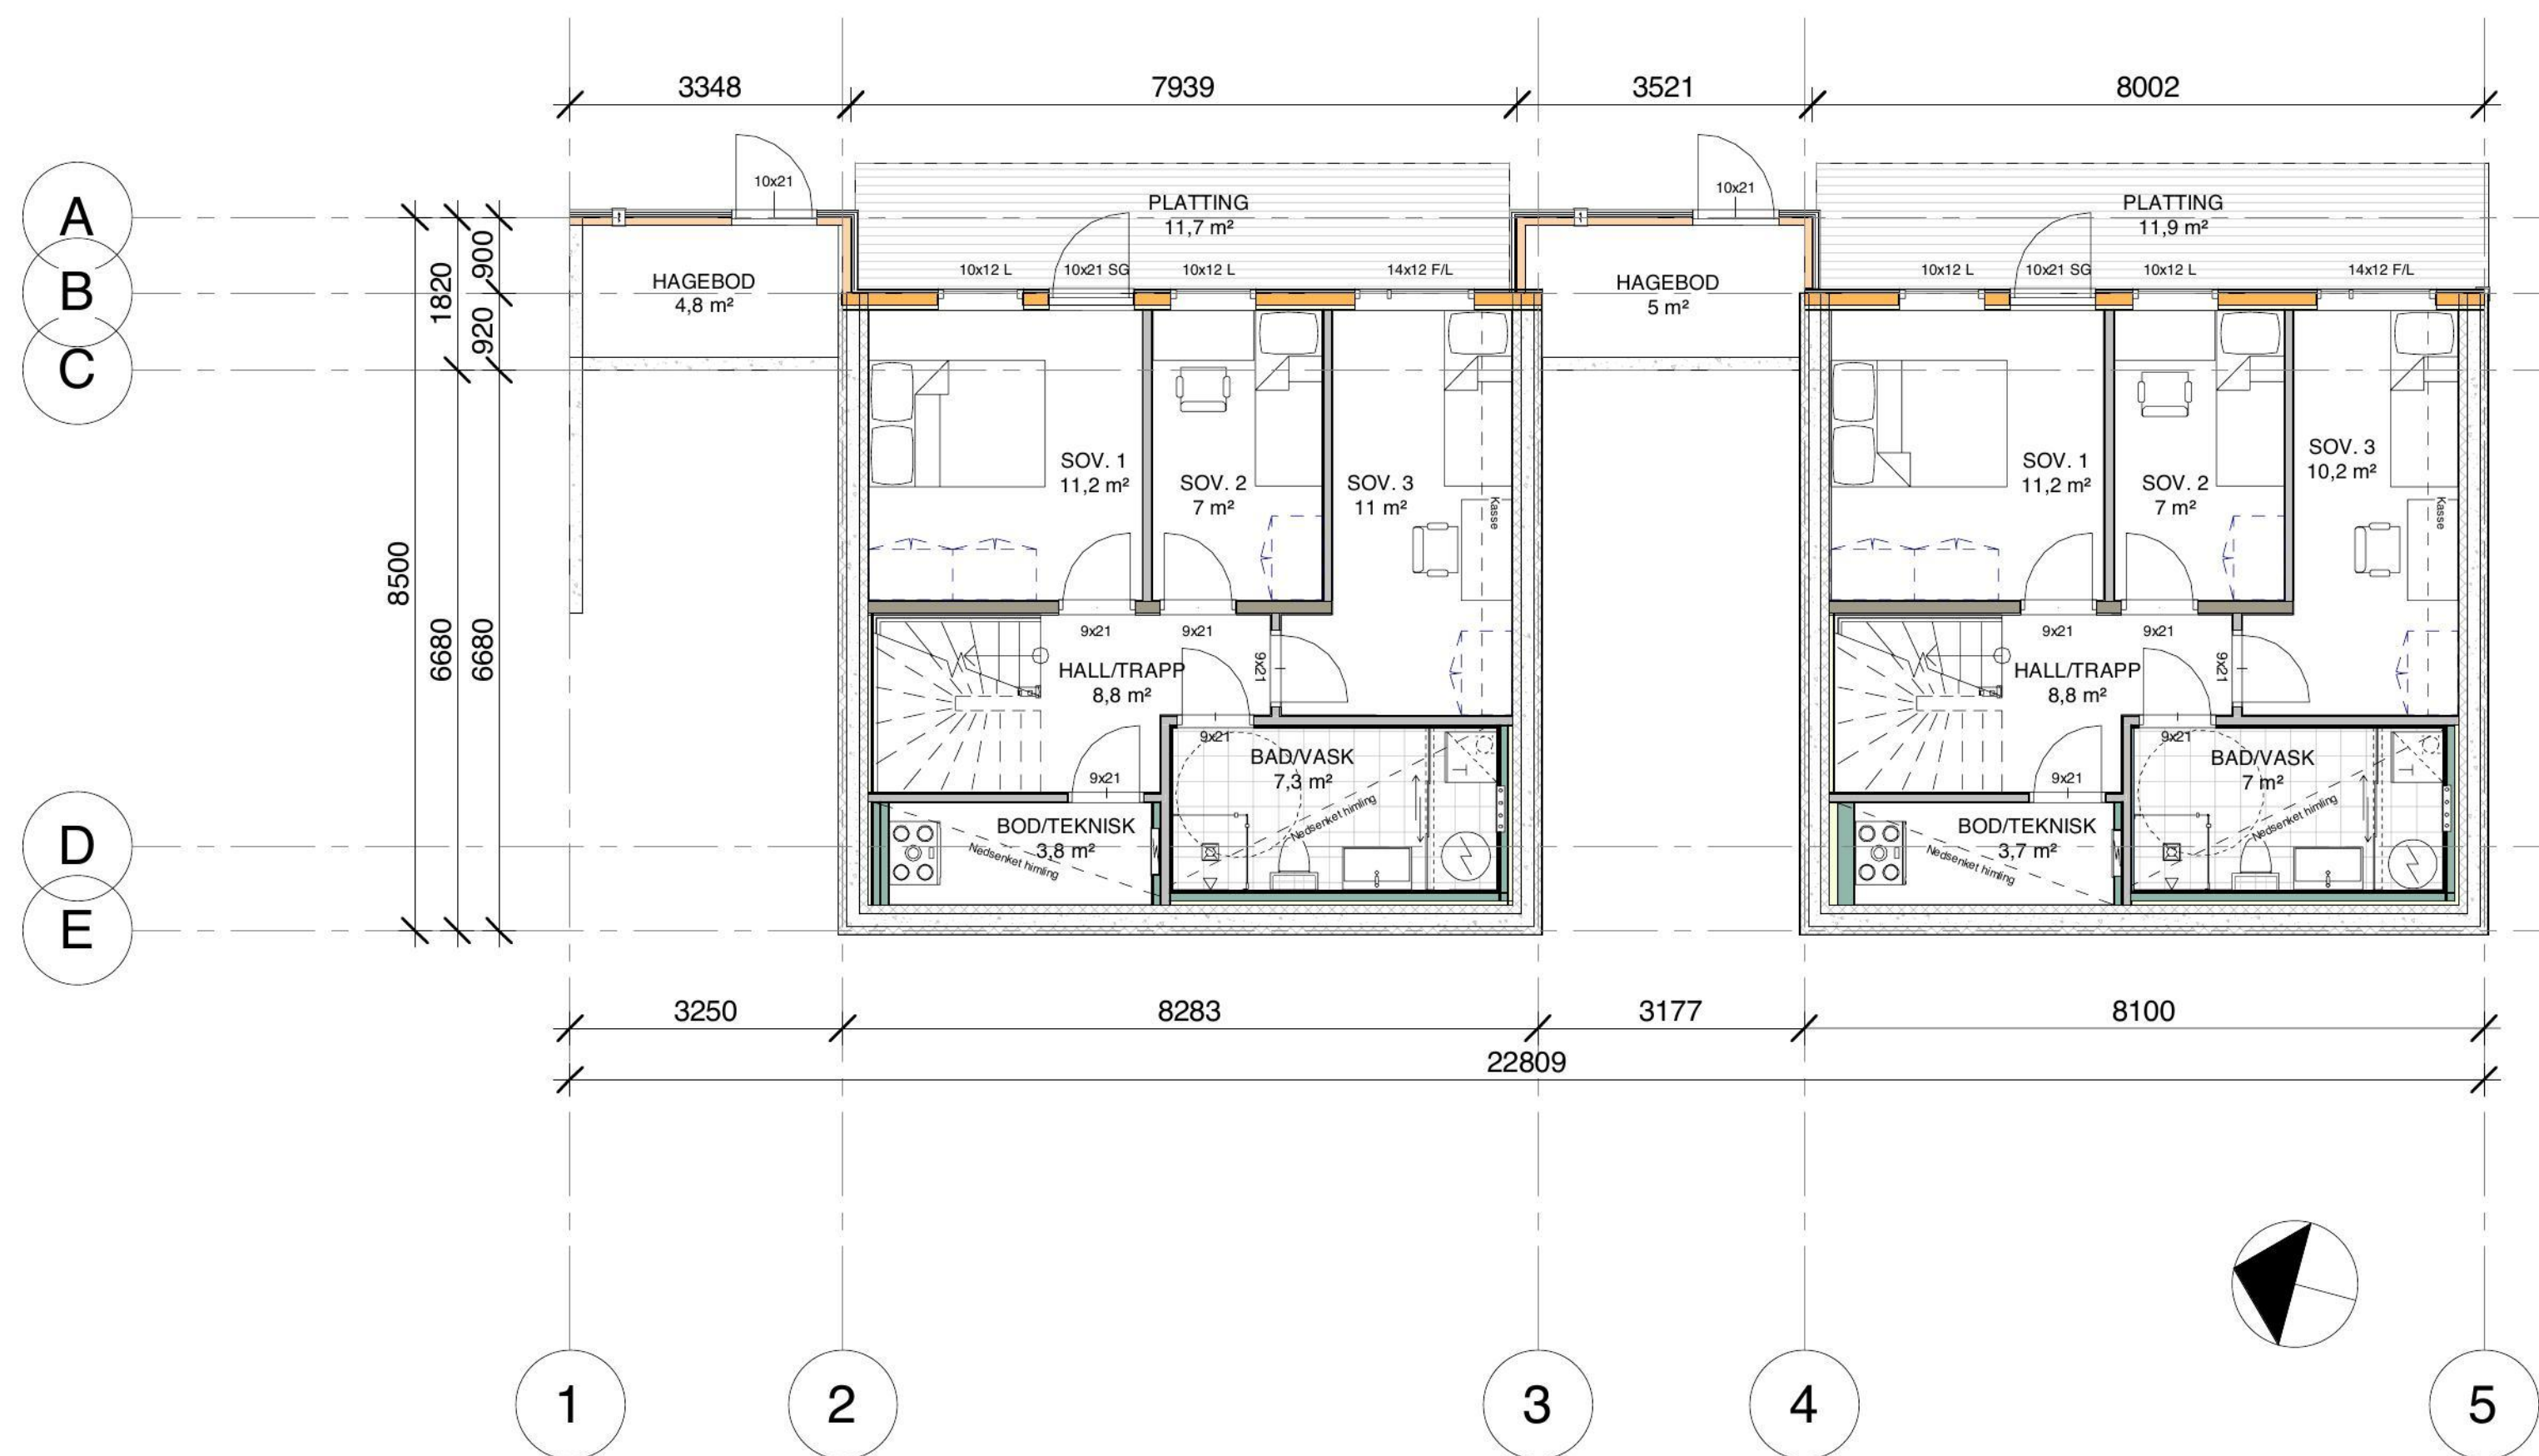

0. Etasje
1 : 100

Lokaliseringsfigur:



Rev.	Revisjonen gjelder	Dato	Utført	Kontr.
Tegningsnavn	Plan U.Etasje	Dato	Tegnet	Kontr.
Tiltakshaver:	OBOS Block Watne AS	27.07.23	M.E.	T.A.
Byggeplass:	Benestadheia 149-151			
Prosjektnavn:	DRANGSVANN BKS16 - HUS 106-107			
G.NR./B.NR.	67/230-231	Målestokk	As indicated	Arkstørrelse
KOMMUNE:	KRISTIANSAND	TEGNINGSTYPE:	U1 A PL 20 1	
HUSTYPE:	-	BOLIGTYPE:	Kjedet enebolig	
Tegningsnr.	137990805	ETASJE	FAG	TYPE
PROSJEKTNUMMER	U1 A PL 20 1 F 0	DISIPLIN	LOPENR	FASE
		REVISJON		