


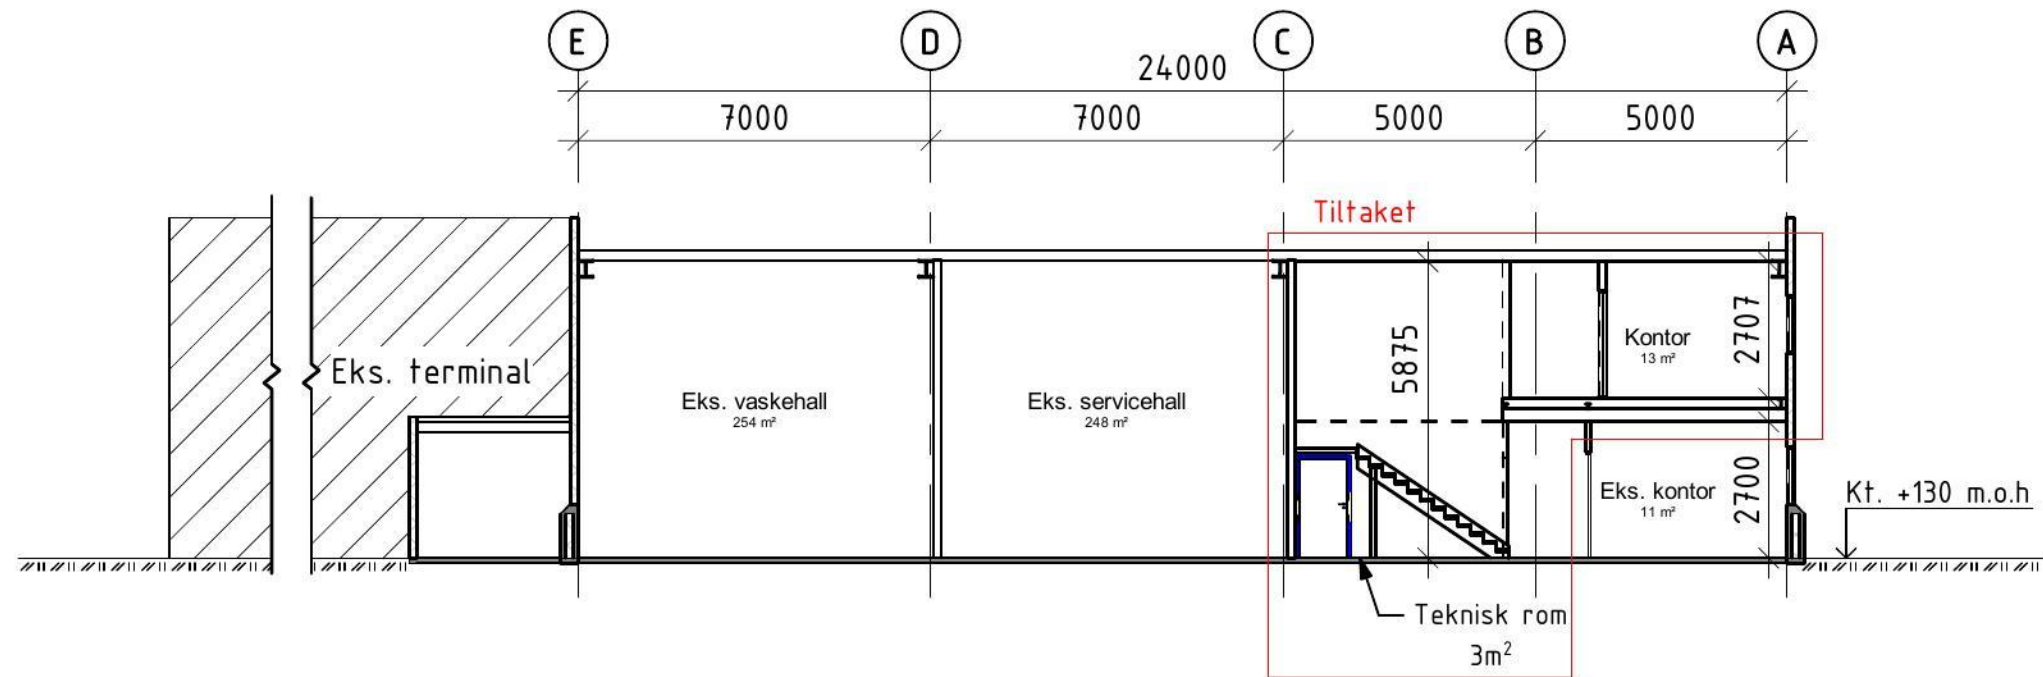

Prosjekt Veøy AS Omb. ny 2 etg kontorer Veøy Mjåvann	Tegningsstatus Søknadstegning	G.nr / B.nr 575/458	Målestokk 1:200
	Tegningsnummer A 40 101	Dato 06.06.2023	Prosjektnummer 23101
Tegningstittel Hovedsnitt Mjåvannsvegen 156, 575/458	 RÅDGIVENDE INGENIØRER	Tegnet av AH	Kontrollert av KA
		Revisjonsnummer	Fagdisiplin ARK