




Andøytoppen 84/86

Dato: 16.05.2023

Målestokk: 1:500

Koordinatsystem: UTM 32N

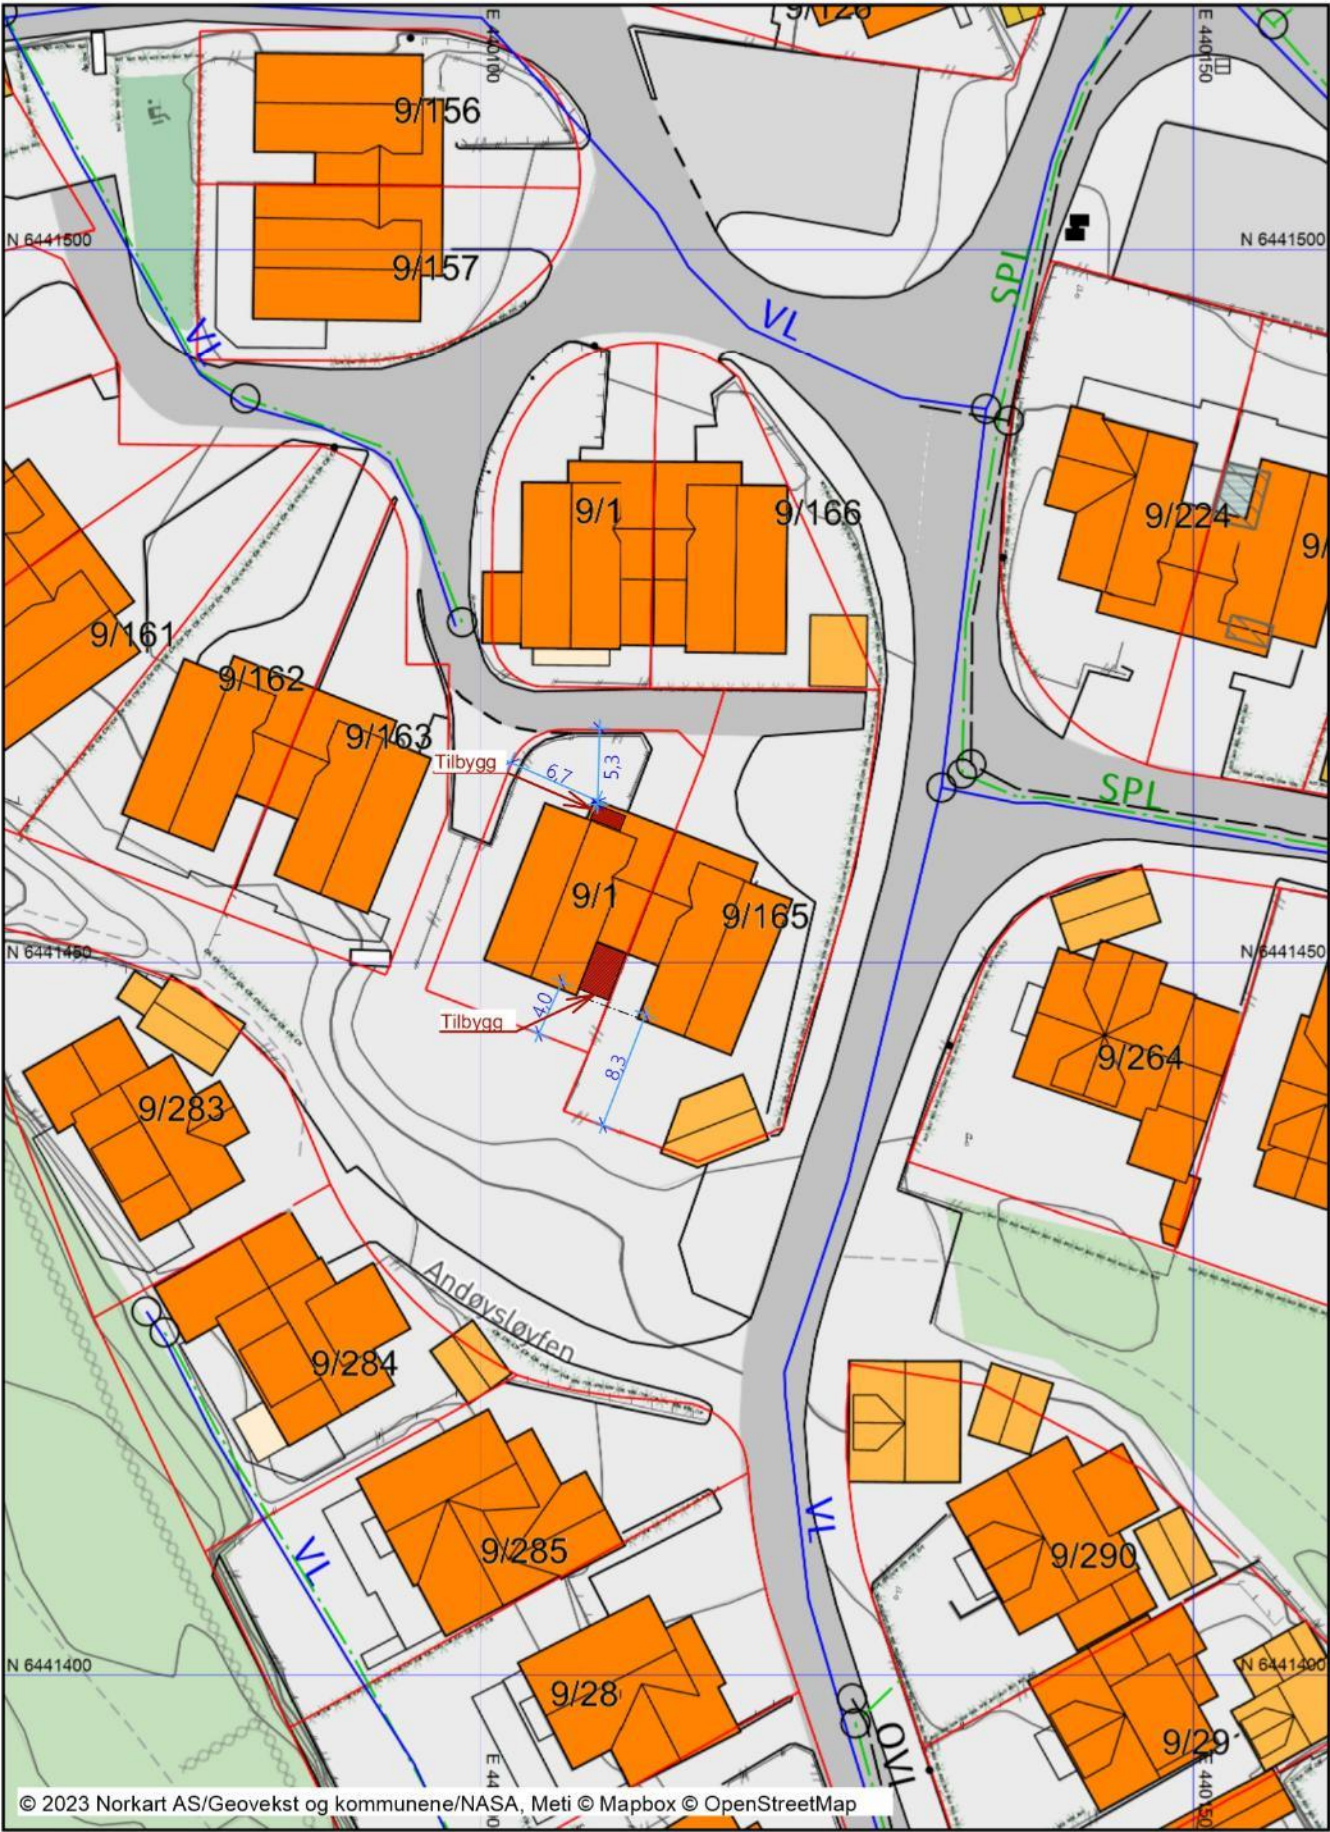

© 2023 Norkart AS/Geovekst og kommunene/NASA, Meti © Mapbox © OpenStreetMap

Høyde		Høyder	I meter
Gesimshøyde			4 280
Månehøyde			6 200
Terreng gj.sn.			-250
BYA og BRA er utregnet iht norsk standard 3940 NB Arealene kan ikke brukes i salgøyemed			
BYA Oppsummering			
Kategori		Areal (m²)	
BYA1 - Eksisterende bygg	Y1.1	BYA generelt	92,15
			92,15 m²
BYA2 - Tilbygg	Y1.1	BYA generelt	13,61
			13,61 m²
			105,75 m²
BRA Oppsummering bygg enkel			
Kategori		Areal (m²)	
BRA 1 - Eksisterende bygg	R1.1	BRA Generelt	201,95
			201,95 m²
BRA 4 - Nybygg	R1.1	BRA Generelt	11,52
			11,52 m²
			213,47 m²
BTA bygg enkel			
Kategori		Areal (m²)	
BTA 7 - Nybygg	R10	BTA Generelt	7,50
			7,50 m²
BTA 8 - Eksisterende bygg	R10	BTA Generelt	7,50
			7,50 m²
			15,00 m²
Situasjonskartet er hentet fra kommunens kart base, men kan inneholde feil.			

Rev.:	Dato:	Revisjonen gjelder:	Sign:
Prosjekt: Bolig for			
Klient: Tommys Bygg AS Storevollhei 54 C 4700 Vennesla Tiltakshaver: Andre Vigebø Haugen Andøytoppen 84 4623 Kristiansand Byggeadresse: Andøytoppen 84 4623 Kristiansand Byggested: Gnr. 9 Bnr. 164 Snr. - Fnr. - i Kristiansand kommune.			 Hunsøya 4700 Vennesla Tlf: 33 15 69 00 Faks: 38 15 69 01 E-post: firmapost@norsk-byggservice.no Signatur: F.Strandberg Kontroll: Håkon Hansen Arkitektonisk Prosjekterende: Norsk Byggservice AS
Tegningsfase: Tegningen er arkitektonisk prosjektert Tegning: Situasjonsplan			Format: A3 1:500 Oppstartsdato: 15.05.2023 Tegningsnr.: 94940 D-01