
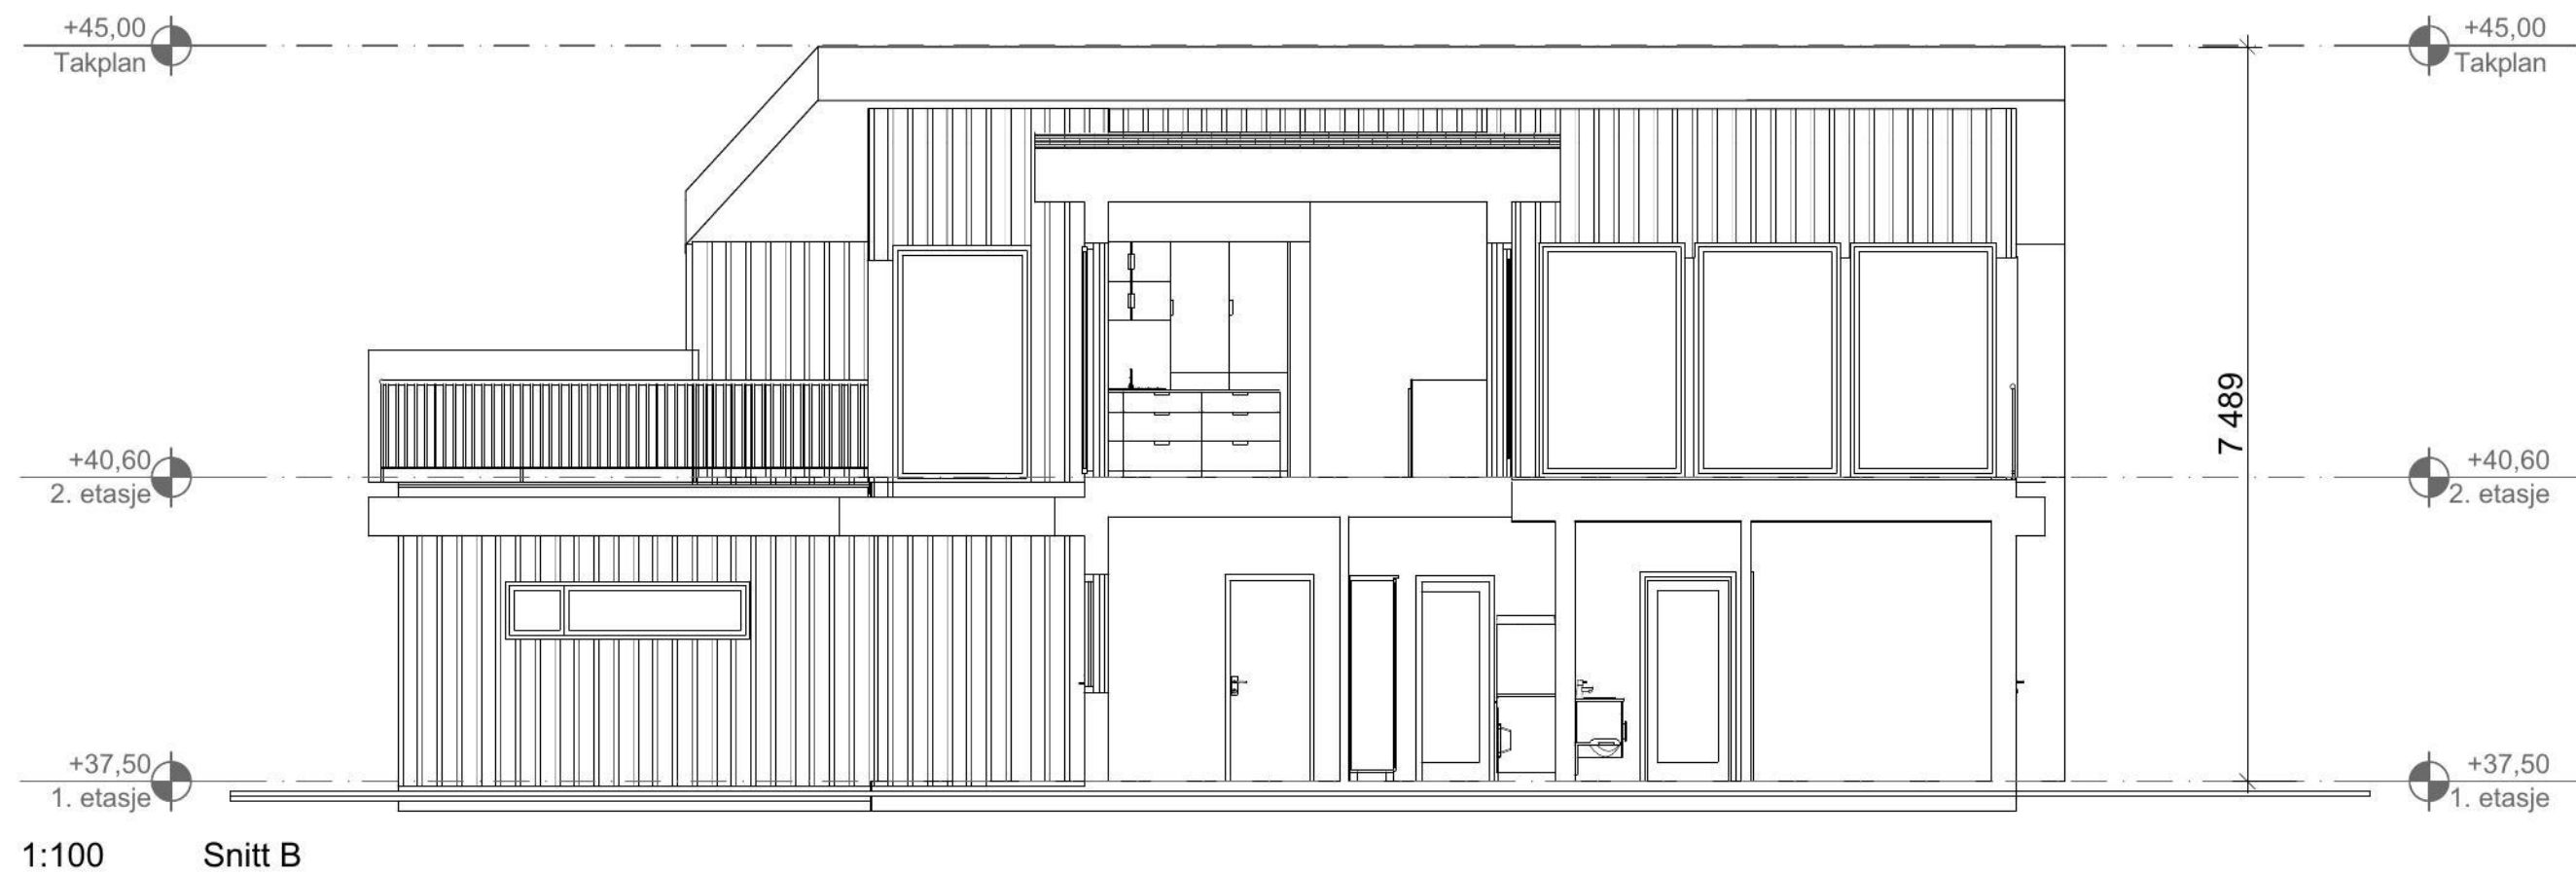


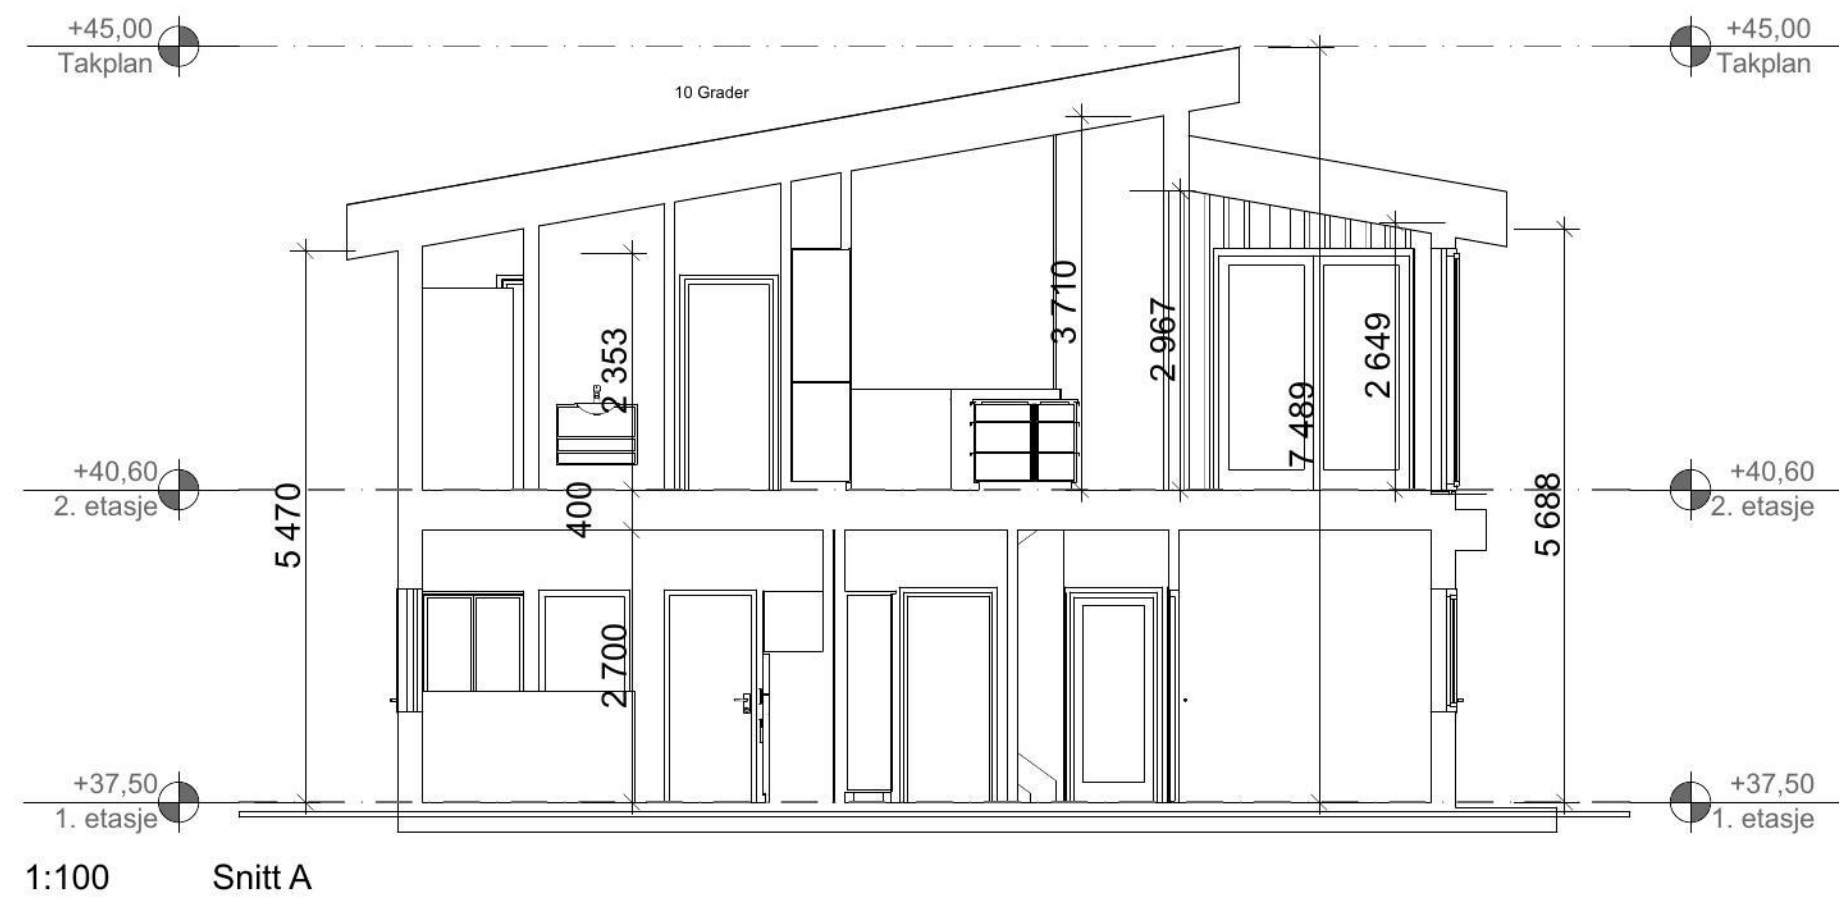

Prosjekt: Villa Kristensen/Michalsen	Kontroll prosjekt:	
	Sign.:	Kontroll:
Tiltakshaver: Morten Kristensen & Rebecca Michaelsen Holtheia 26 4639 Kristiansand.s,	Gnr./Bnr./Festnr.: 92/361	
Prosjekterende: Choose design & interiør Hånestangen 91 4635 Kr.sand S.		
© Alle rettigheter tilhører utførende for prosjektering, kopiering eller bruk av disse tegningene er forbudt uten skriftlig samtykke	Dato: 07.07.23	
Tegning: Snitt A og B	Målestokk: 1:100	
	Tegningsnr.:	Rev.:
	A30-1	