


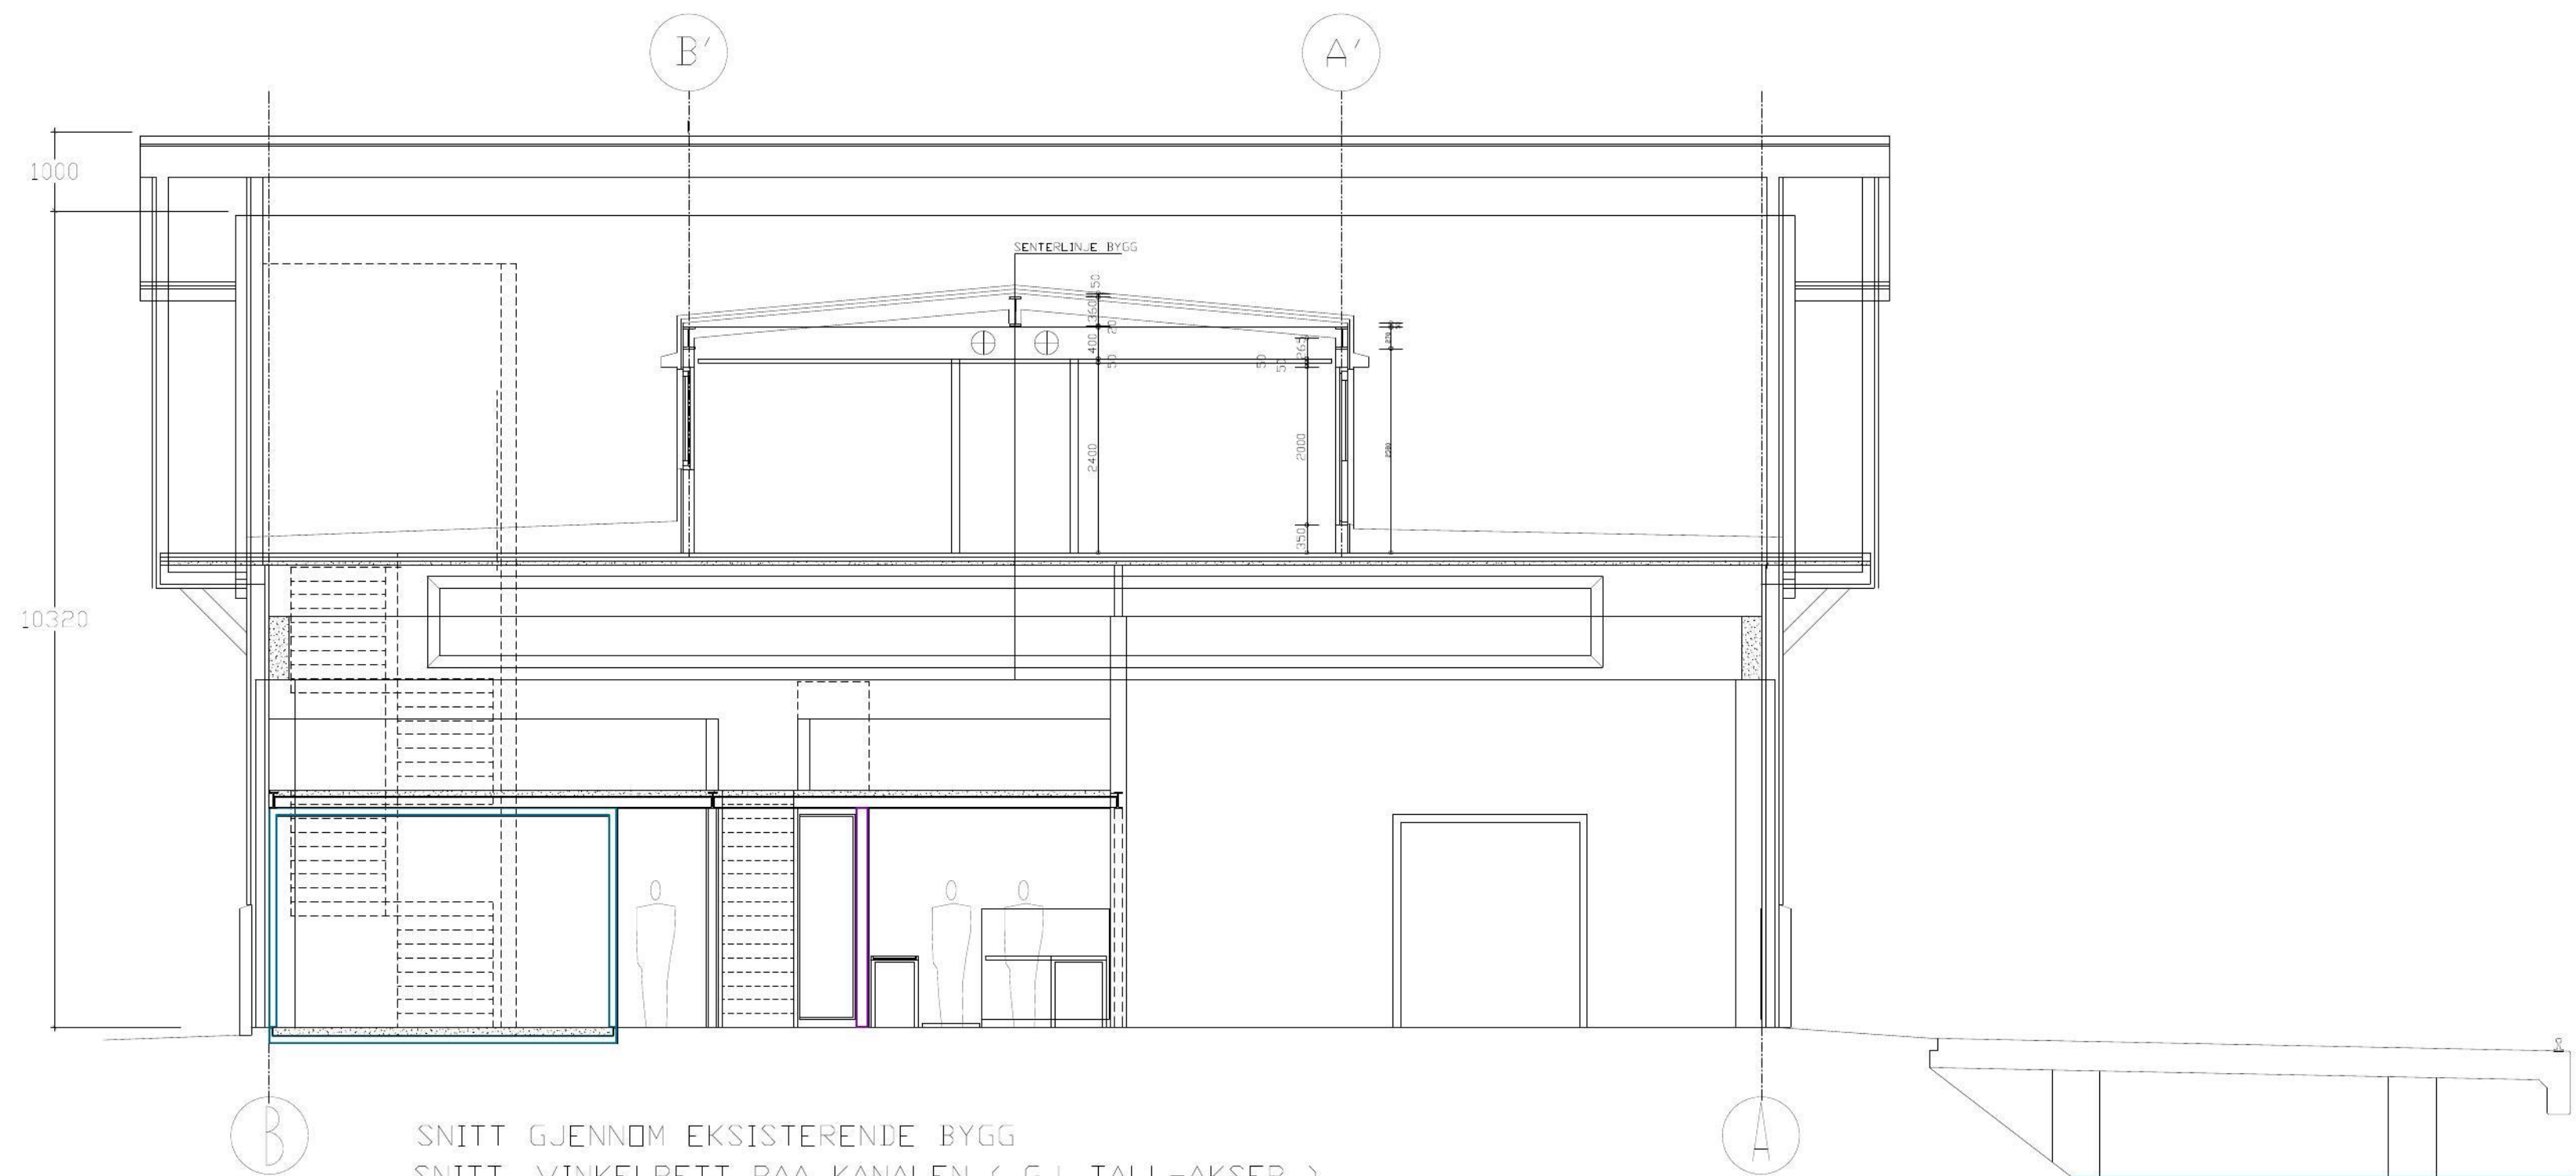

SNITT GJENNOM EKSISTERENDE BYGG
SNITT, VINKELRETT PÅ KANALEN (GJ. TALL-AKSER)
SNITT GJELDER OGSÅ SOM PRINSIPPSNITT FOR NYTT BYGG

PROSJEKT		KRS.HAVN: SKAGERAKFISKBYGGET	
NIVÅ		UTVIDELSE AV SKAGERAKFISKBYGGET I H2	
TEGNING		SNITT	
MÅL	TEGN. AV	LØVDAHL:AS SIVILARKITEKT M.N.A.L. KJERKEHEIA no 18 4790 LILLESAND mobil: 900 36 604 e-post: jan.lovdahl@lovdahl-as.no	
TÆT	ANSV.		
06.09.2023	JEL		