

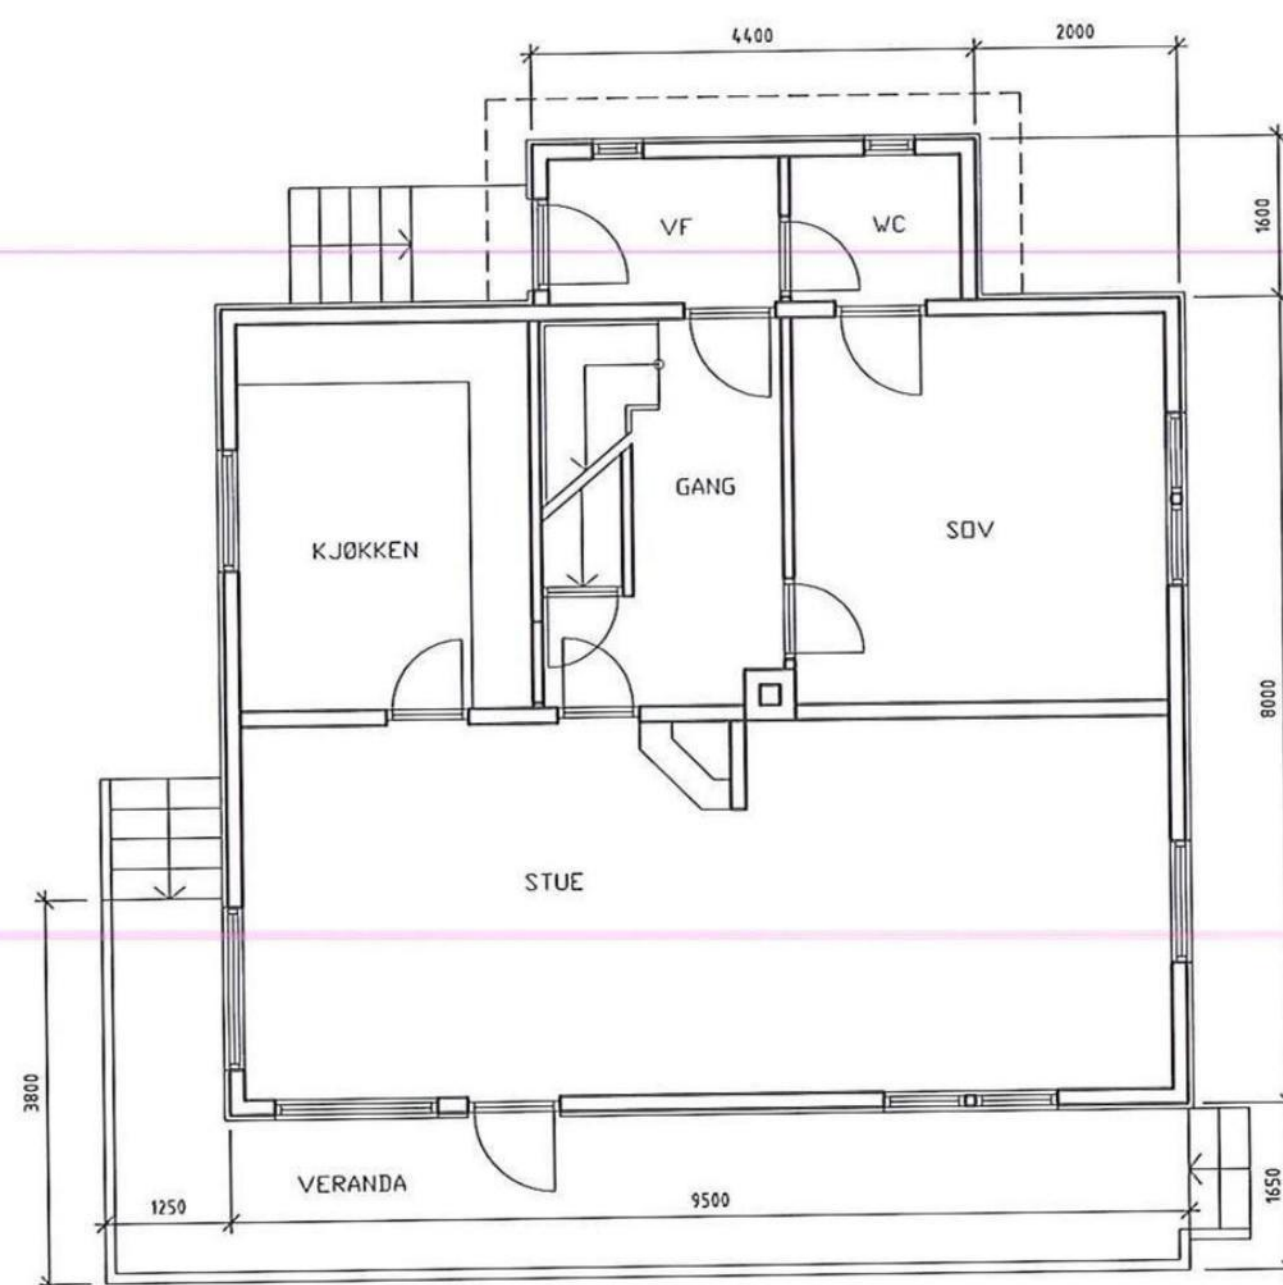


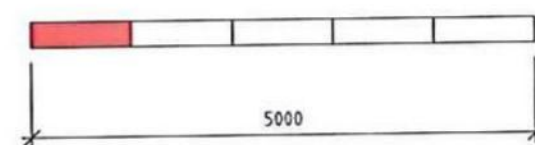

HØVEDETASJE,
EKSISTERENDE
BYA 103,5 m²
BRA 76,5 m²

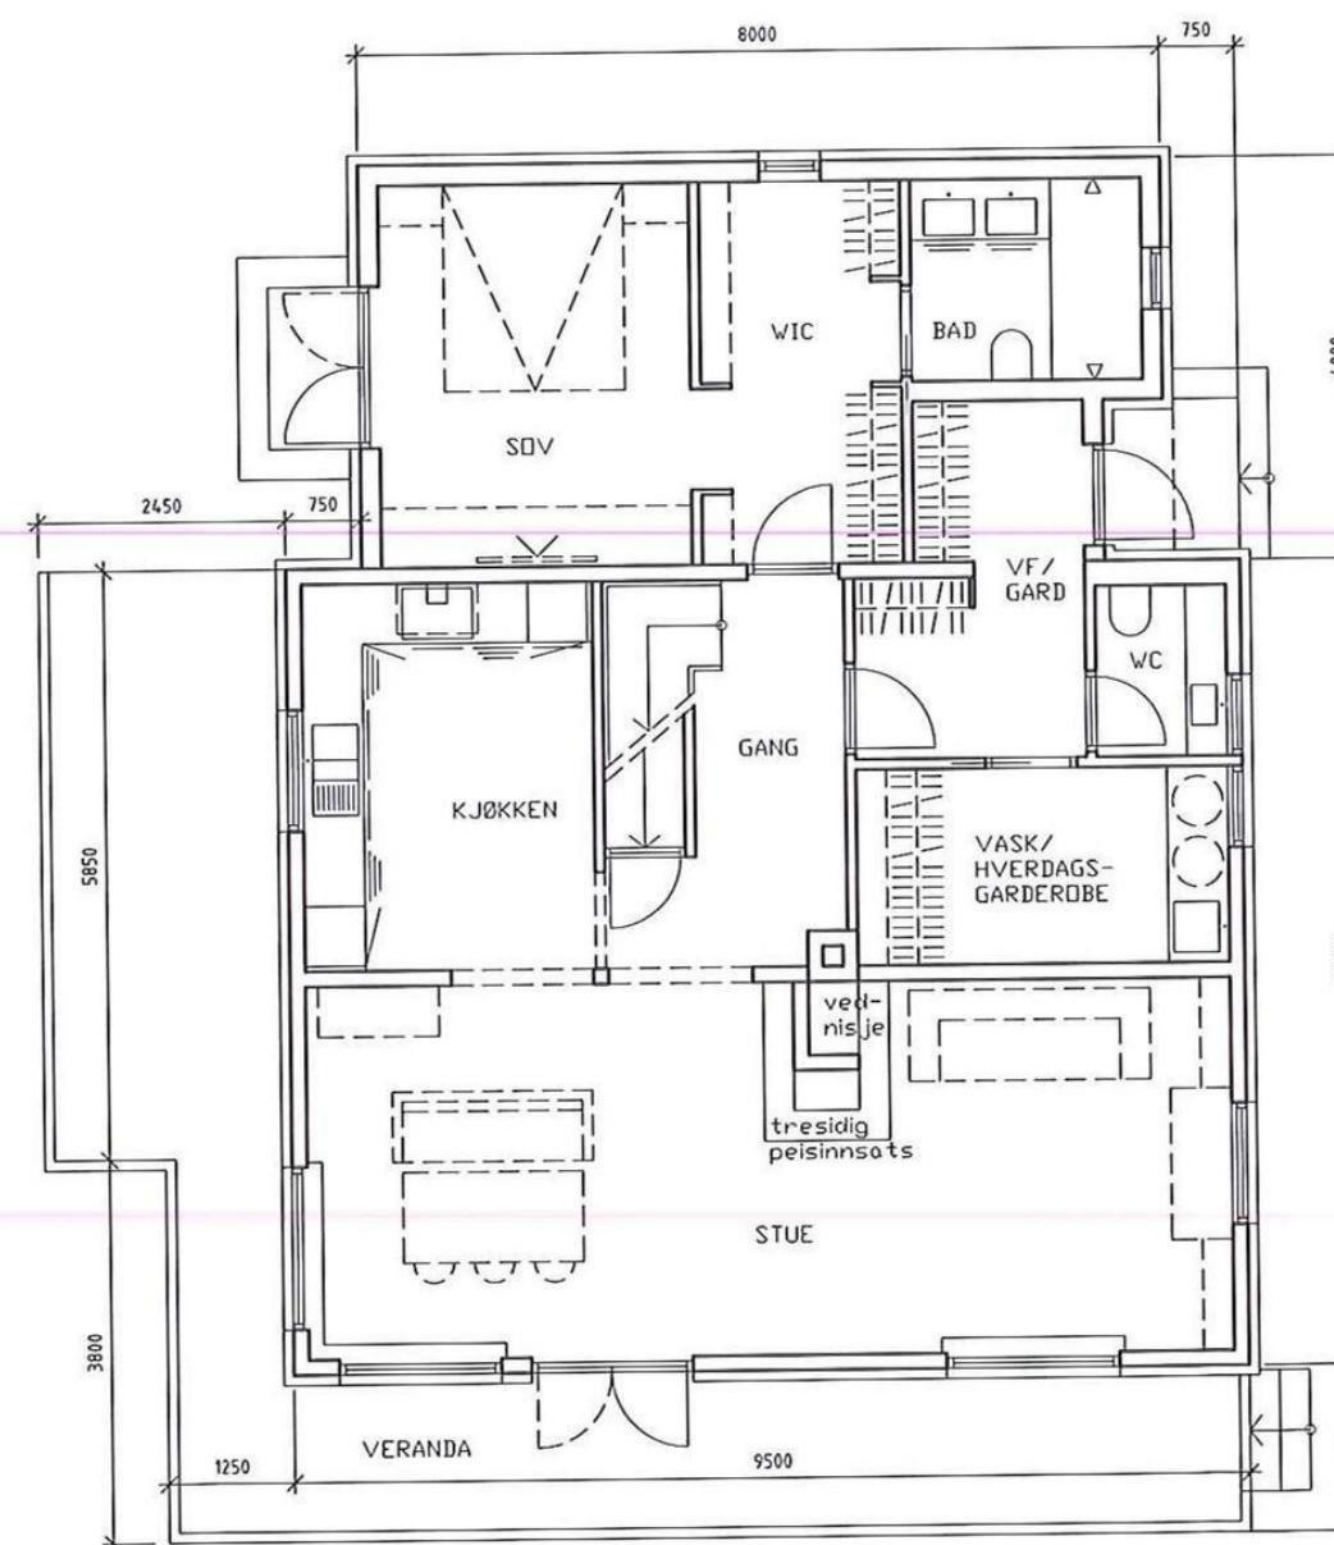

HØVEDETASJE,
ENDRINGSFØRSLAG
BYA 142,8 m²
BRA 99,4 m²

Nivå	UTVIDELSESFØRSLAG	
Prosjekt	ASPERØYVEIEN 9	
Byggherre	KOBELTVEDT	
Tegning	Plan, snitt og fasader	
Mål	1:100	
Dato	01.02.2016	
sivilarkitekt NINA STOKSET NILSEN Holbergsgate 11, 4614 Kristiansand Mobil 45454214		