
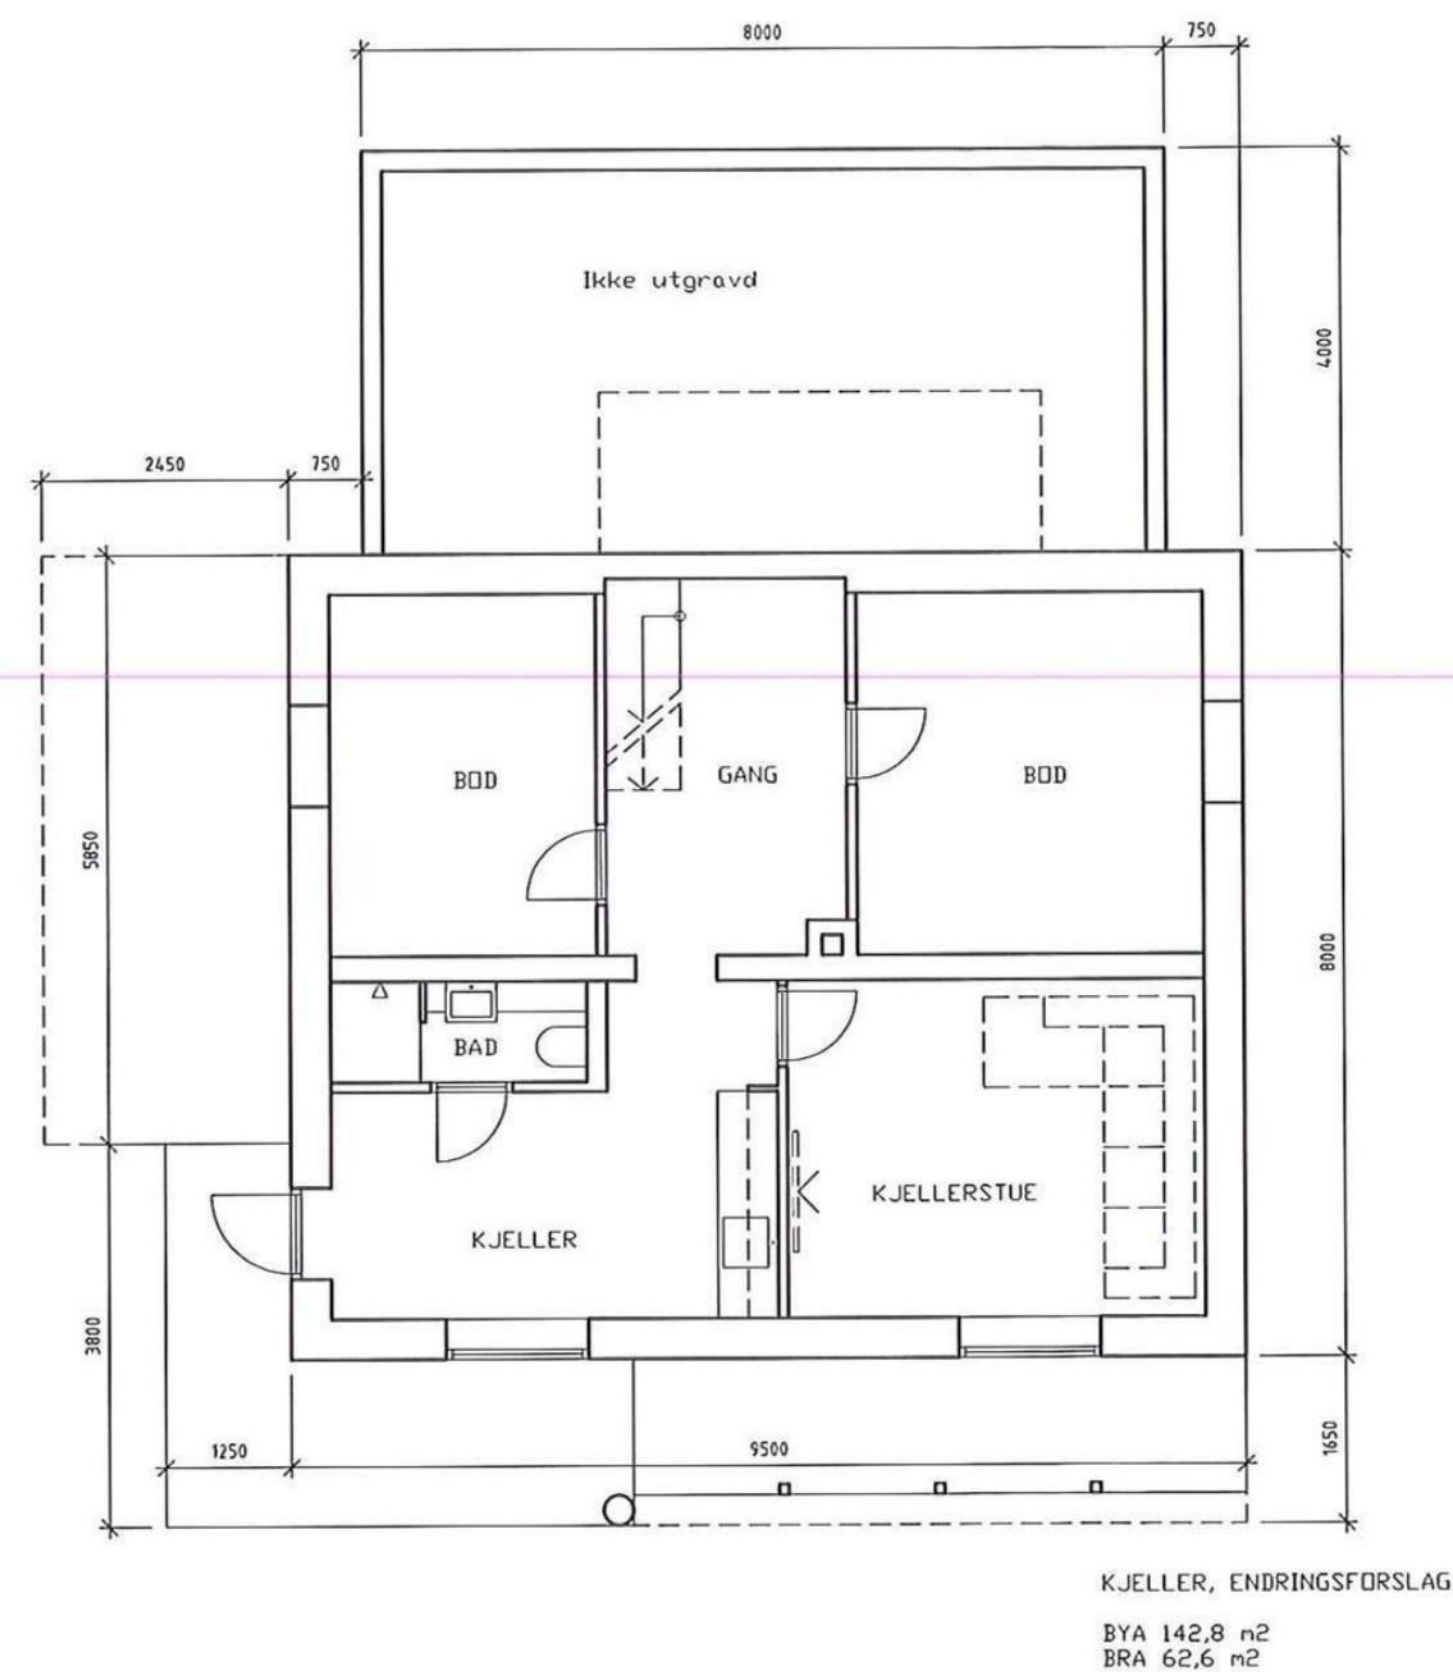


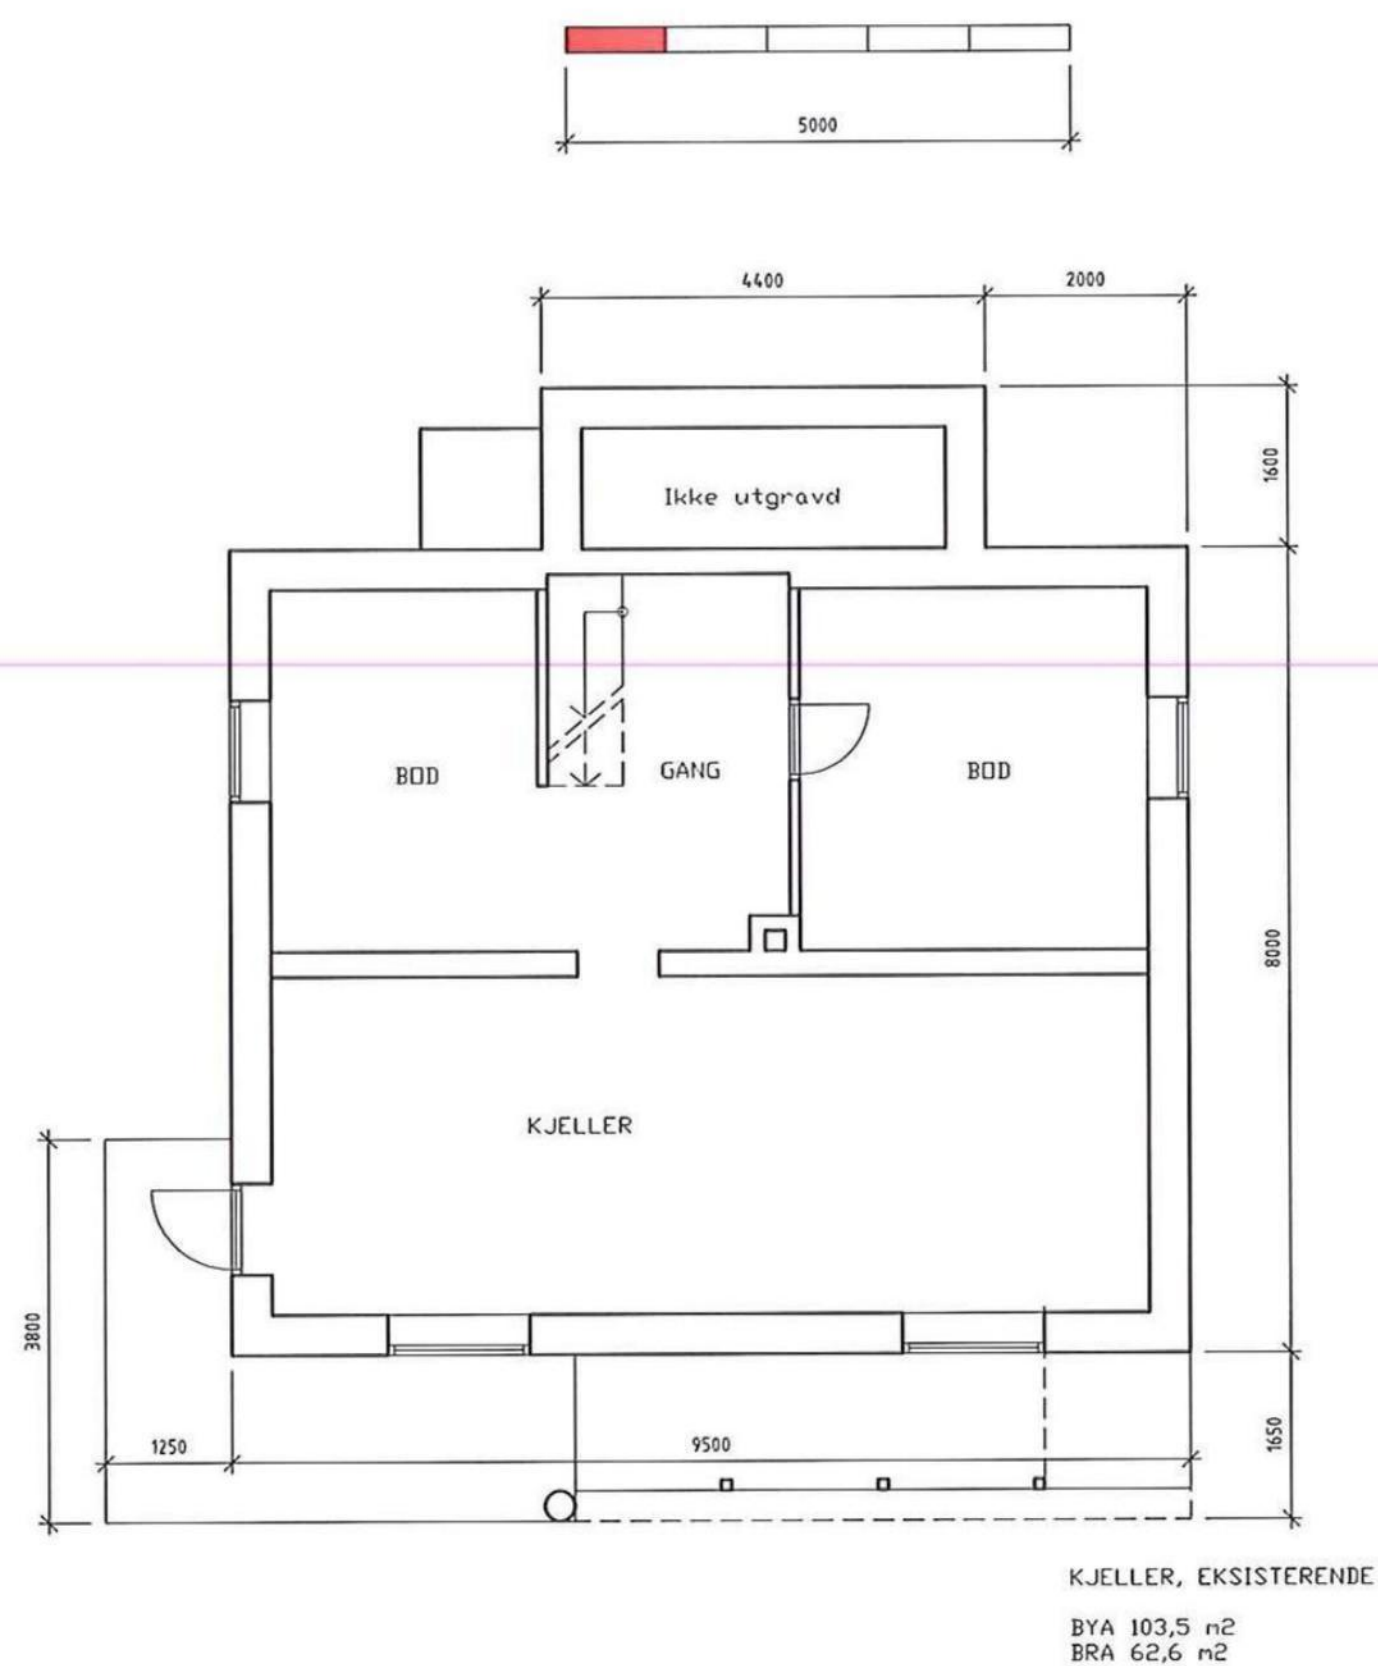

Nivå	UTVIDELSESFØRSLAG	
Prosjekt	ASPERØYVEIEN 9	
Byggherre	KOBELTVEDT	
Tegning	Plan, snitt og fasader	
Mål	1:100	
Dato	01.02.2016	
sivilarkitekt NINA STOKSET NILSEN Holbergsgate 11, 4814 Kristiansand Mobil 45454214		