



BYGGEMELDINGSTEGNING

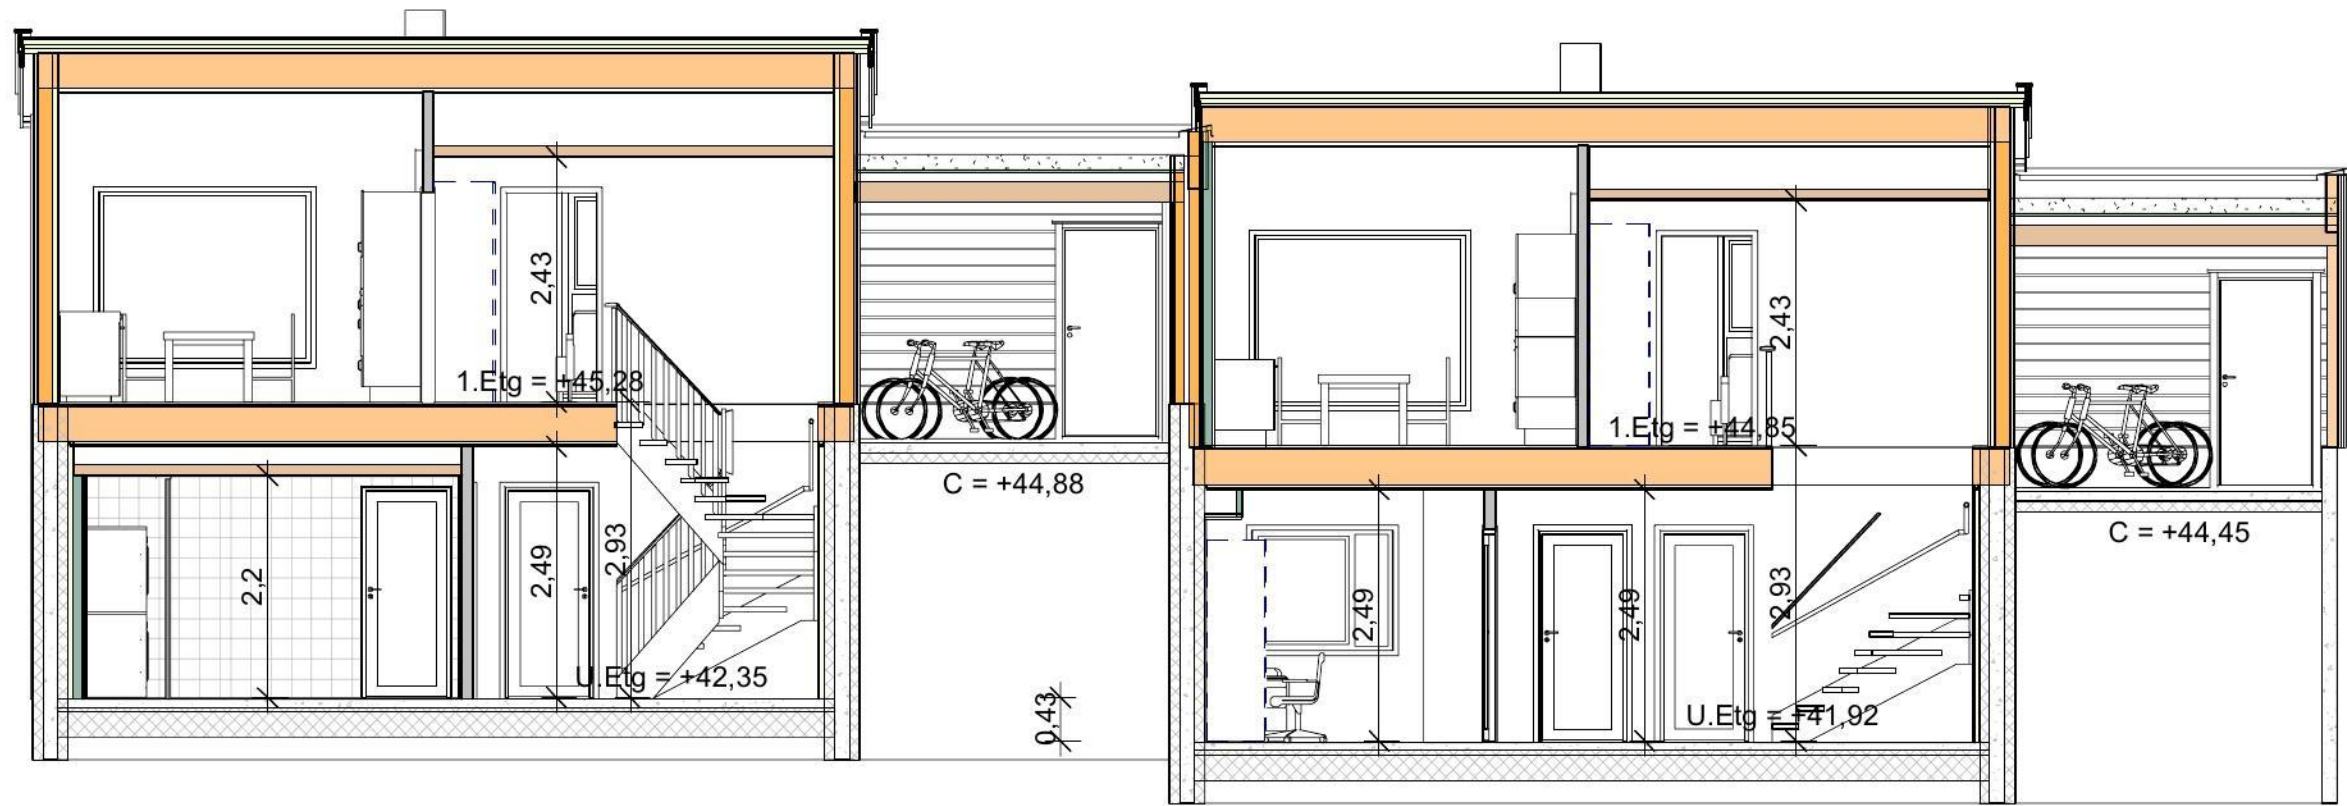

Snitt 1
1 : 100

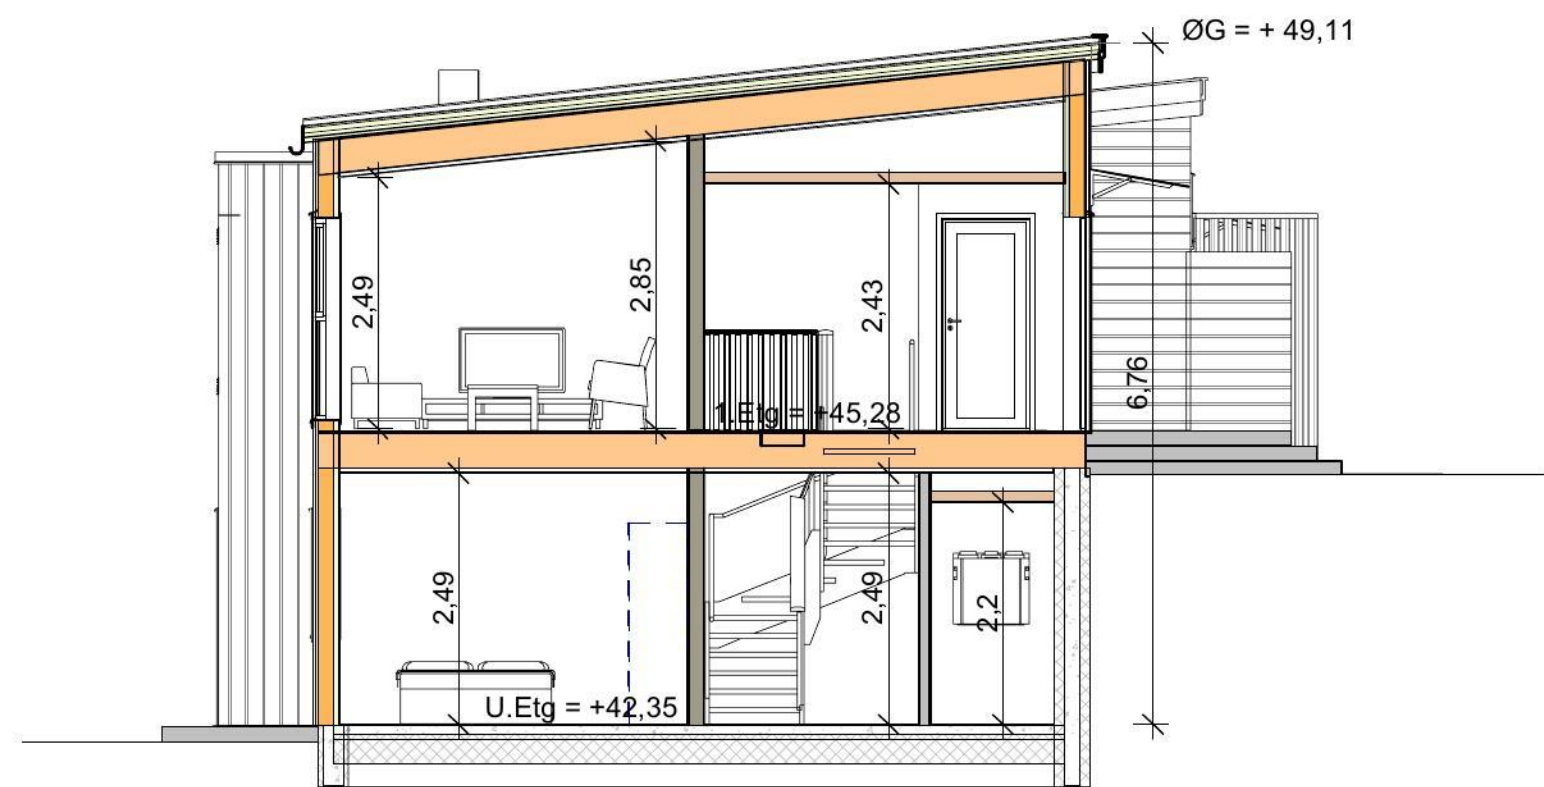

Snitt 2
1 : 100

Lokaliseringsfigur:



Rev.	Revisjonen gjelder	Dato	Utført	Kontr.
Tegningsnavn	Snitt 1	Dato	Tegnet	Kontr.
		26.07.23	M.E.	T.A.
Tiltakshaver: OBOS Block Watne AS				
Byggeplass: Benestadheia 145-147				
Prosjektnavn: DRANGSVANN BKS16 - HUS 104-105				
G.NR./B.NR. 67/228-229		Målestokk As indicated		Arkstørrelse A2
KOMMUNE: KRISTIANSAND		TEGNINGSTYPE: XX A SN 20 1		
HUSTYPE: -		BOLIGTYPE: Kjedet enebolig		
Tegningsnr. 137990804		XX A SN 20 1 F 0		
PROSJEKTNUMMER		ETASJE FAG TYPE DISIPLIN LØPENR FASE REVISJON		