


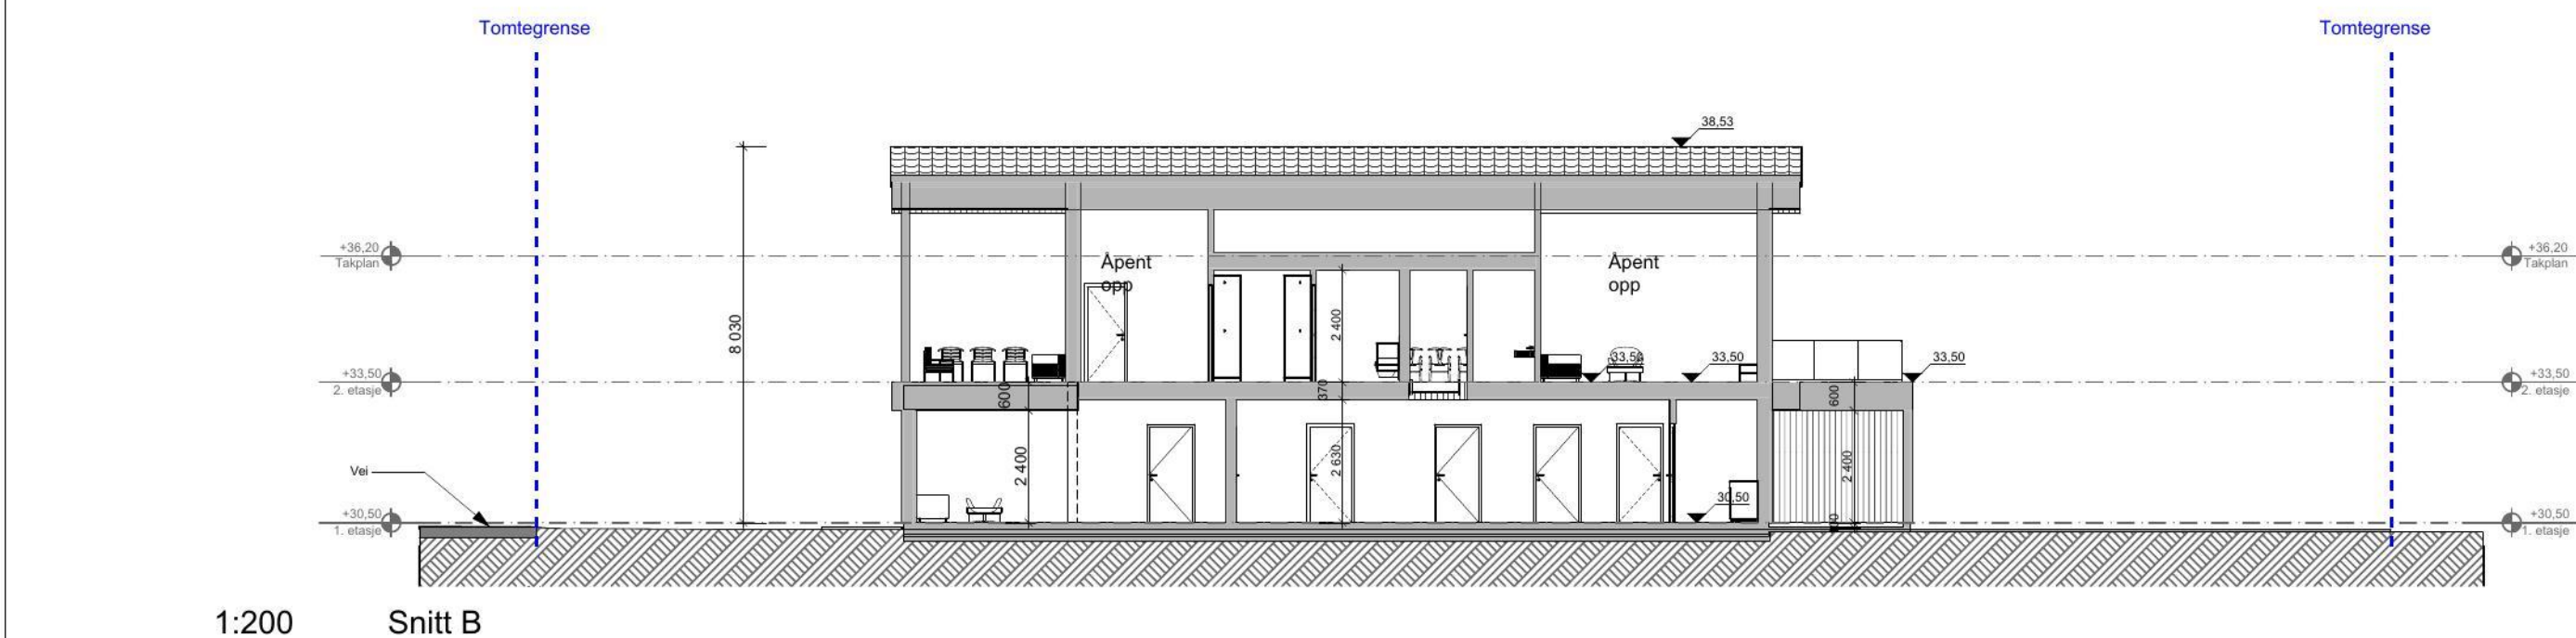

1:200 Schnitt B

Tegningsnr.. A30-01	Revisjon nr..	
Type tegning Snitt A og B		
Tomt:	841,8 m2	
BYA: bolig og garasje m/2 p-plasser (199,8 m2) + overbygg garasje (11,9 m2 + 3,3 m2)	215,0 m2	
Utnyttelse BYA:	25,5%	
BRA: 1. etasje (134,5 m2) + garasje (35,7 m2) + Sportsbod (7,7 m2) + overbygd inngangsparti (11,9 m2) + overbygg bakside garasje (3,3 m2) + 2. etasje (108,2 m2) + overbygd terrasse (25,8 m2)	327,1 m2	
Oppvarmet BRA: 1. etasje (134,5 m2) + 2. etasje (108,2 m2)	242,7 m2	
Prosjekteringsgruppen		
● ARK : Agderbygg AS		Gyldenløves gate 99 4614 Kristiansand Tlf.: 918 89 661 tm@agderbygg.no
Fase		
Byggemelding		
 AGDERBYGG		
Tiltakshaver		Godkjent
Marius Byklum Jakobsen		Kontroll prosjekt.
Rismyrbakken 25 4645 Nodeland		Sign.. Kontroll
		Filnavn Birkenesvegen 6.pln
		Dato 10.08.2023
		Målestokk 1:200, 1:100
		Kontroll utførelse
Gnr./Bnr./Festenr.: 578/275	Sign.. Kontroll	Prosjektnr.. for prosjekterende/lev.
Prosjektnr.: Prosjektnr.	Tegningsnr.: A30-01	
Type tegning: Snitt A og B		