



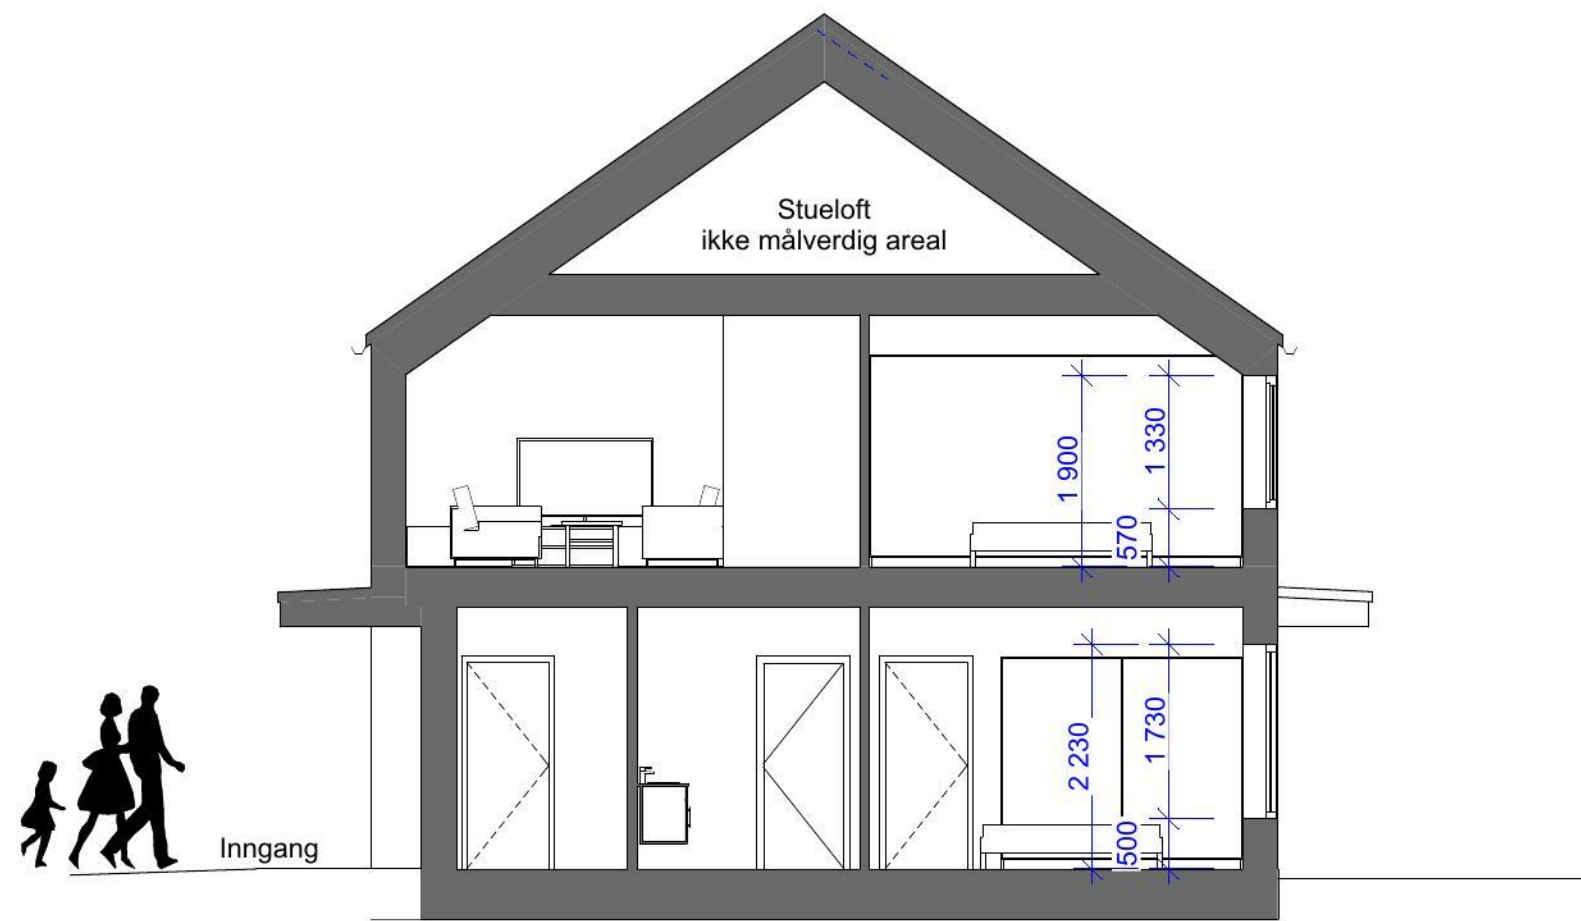

1:100 Snitt B

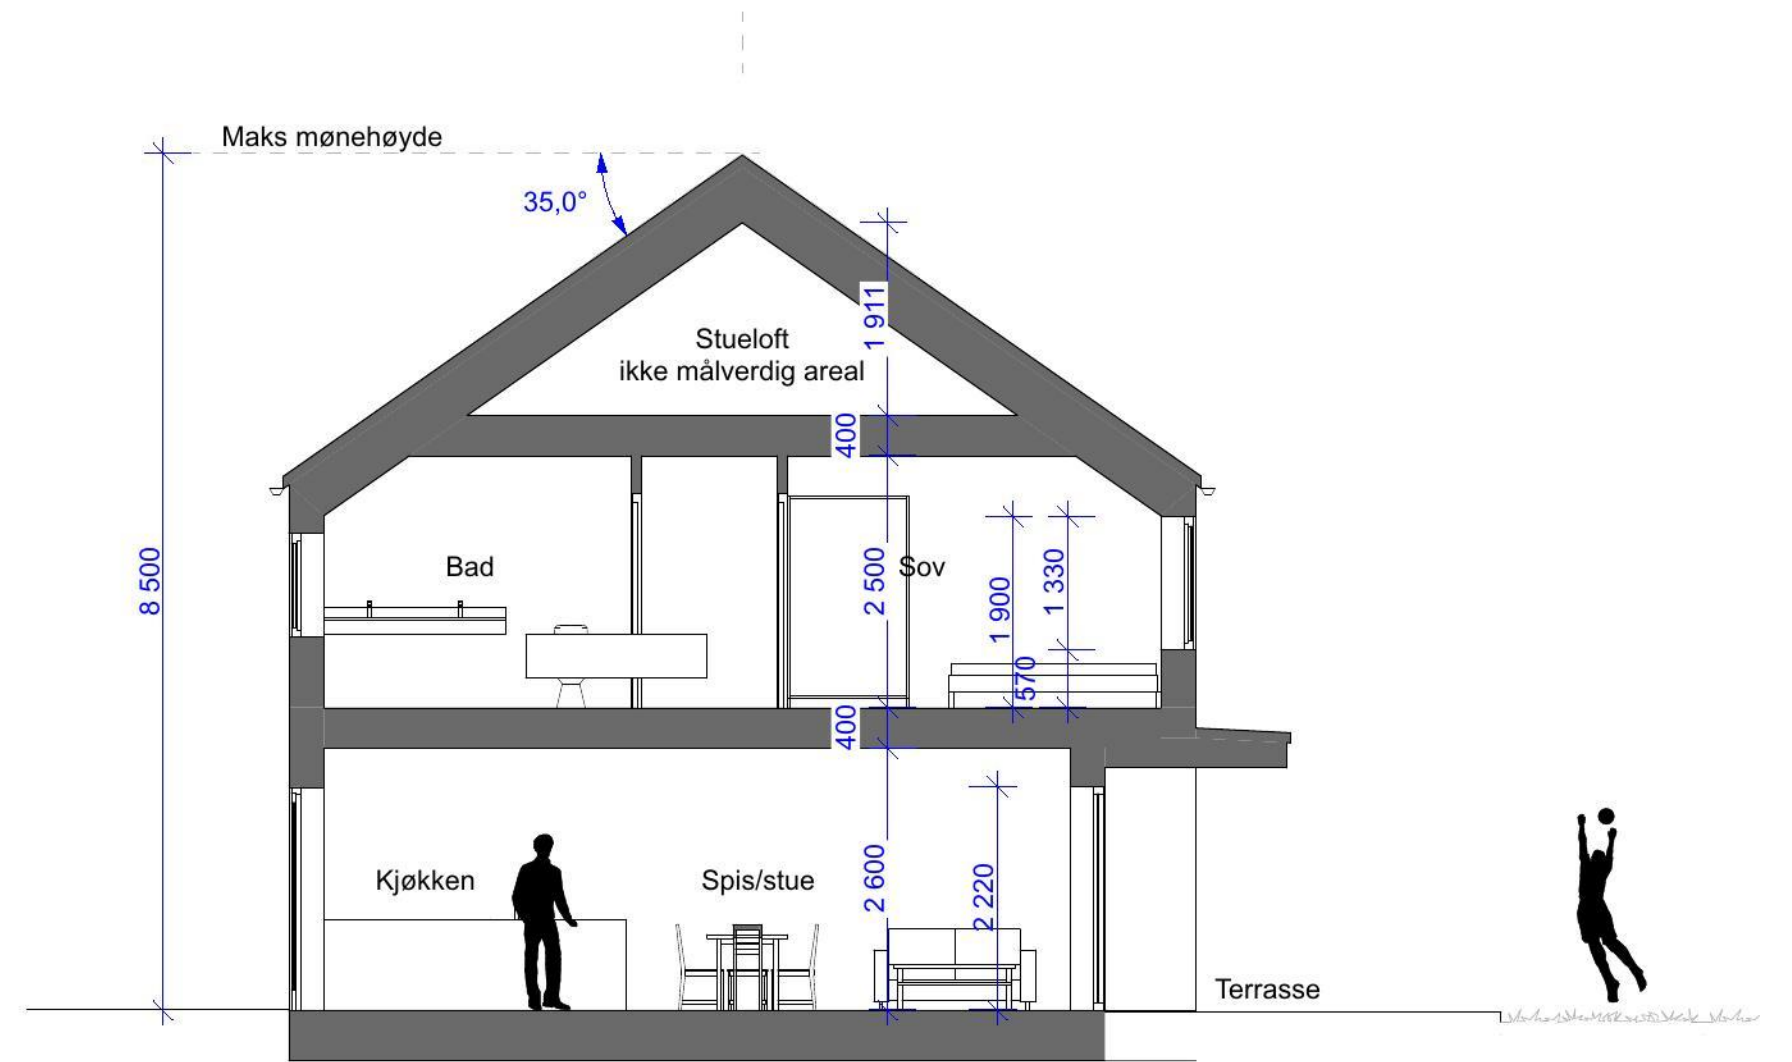

1:100 Snitt A

Prosjekt: Lille Kartemyrvei 14	Gnr./ Bnr.: 151/2964	Tegningsnr.: A30-S01	Fase: RAMMESØKNAD	Tegnet: ESTR	Arkitekt: ESTR	Godkjent:
Oppdragsgiver: Aamodt Hus AS	Prosjektnr.: 23002	Tegningsnavn: Snitt A og B	Målestokk: 1:100	Ark: A3	Høydesystem: NN2000	Dato: 13.06.2023
						Rev. .

