




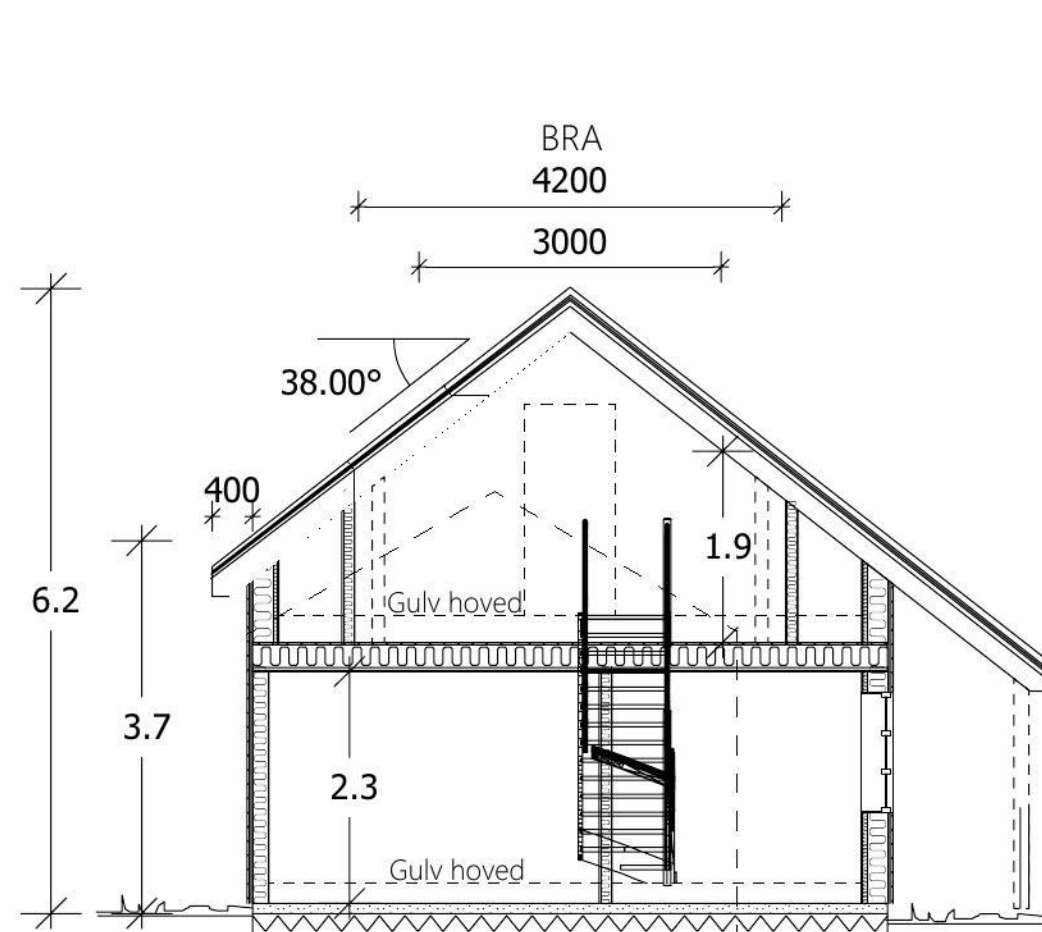

SNITT B - B

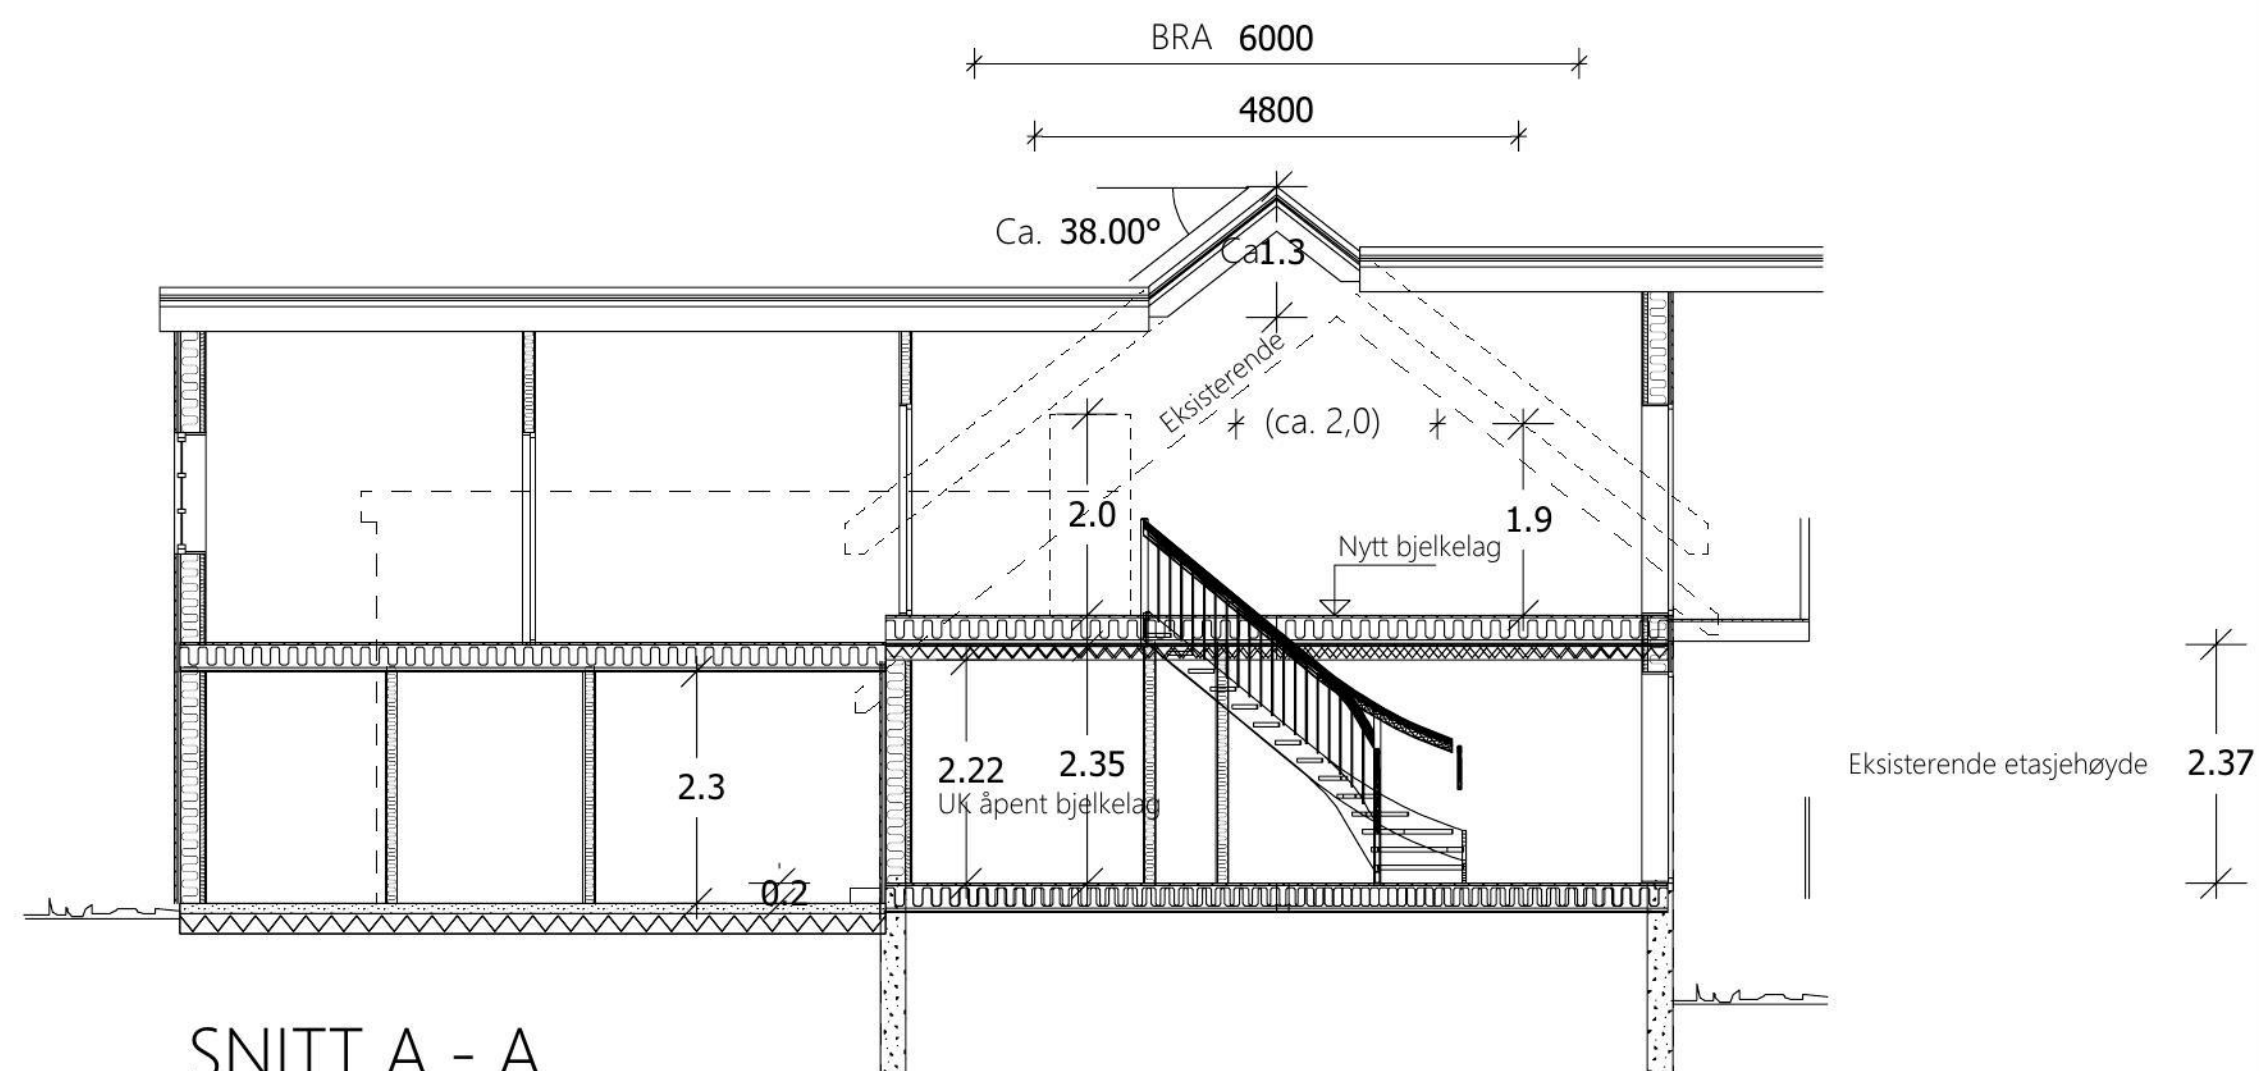

SNITT A - A

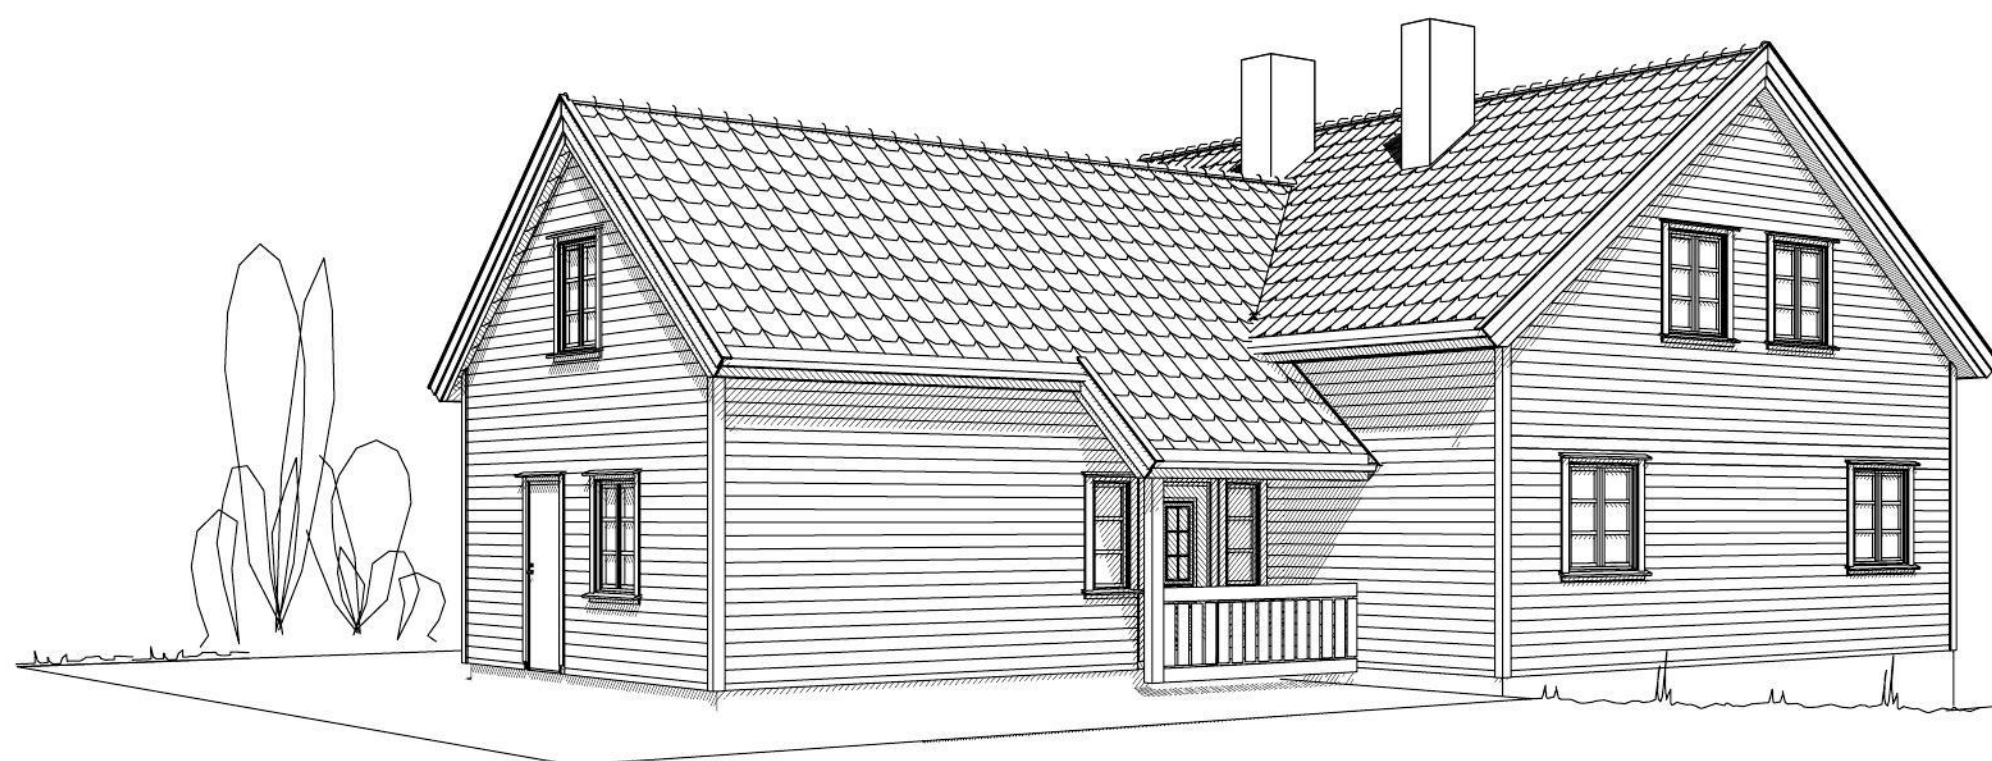

C	Vinduer loft	AC18	16.08.2023
B	Justering vinduer og kvist	AC18	04.07.2023
A	Kvist	AC18	12.06.2023

DATA DESIGN SYSTEM

REV.	ANT.	REVIDERINGEN GJELDER	SIGN.	DATO
------	------	----------------------	-------	------

Tilbygg / påbygg	Bjørn Arild Stea	G.NR. 420	B.NR. 3
Snitt	Gamle Årosvei 64	KOMMUNE: Kr.sand	
 Flatnes Bygg Consult	TEGN. AME	PROSJ.NR.	
	GODKJ.	3187	
	MÅL 1 : 100	TEGN. NR.	
	DATO 25.05.2023	506	

TEGNINGEN MÅ HVERKEN HELT ELLER DELVIS KOPIERES ELLER BENYTTES TIL UTFØRELSE AV ARBEID SOM FLATNES BYGG CONSULT AS IKKE MEDVIRKER I