


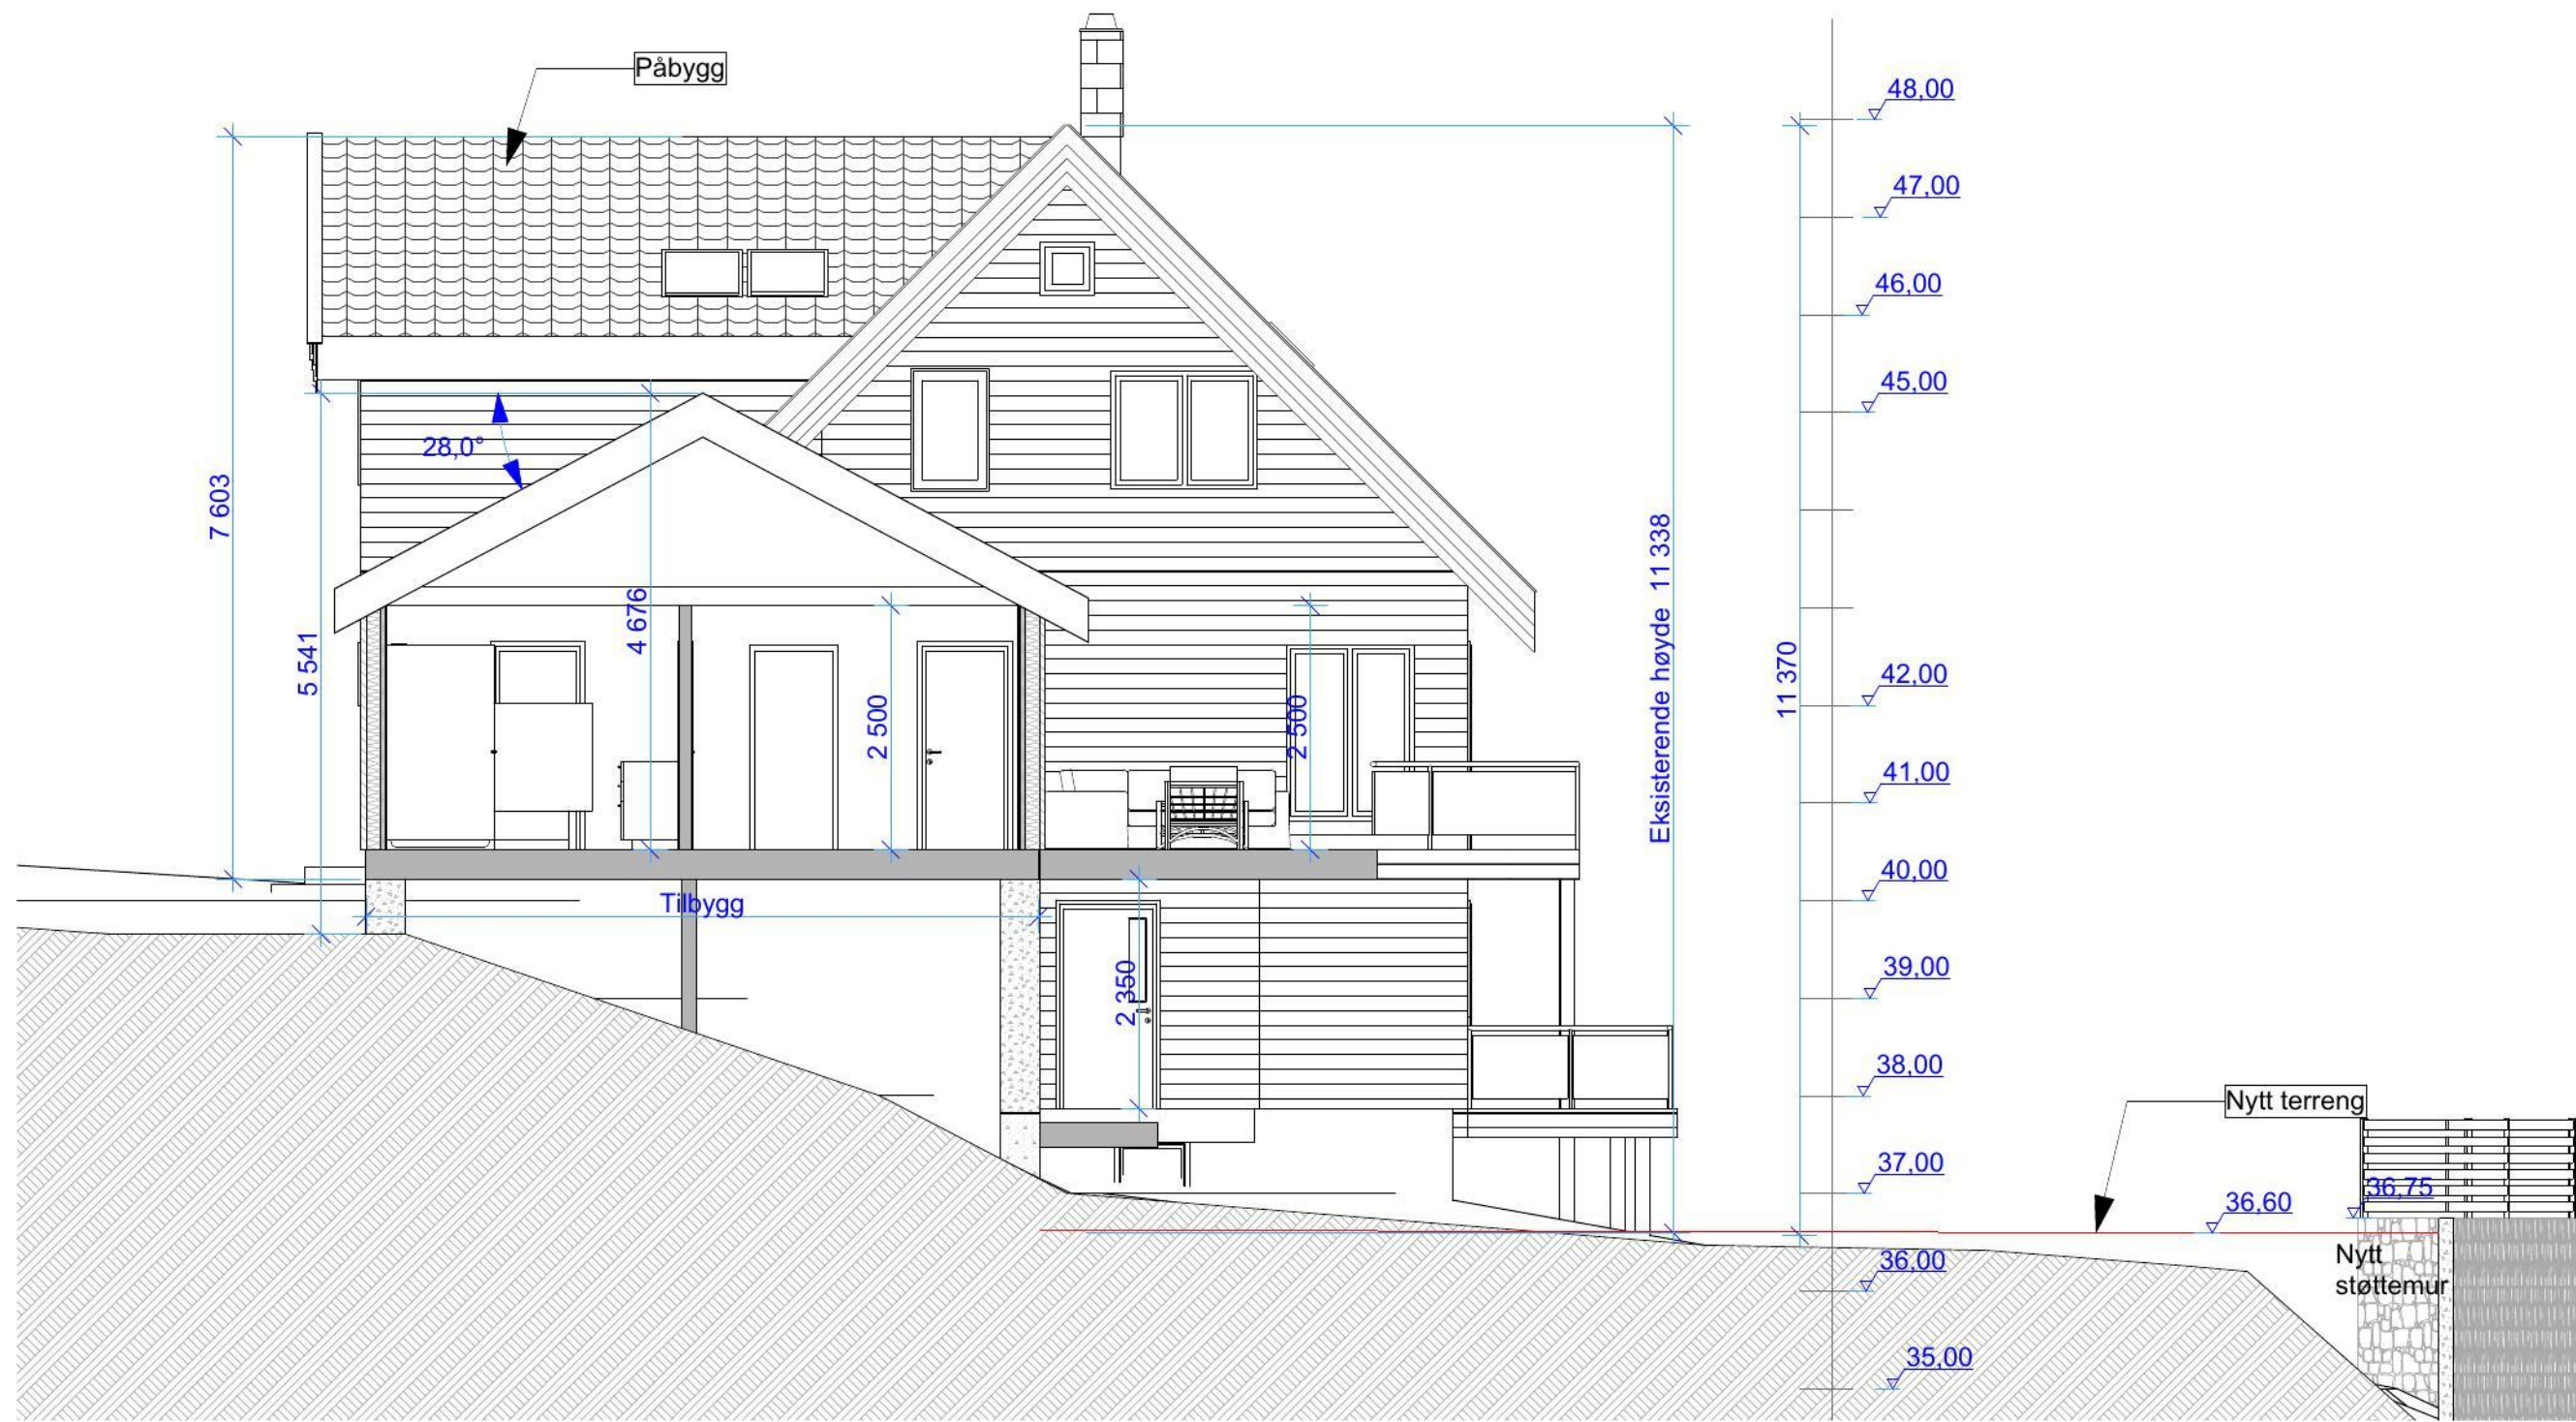

Snitt A-A

Situasjonskartet er hentet fra kommunens kart base, men kan inneholde feil.

-	-	-	-
-	-	-	-
-	-	-	-
-	-	-	-
-	-	-	-
-	-	-	-
Rev.:	Dato:	Revisjonen gjelder:	Sign:
Prosjekt: Bolig for			
Tiltakshaver: Simen Strømsøyen			
Byggeadresse: Knausveien 3			
Byggested: Gnr. 33 Bnr. 64 Snr. - Fnr. - i Kristiansand kommune.			
Tegningsfase: Byggemeldingstegninger		Format: A3 1:100	Utskriftsdato: 15.06.2023
Tegning: Snitt		Tegningsnr.: 8063	

Norsk Byggservice AS

Johan Sverdrupsgate 3
3256 LARVIK
Tlf: 33 15 69 00
Faks: 38 15 69 01
E-post: petter@norsk-byggservice.no

Signatur: Nina A.

Kontroll: -

Revisjon: -

Arkitektonisk Prosjekterende: