
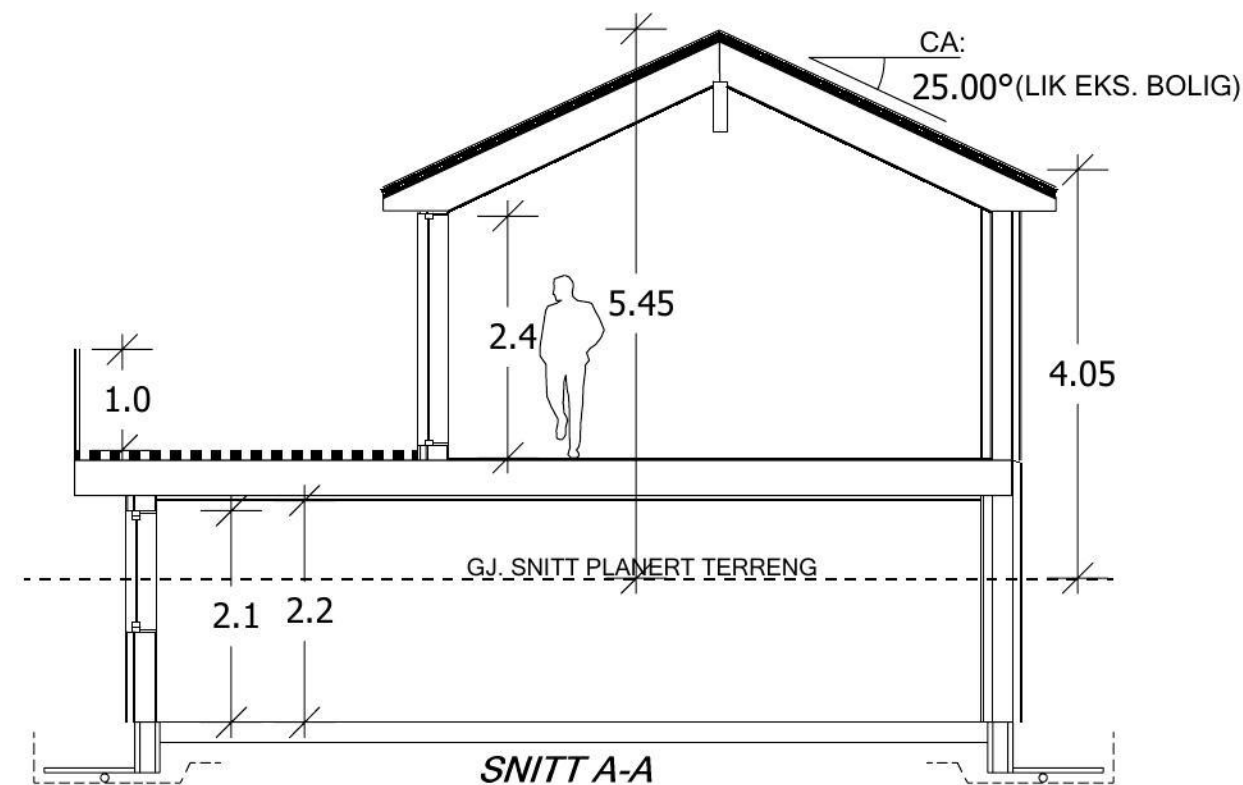
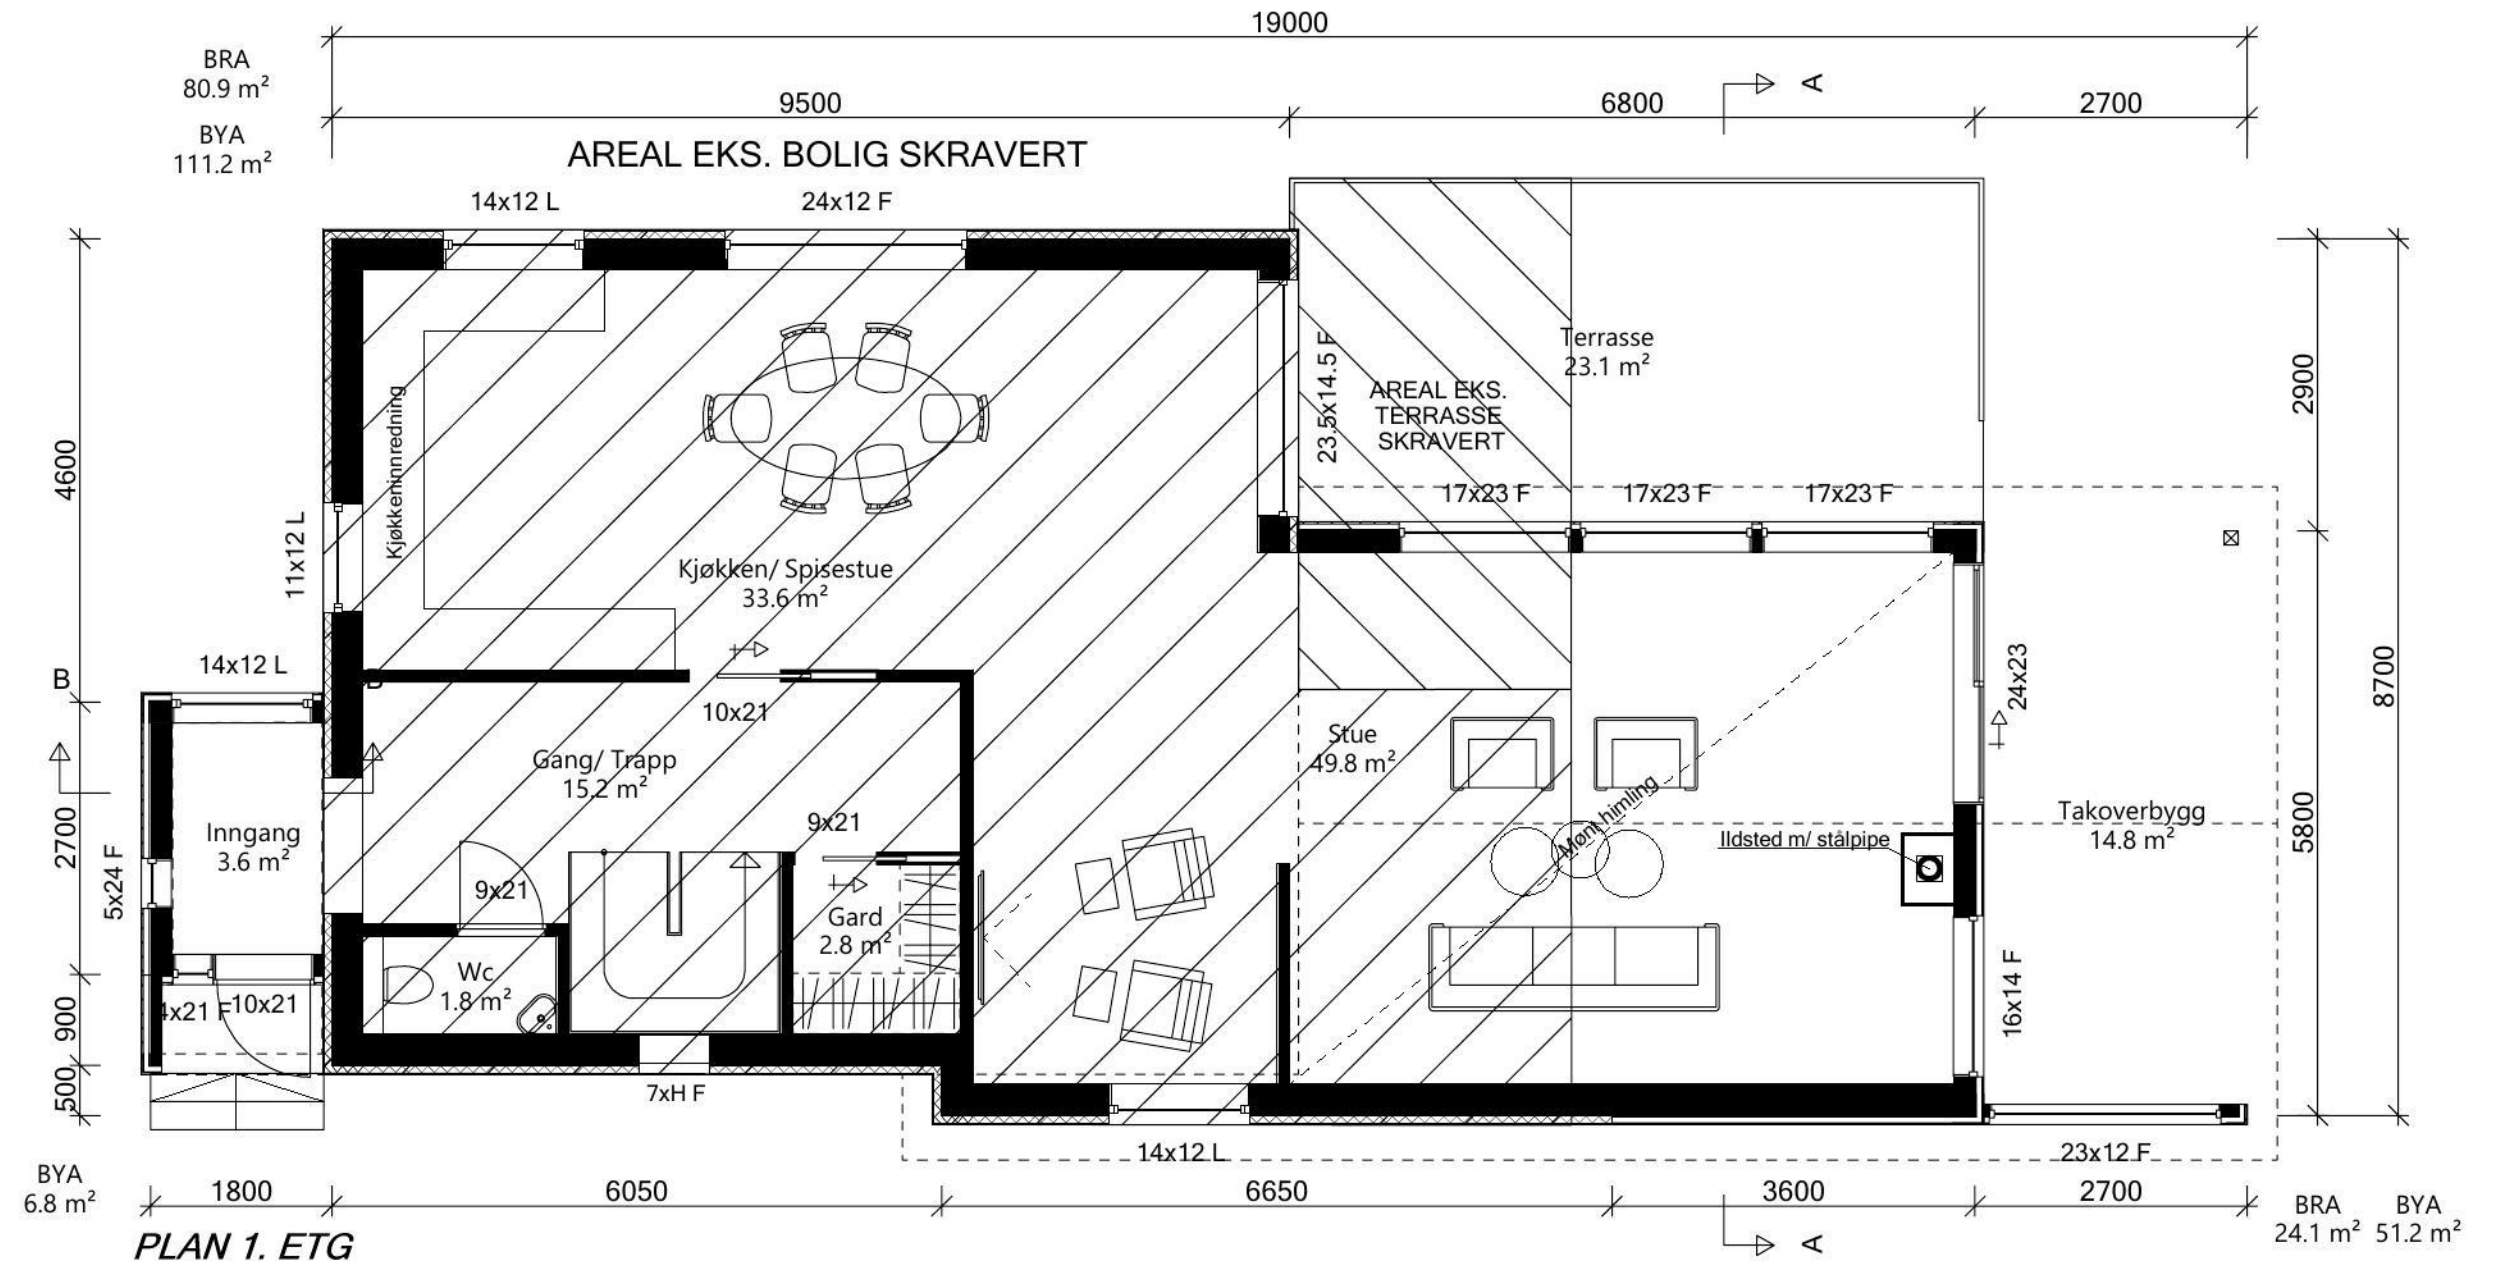


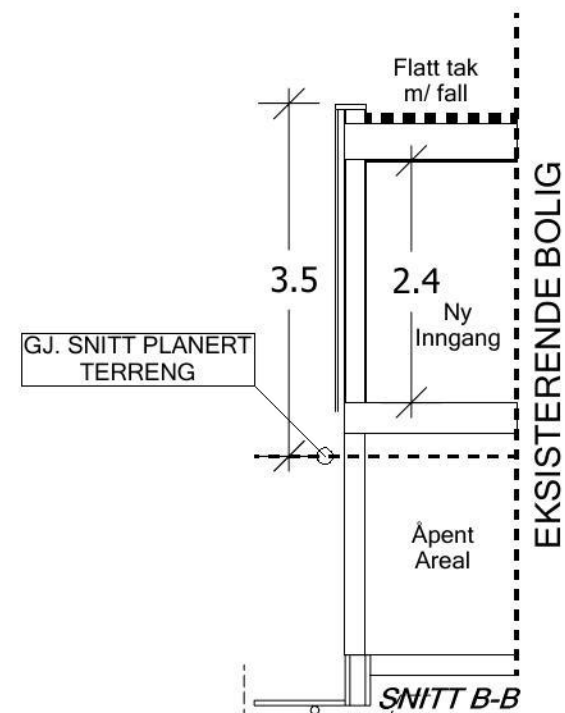

| AREAL EKSISTERENDE:                |                    |         |
|------------------------------------|--------------------|---------|
| Arealberegninger<br>i hht. NS 3940 | Bruksareal BRA kvm |         |
|                                    | Pr etasje          | Sum BRA |
| Kjeller                            | 94.3               | 94.3    |
| 1. etasje                          | 80.9               | 80.9    |
| 2. etasje                          | 70.8               | 70.8    |
| SUM :                              | 246.0              | 246.0   |
| BYA :                              | 111.2              | 111.2   |

| AREAL NYBYGG:                      |                    |         |
|------------------------------------|--------------------|---------|
| Arealberegninger<br>i hht. NS 3940 | Bruksareal BRA kvm |         |
|                                    | Pr etasje          | Sum BRA |
| Kjeller                            | 28.5               | 28.5    |
| 1. etasje                          | 27.7               | 27.7    |
| SUM :                              | 56.2               | 56.2    |
| BYA :                              | 58.0               | 58.0    |

GRAPHISOFT

**Bygg & Prosjekt  
Service as**  
Snekkerveien 22, 4321 Sandnes

TEGNER: Frank Hellenen  
KONTR.:  
MÅL: 1 : 100  
DATO: 11.12.23

| REV.                                                                                               | ANT. | REVIDERING GJELDER | SIGN.         | DATO     |
|---|------|--------------------|---------------|----------|
|   |      |                    |               | 20.12.23 |
| <b>TILBYGG OG ENDRING</b><br>Nils Kverneland<br>Øygardsveien 80, 4327 Sandnes<br>Matrikkel: 38/ 35 |      |                    |               |          |
| PLAN OG SNITT                                                                                      |      |                    |               |          |
| PROSJEKT NR.: 3676                                                                                 |      |                    | TEGN NR.: 500 | REV.:    |