

20.12.23



Sandnes kommune


Situasjonskart

Eiendom: 38/35
Adresse: Øygardsveien 78
Dato: 07.12.2023
Målestokk: 1:500

Areal =
4100 m²



UTM-32

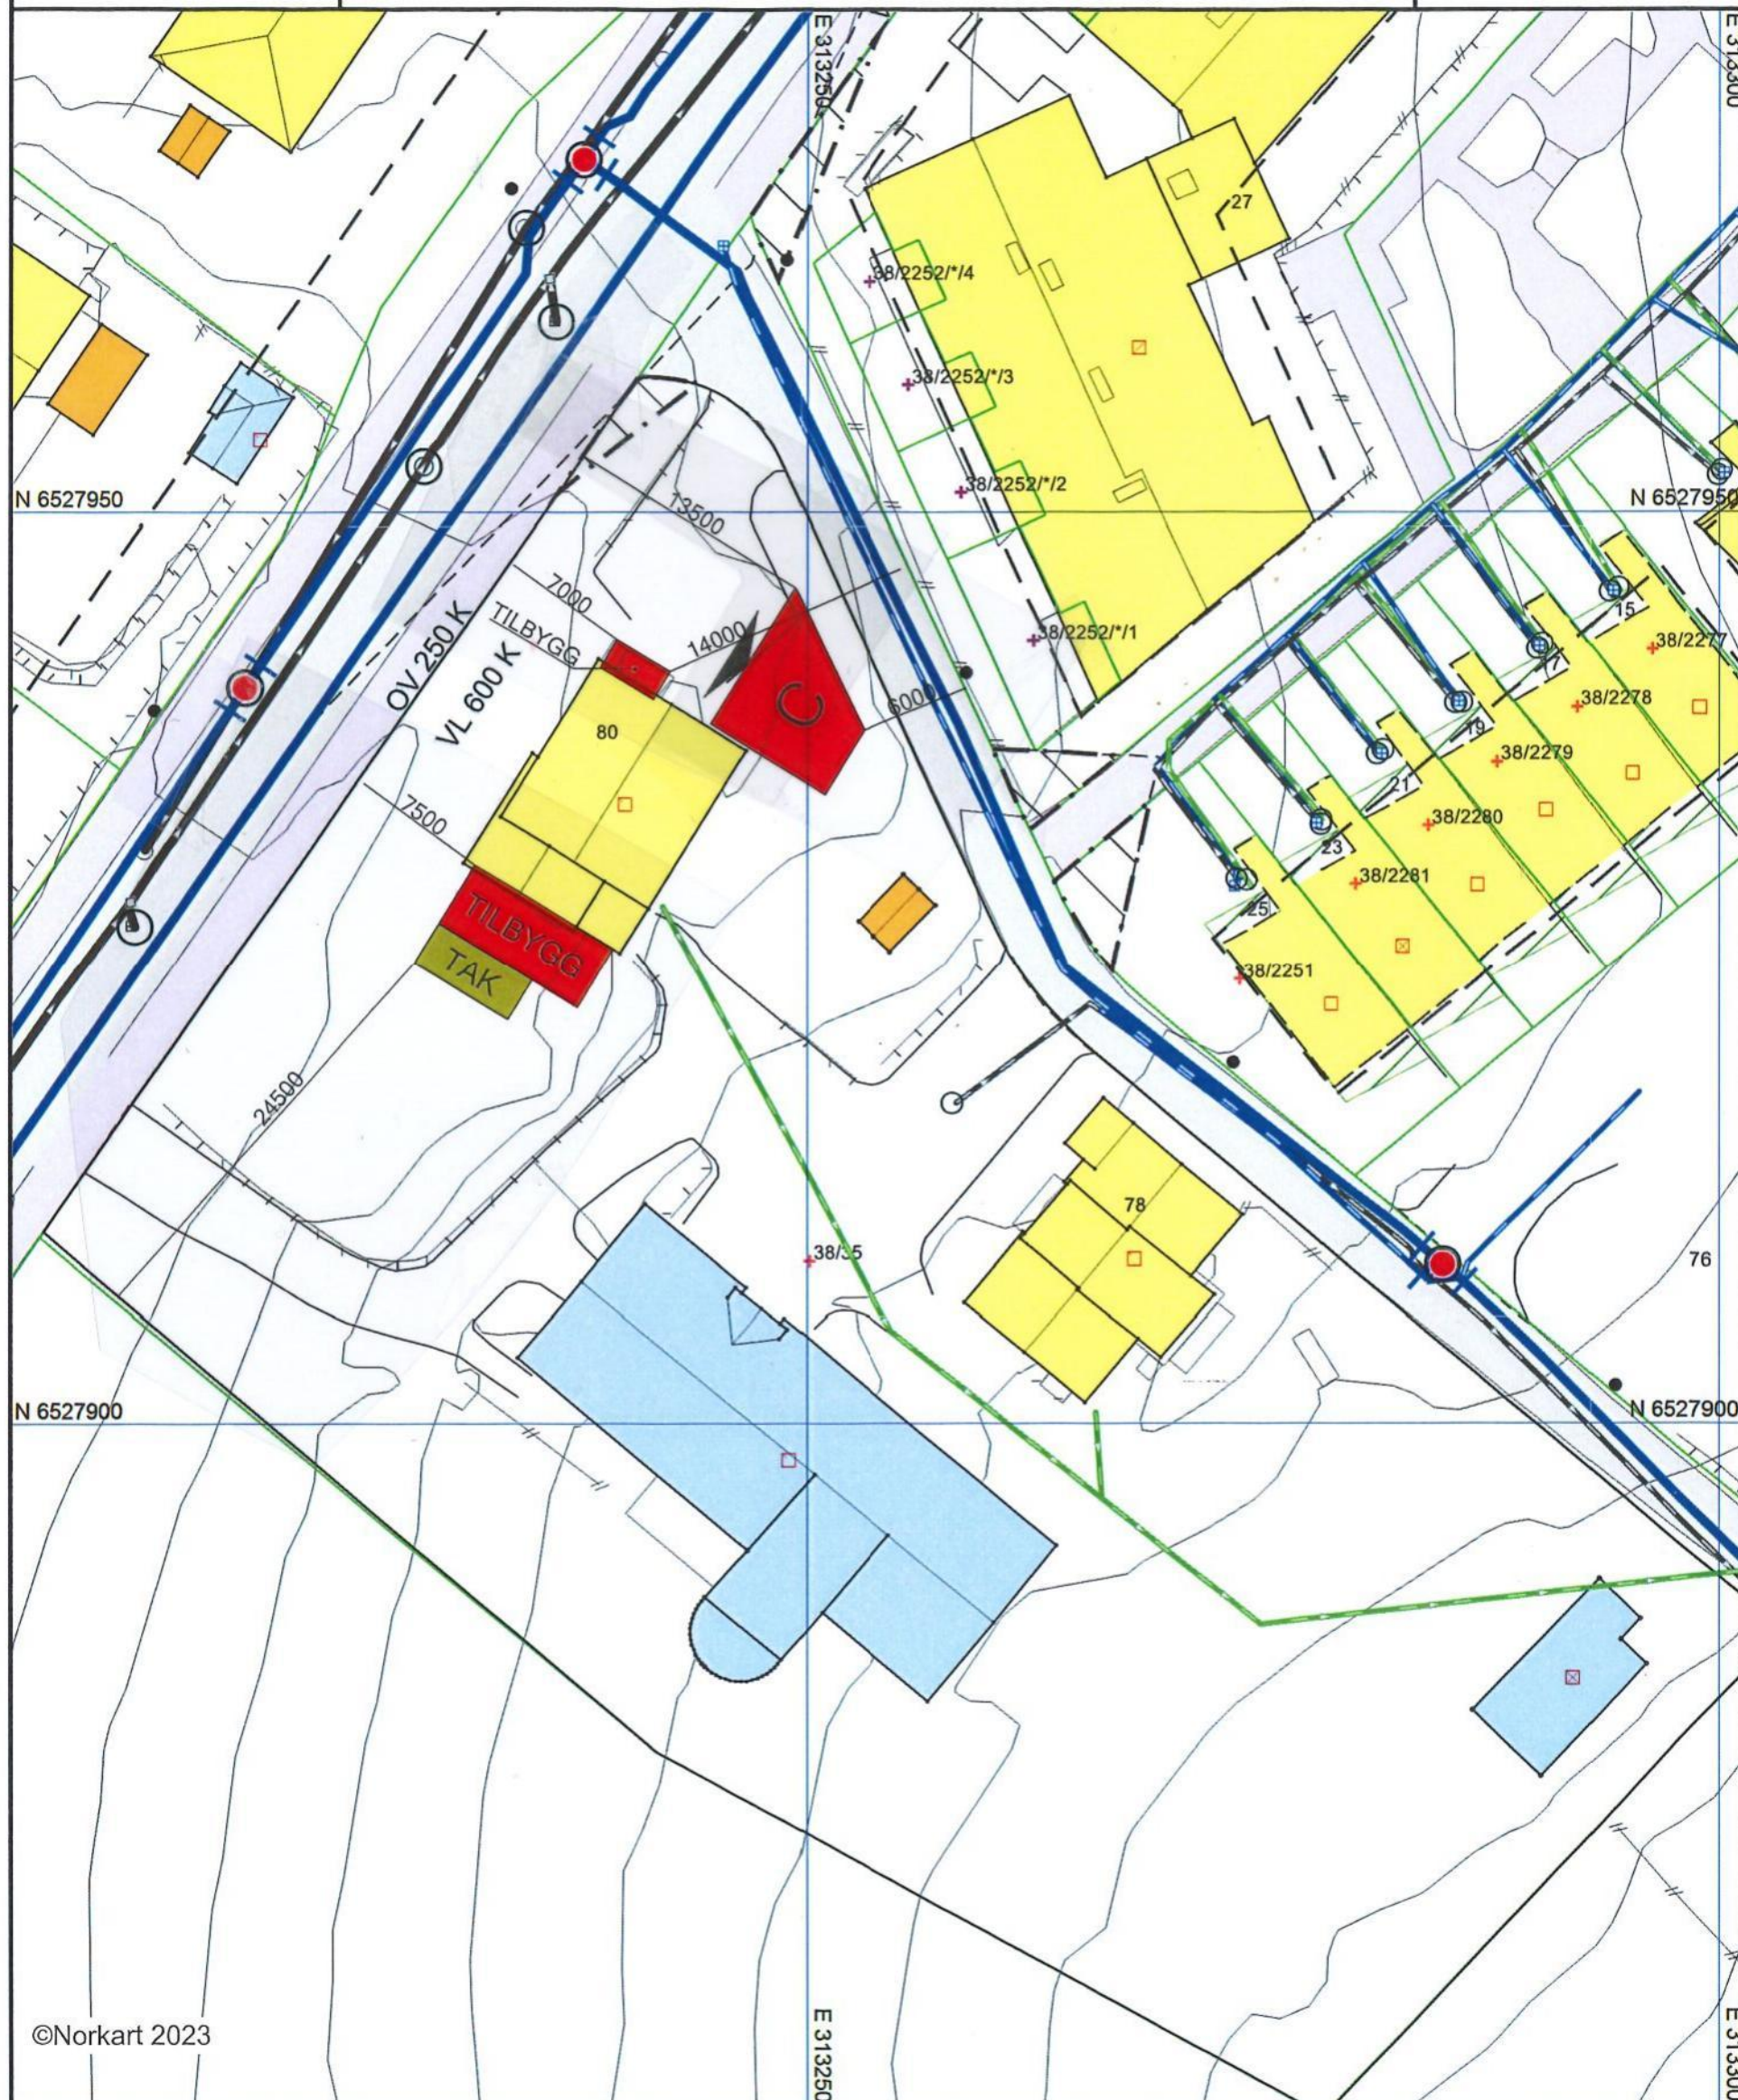

©Norkart 2023

- 1) Det tas forbehold om feil i kartgrunnlaget
- 2) Ved utskrift fra PDF-fil kan målestokken bli unøyaktig